


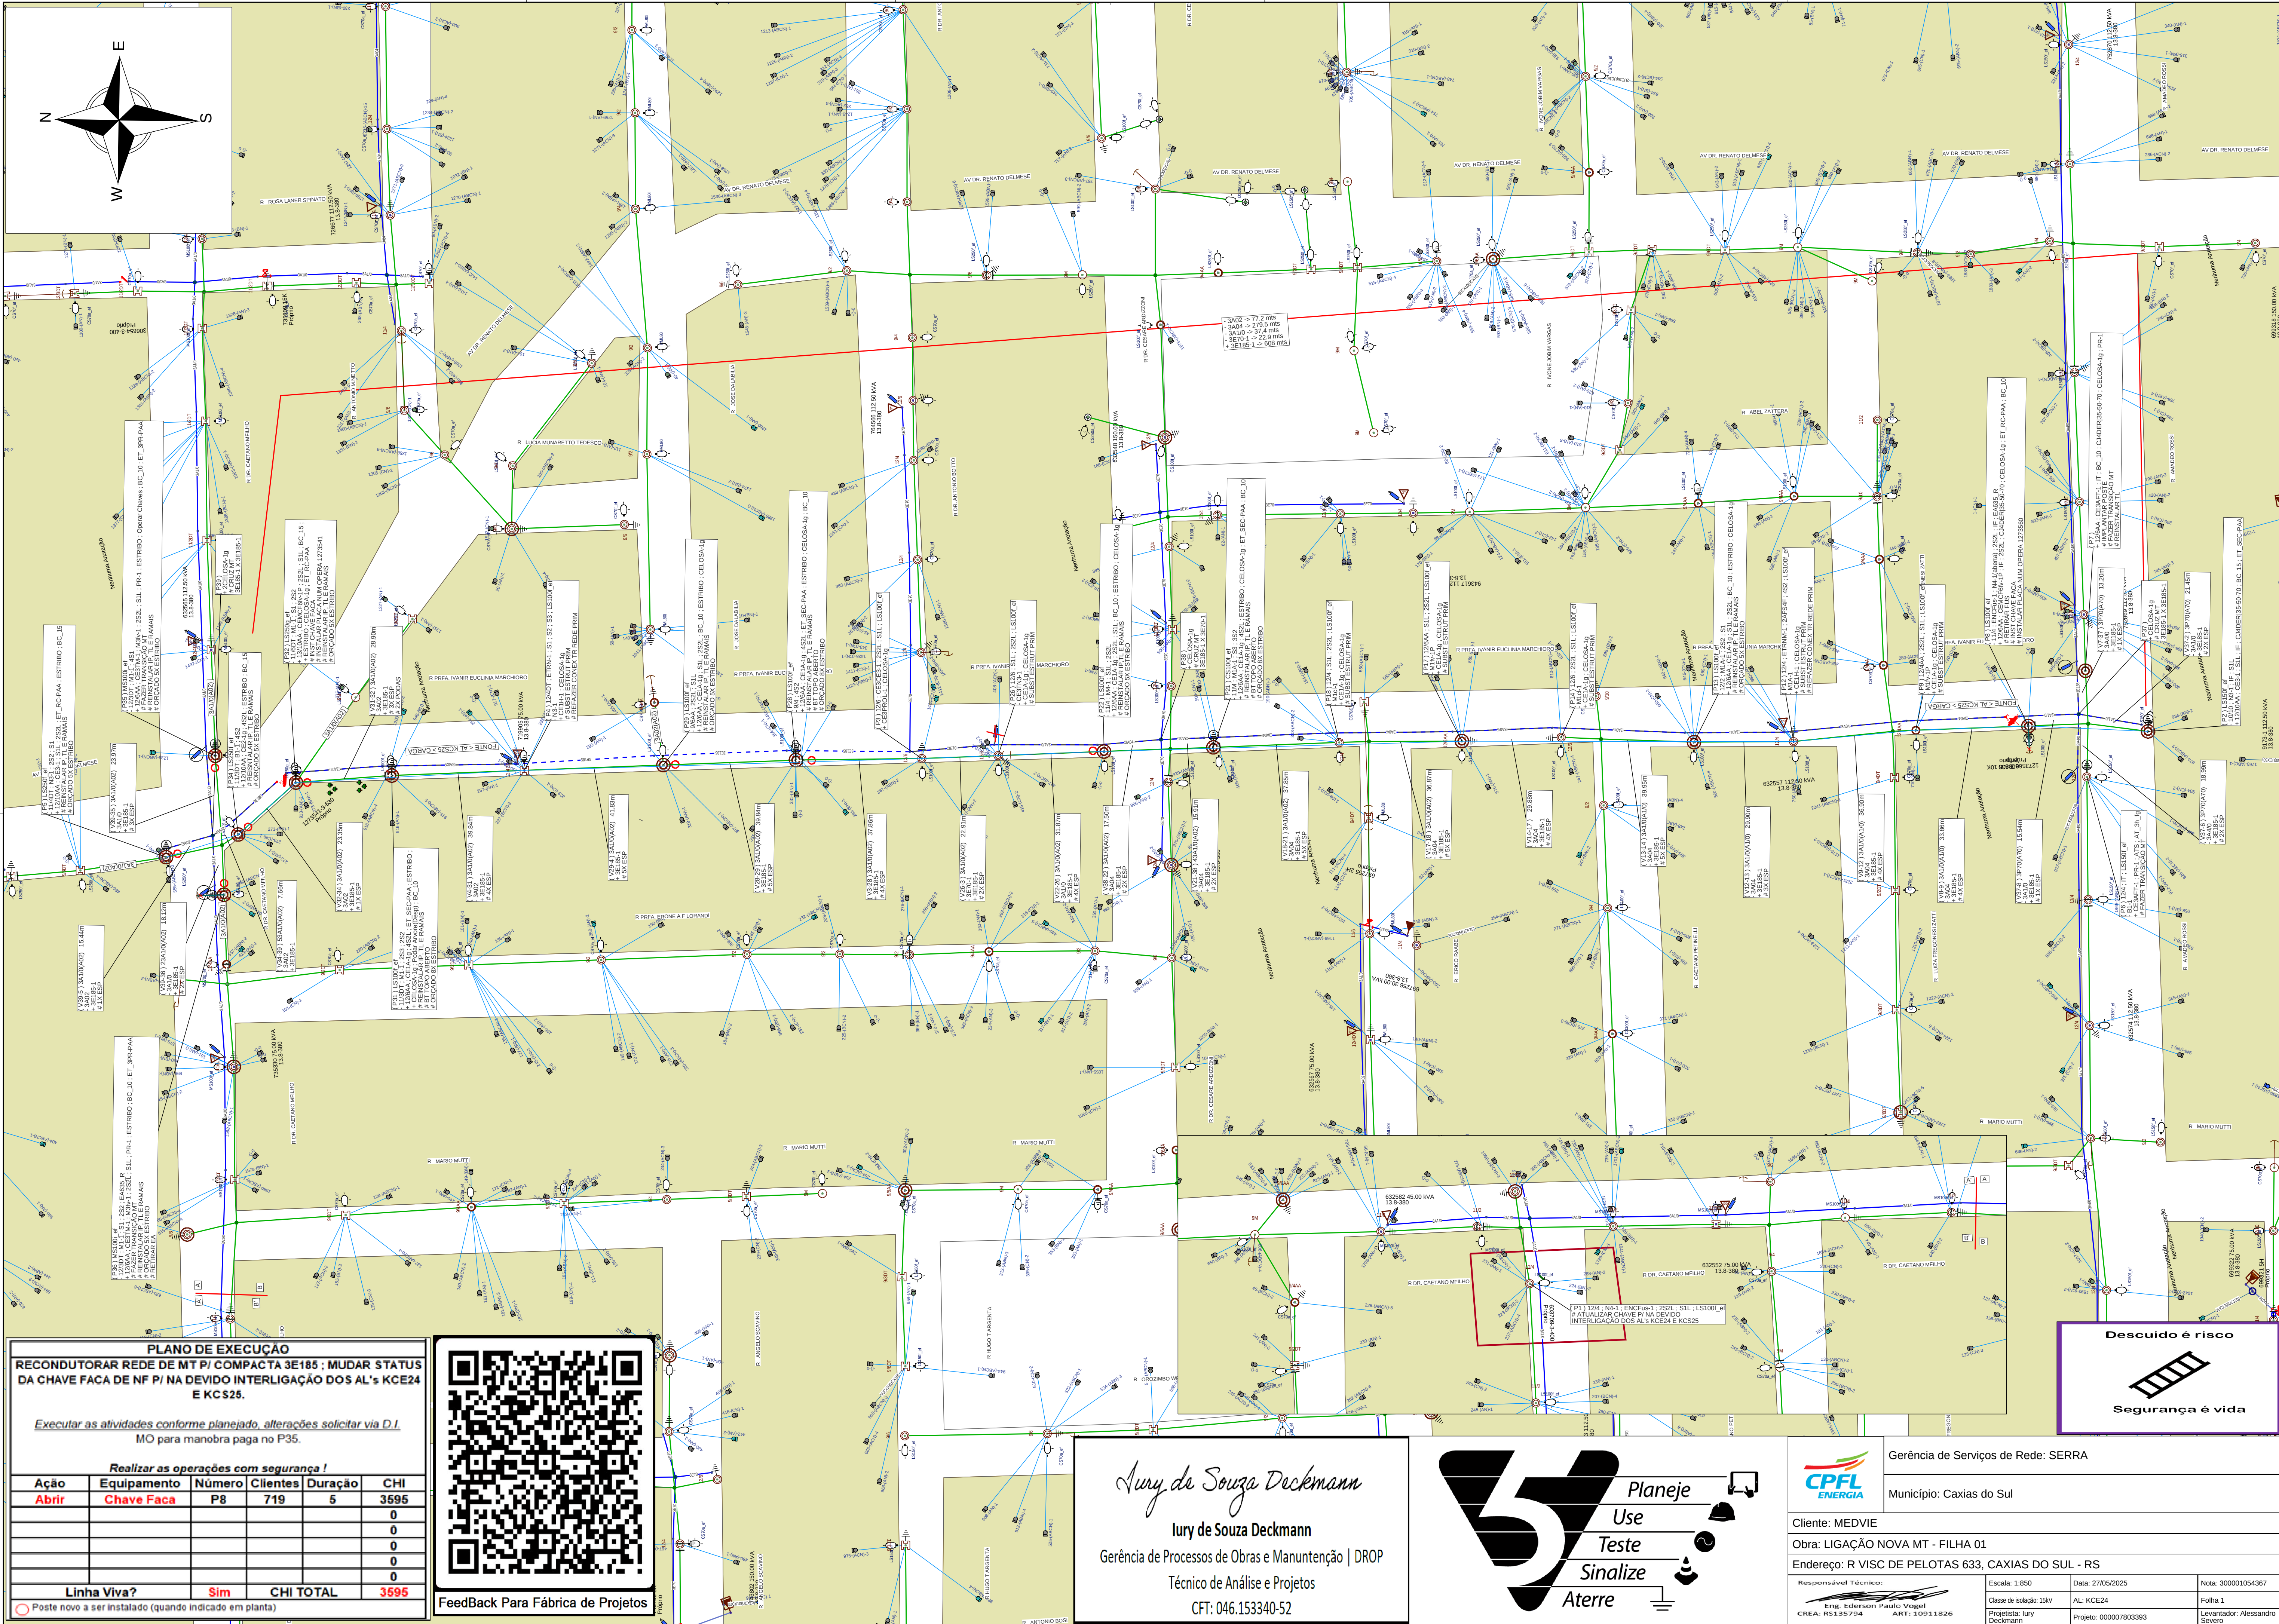

PLANO DE EXECUÇÃO
RECONDUTORAR REDE DE MT P/ COMPACTA 3E185; MUDAR STATUS DA CHAVE FACA DE NF P/ NA DEVIDO INTERLIGAÇÃO DOS AL's KCE24 E KCS25.

Executar as atividades conforme planejado, alterações solicitar via D.I. MO para manobra paga no P35.

Realizar as operações com segurança!

Ação	Equipamento	Número	Clientes	Duração	CHI
Abrir	Chave Faca	P8	719	5	3595
					0
					0
					0
					0
					0
Linha Viva?	Sim	CHI TOTAL			3595

Poste novo a ser instalado (quando indicado em planta)

FeedBack Para Fábrica de Projetos

Iury de Souza Deckmann
Iury de Souza Deckmann
Gerência de Processos de Obras e Manutenção | DROP
Técnico de Análise e Projetos
CFT: 046.153340-52

Planeje
Use
Teste
Sinalize
Aterre

Gerência de Serviços de Rede: SERRA
Município: Caxias do Sul

Cliente: MEDVIE
Obra: LIGAÇÃO NOVA MT - FILHA 01
Endereço: R VISC DE PELOTAS 633, CAXIAS DO SUL - RS

Responsável Técnico:
Eng. Ederson Paulo Vogel
CREA: RS195794

Escala: 1:850
Data: 27/05/2025
Classe de Isolção: 18kV
AL: KCE24
Projeto: 000007803393

Nota: 300001405367
Folha 1
Levantador: Alessandro Severo

Descuido é risco

Segurança é vida