


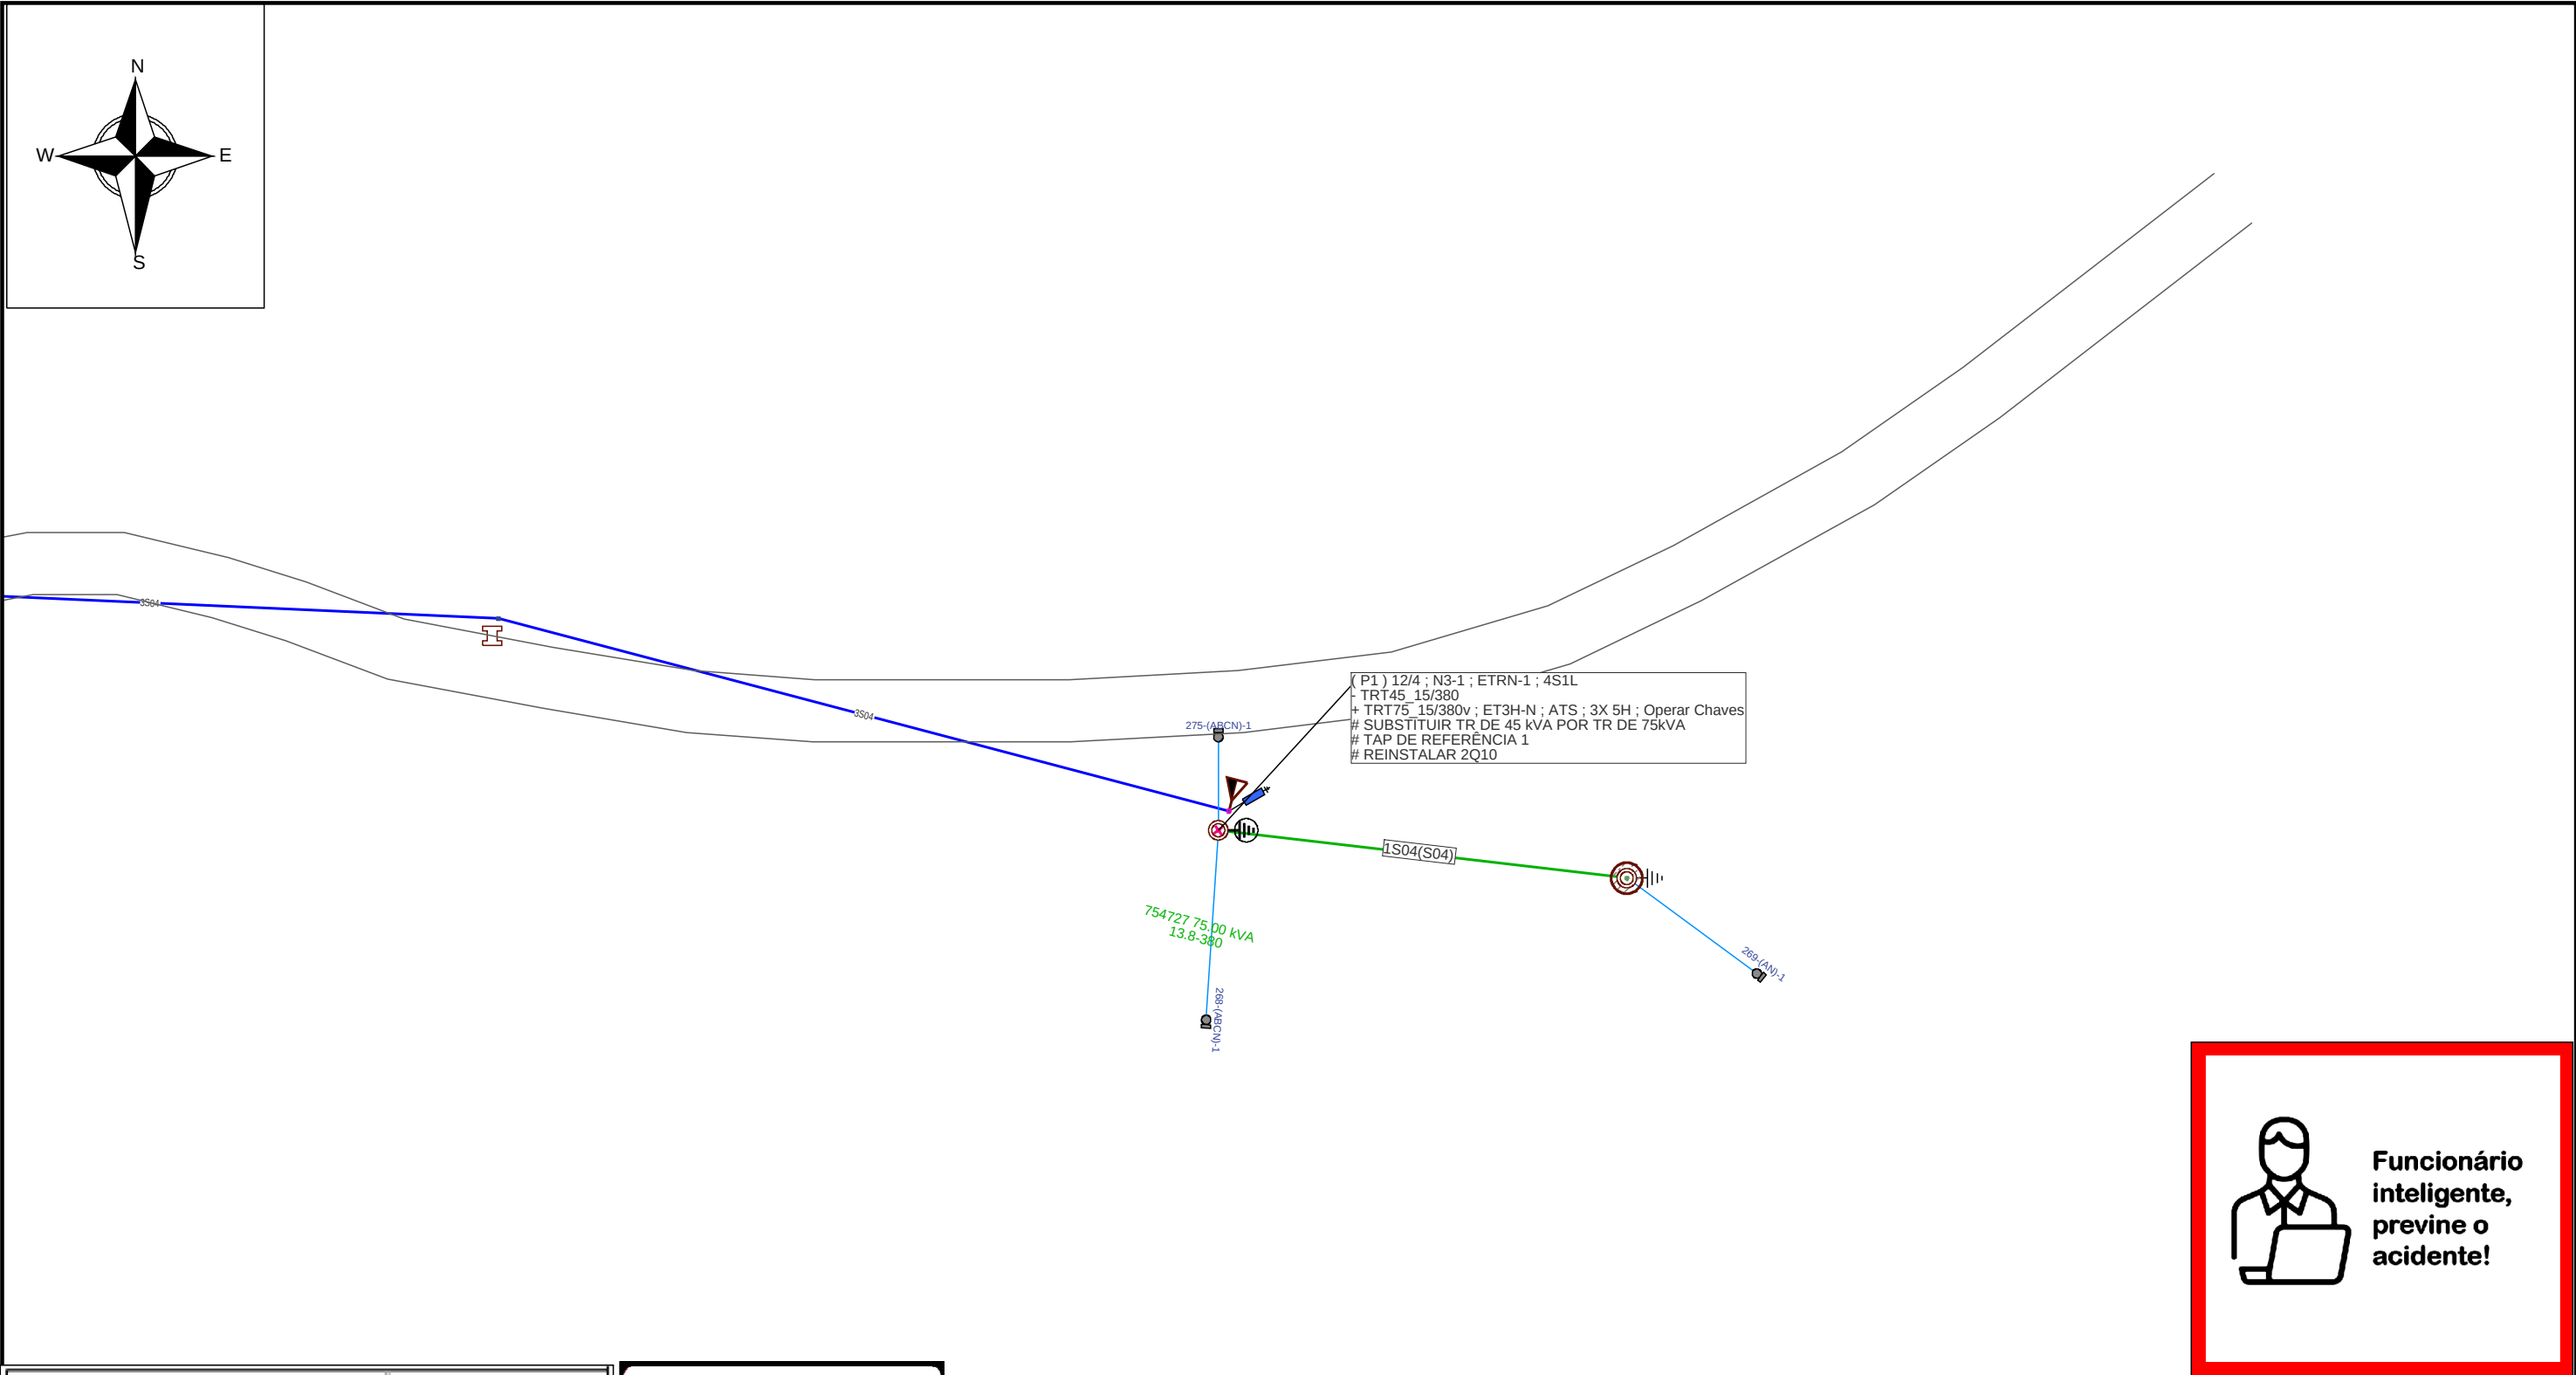

PLANO DE EXECUÇÃO					
Manobrar equipamentos abaixo para realizar obra.					
Ação	Equipamento	Número	Clientes	Duração	CHI
Abrir	Chave Fusível	754726	3	5	15
Linha Viva?		Não	CHI TOTAL		15
☐ Poste novo a ser instalado (quando indicado em planta)					

FeedBack Para Fábrica de Projetos

Wellerson Avila

Wellerson Amaral Avila

Gerência de Processos de Obras e Manutenção | DROP

Técnico de Análise e Projetos

CFT: 04993185014

Gerência de Obras e Manutenção

Município: São Marcos

Cliente: UESLEN SPIGOLON

Obra: ALTERAÇÃO DE FASE BT - RURAL

Endereço: EST ZON CAMPO 275 95190-000 SAO MARCOS BR RS

Responsável Técnico:

Eng. Ederson Paulo Vogel
CREA: RS135794 ART: 10911826

Escala: 1:850

Classe de isolamento: 15kV

Projetista: Wellerson Avila

Data: 04/06/2025

AL: SMC13

Projeto: 000007810629

Nota: 300001055109

Folha 1

Levantador Marcio Bedin