


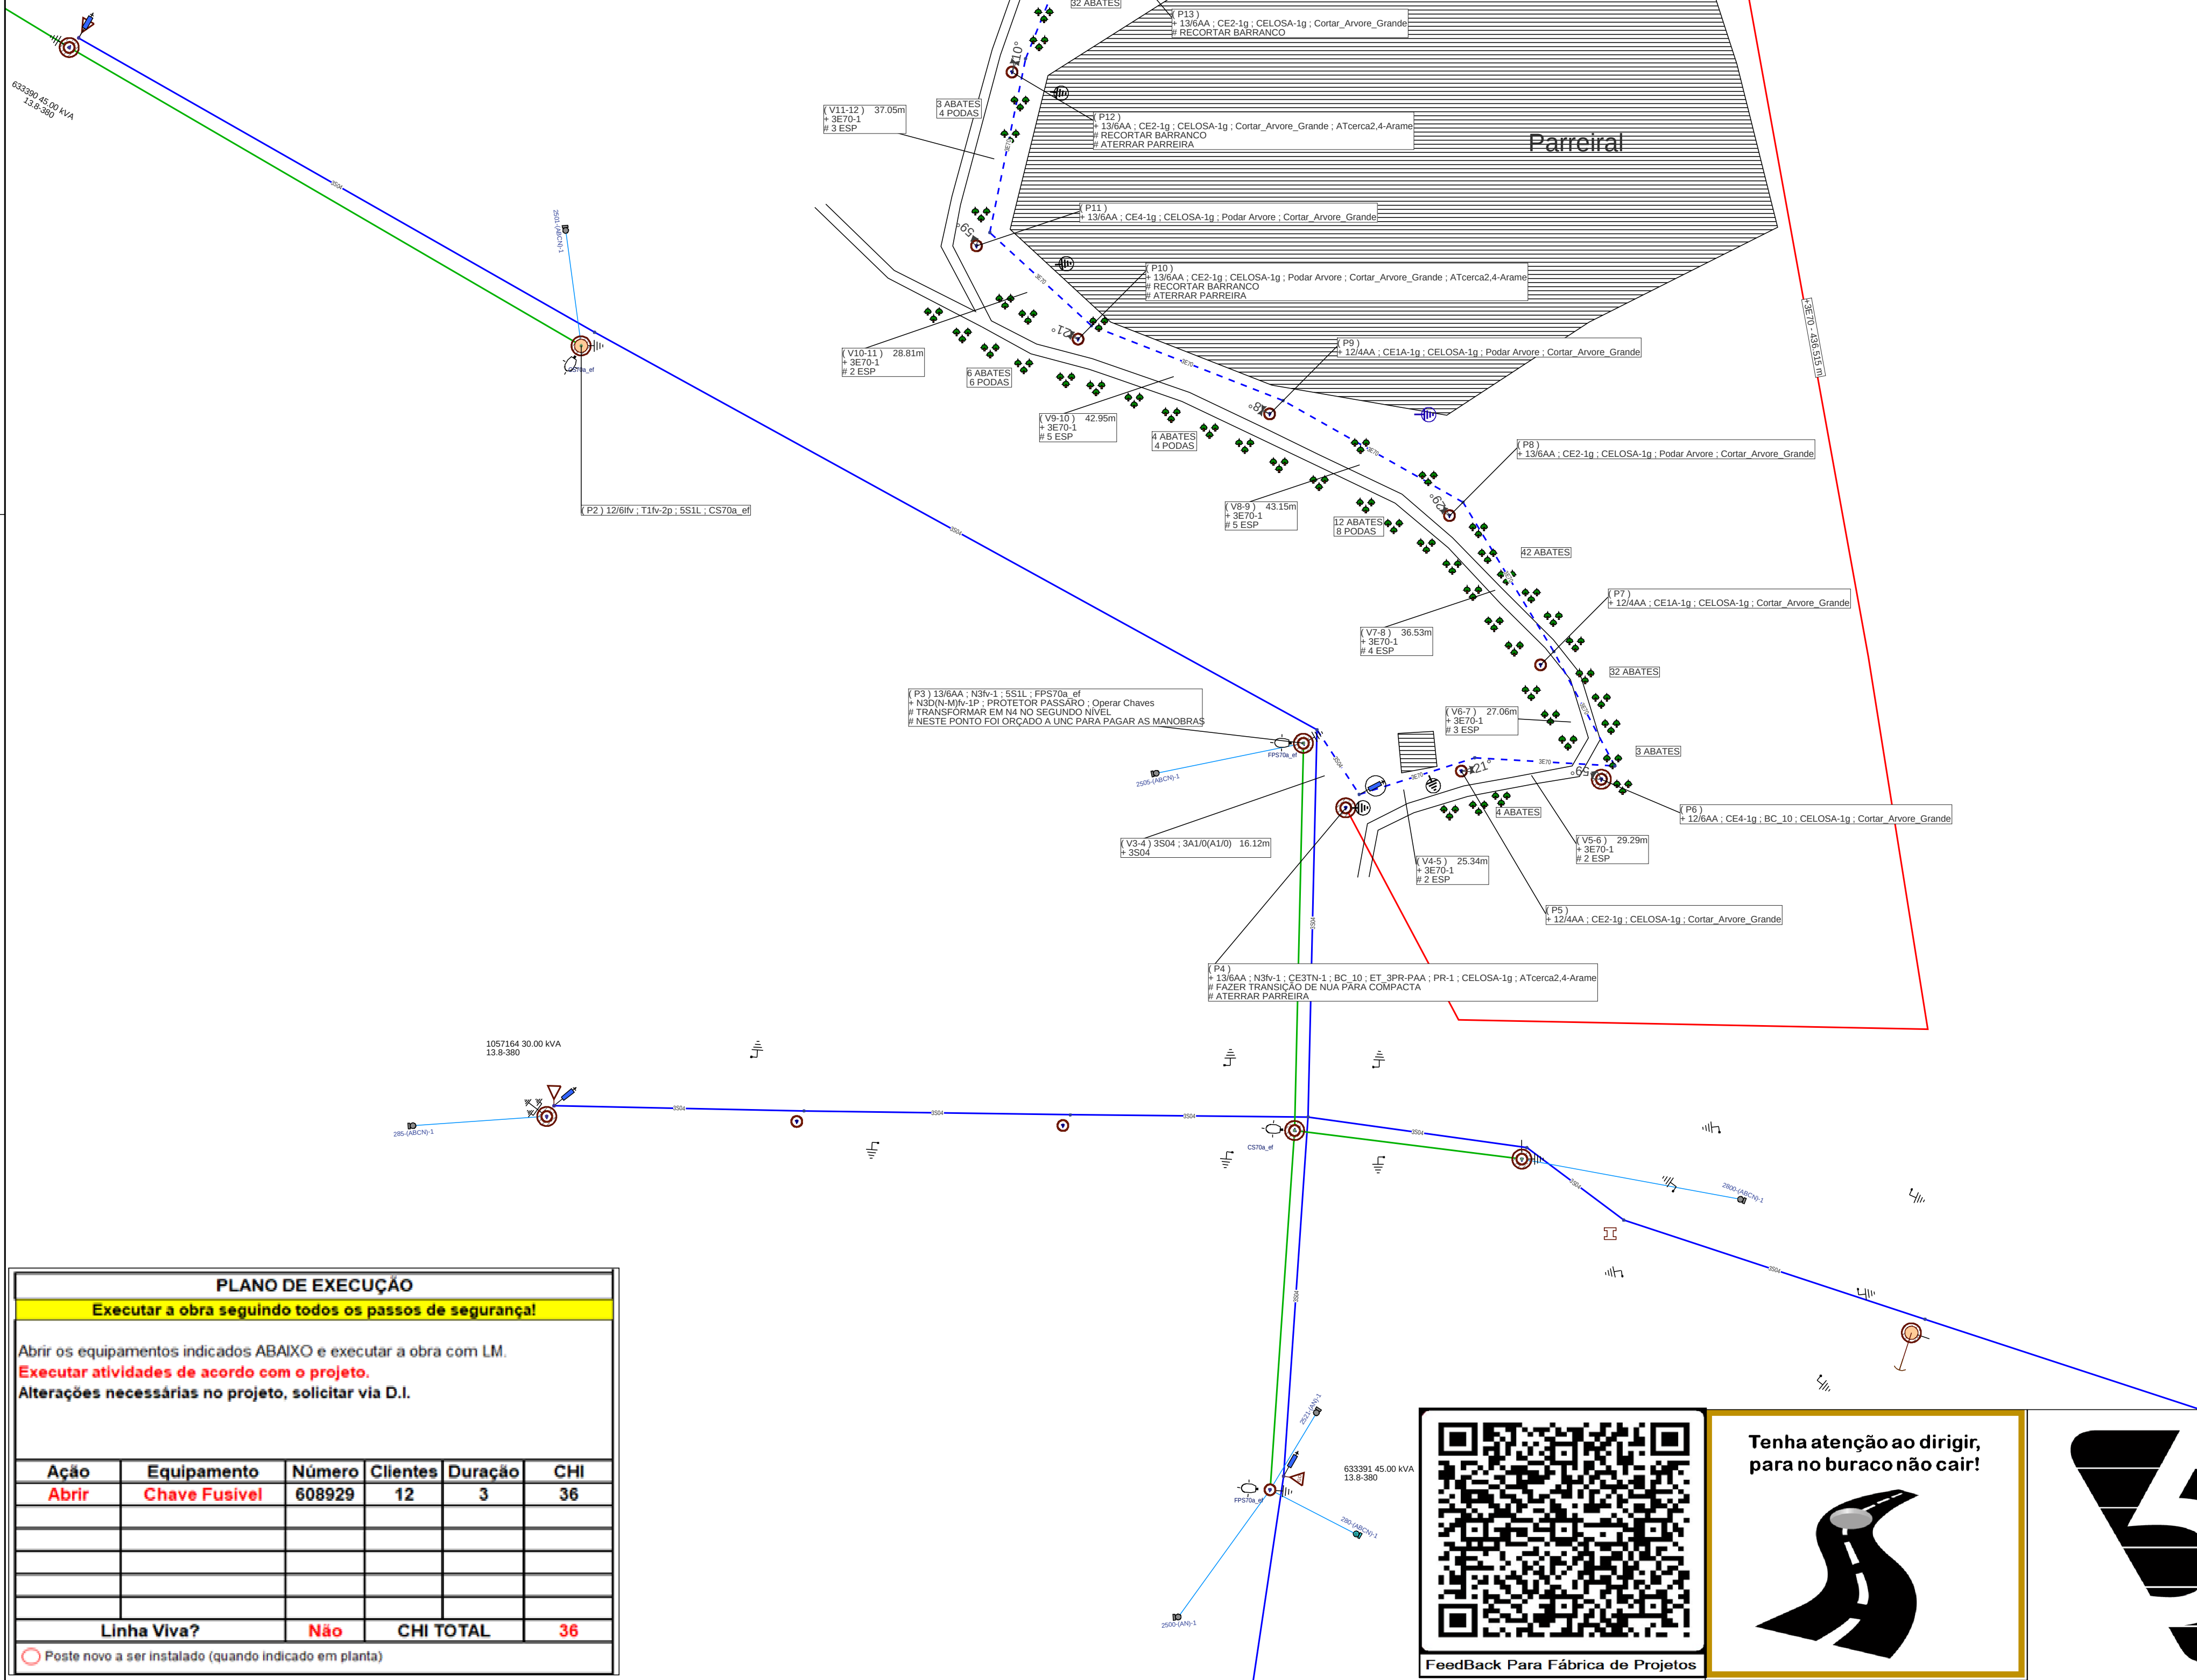

PLANO DE EXECUÇÃO					
Executar a obra seguindo todos os passos de segurança!					
Abrir os equipamentos indicados ABAIXO e executar a obra com LM.					
Executar atividades de acordo com o projeto.					
Alterações necessárias no projeto, solicitar via D.I.					
Ação	Equipamento	Número	Clientes	Duração	CHI
Abrir	Chave Fusivel	608929	12	3	36
Linha Viva?		Não	CHI TOTAL		36

☐ Poste novo a ser instalado (quando indicado em planta)

Luana Candido da Silva
Luana Candido da Silva
rência de Processos de Obras e Manutenção | DRC
Técnico de Análise e Projetos
CFT: 025.291.090-79

Gerência de Serviços de Rede: SERRA

Município: Caxias do Sul

Cliente: JUARES PEROCHIN - Telefone: (54) 9 9932-2358

Obra: LIGAÇÃO NOVA BT - RURAL

Endereço: EST MUN S VALENTIM 2502 95074-870 CAXIAS DO SUL BR RS

Responsável Técnico:	
----------------------	--

Escala: 1:85

Data: 22/07/2025

Nota: 300001055698

Eng. Ederson Paulo Vogel
CREA: RS135794 ART: 1091182

Escala: 1:85

Data: 22/07/2025

Nota: 300001055698

Classe de isolan

AL: CXG12

Folha 1



**Tenha atenção ao dirigir,
para no buraco não cair!**

