

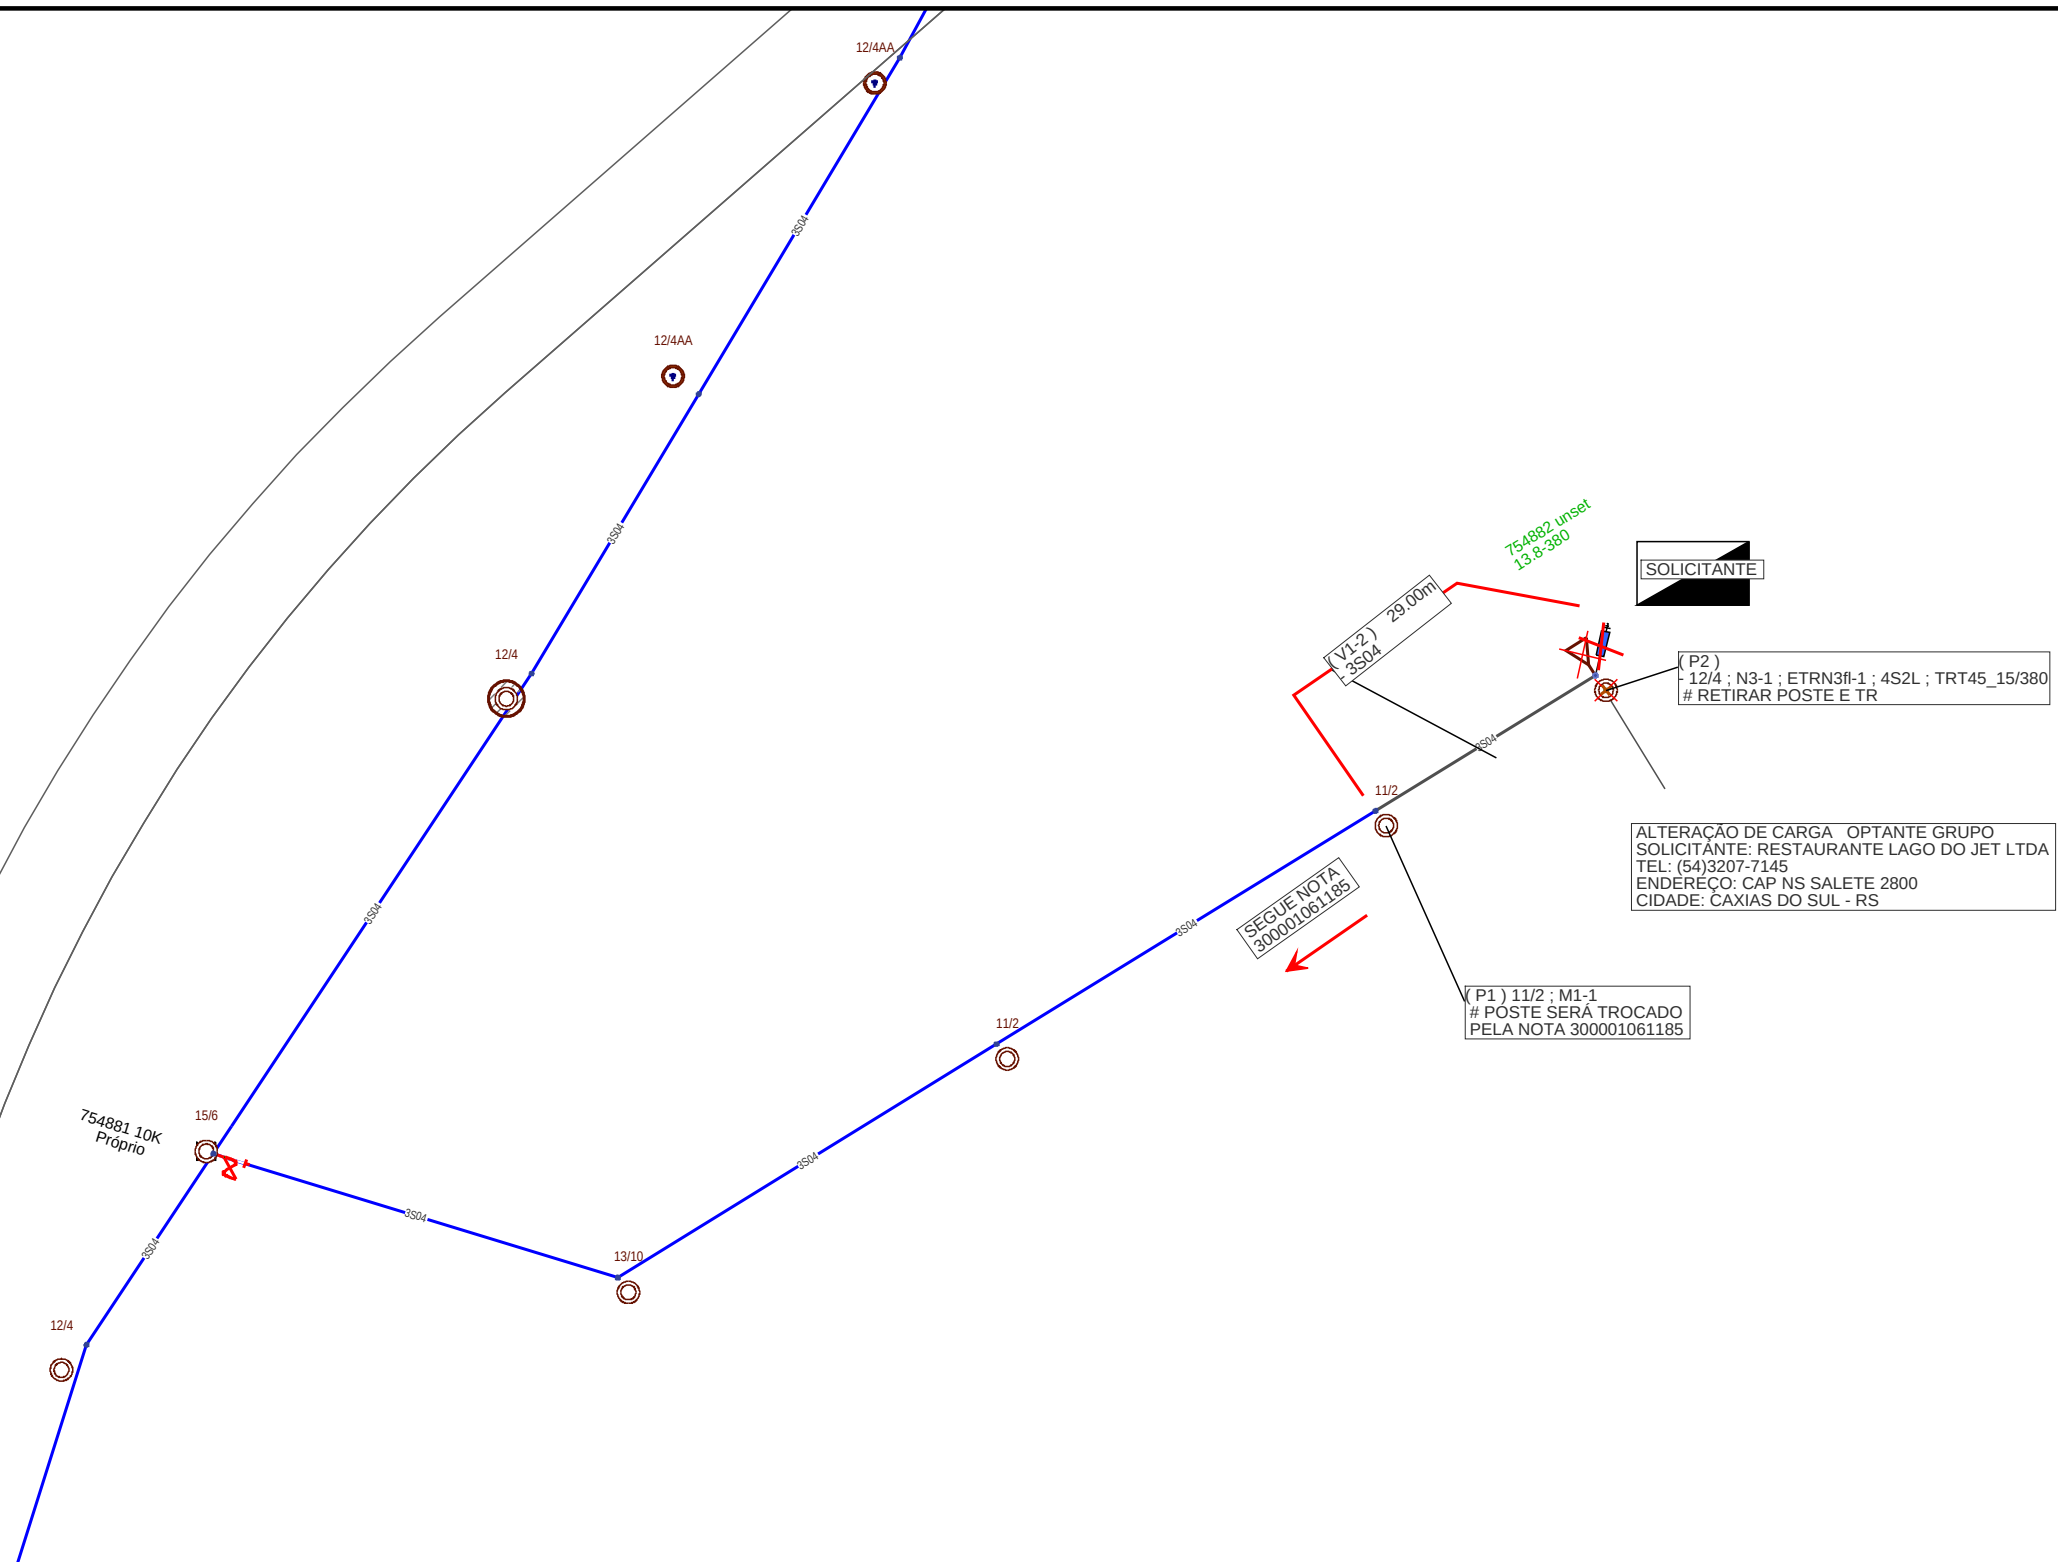


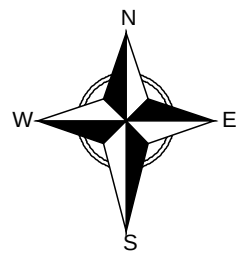

Descuido é risco

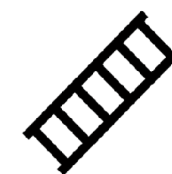

Segurança é vida

PLANO DE EXECUÇÃO

P2: RETIRAR TR E POSTE ; DESLIGAMENTO PREVISTO NA NOTA 300001061185.

Executar as atividades conforme planejado, alterações solicitar via D.I


Realizar as operações com segurança !

[illegible]

Linha Viva?	Não	(
☐ Poste novo a ser instalado (quando indicado em planta)		



FeedBack Para Fábrica de Projetos

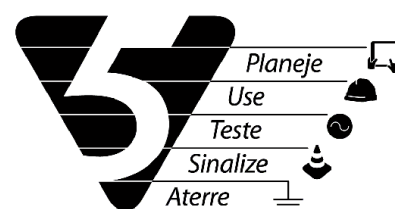

Aury de Souza Deckmann

Iury de Souza Deckmann
Gerência de Processos de Obras e Manutenção | DROP

CFT: 046.153340-52



Gerência de Obras e Manutenção

Município: Caxias do Sul

Cliente: RESTAURANTE LAGO DO JET LTDA

Obra: ALTERAÇÃO DE CARGA OPTANTE GRUPO - F2

Endereço: CAP NS SALETE 2800, CAXIAS DO SUL - RS

Responsável Técnico:

Eng. Ederson Paulo Vogel
CREA: RS135794 ART: 10911826

Escala: 1:850

Data: 20/06/2025

Nota:	300001061186
-------	--------------

Classe de isolação:
15kV

AL: FAR54

Folha 1

Projekta: Iury Deckmann

Projeto: 000007818944

Levantador: Ricardo Quevedo
