
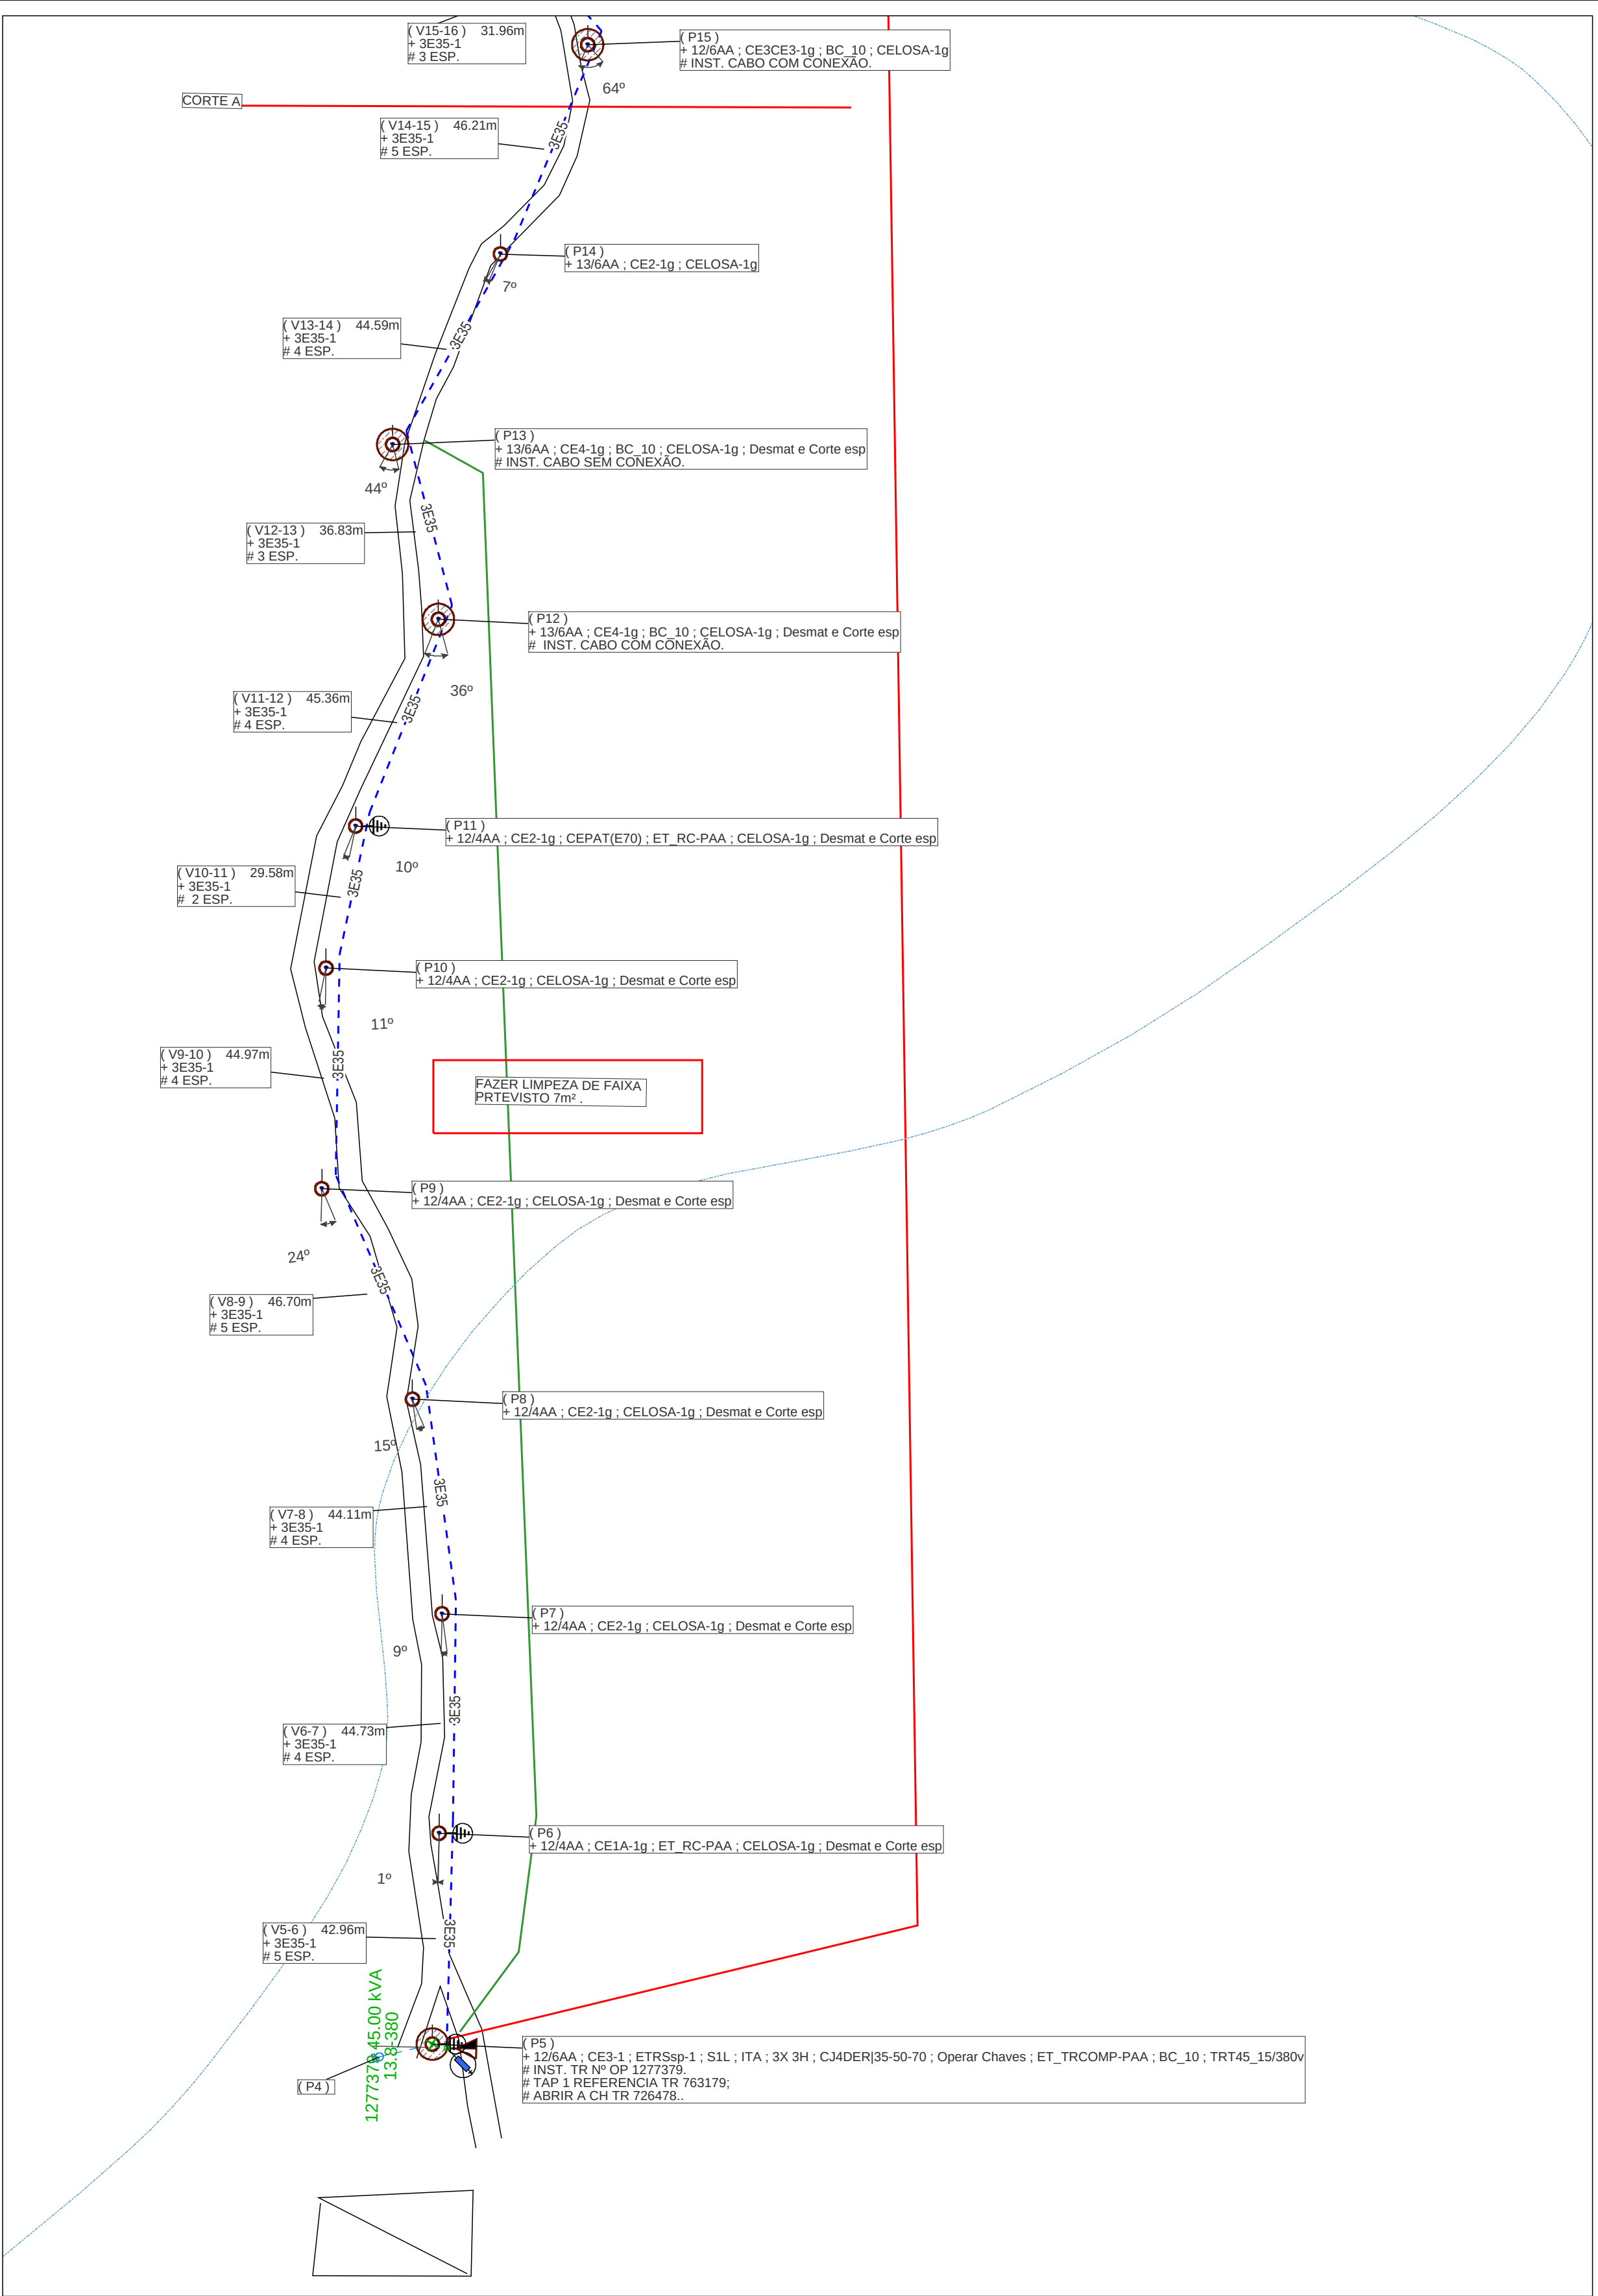
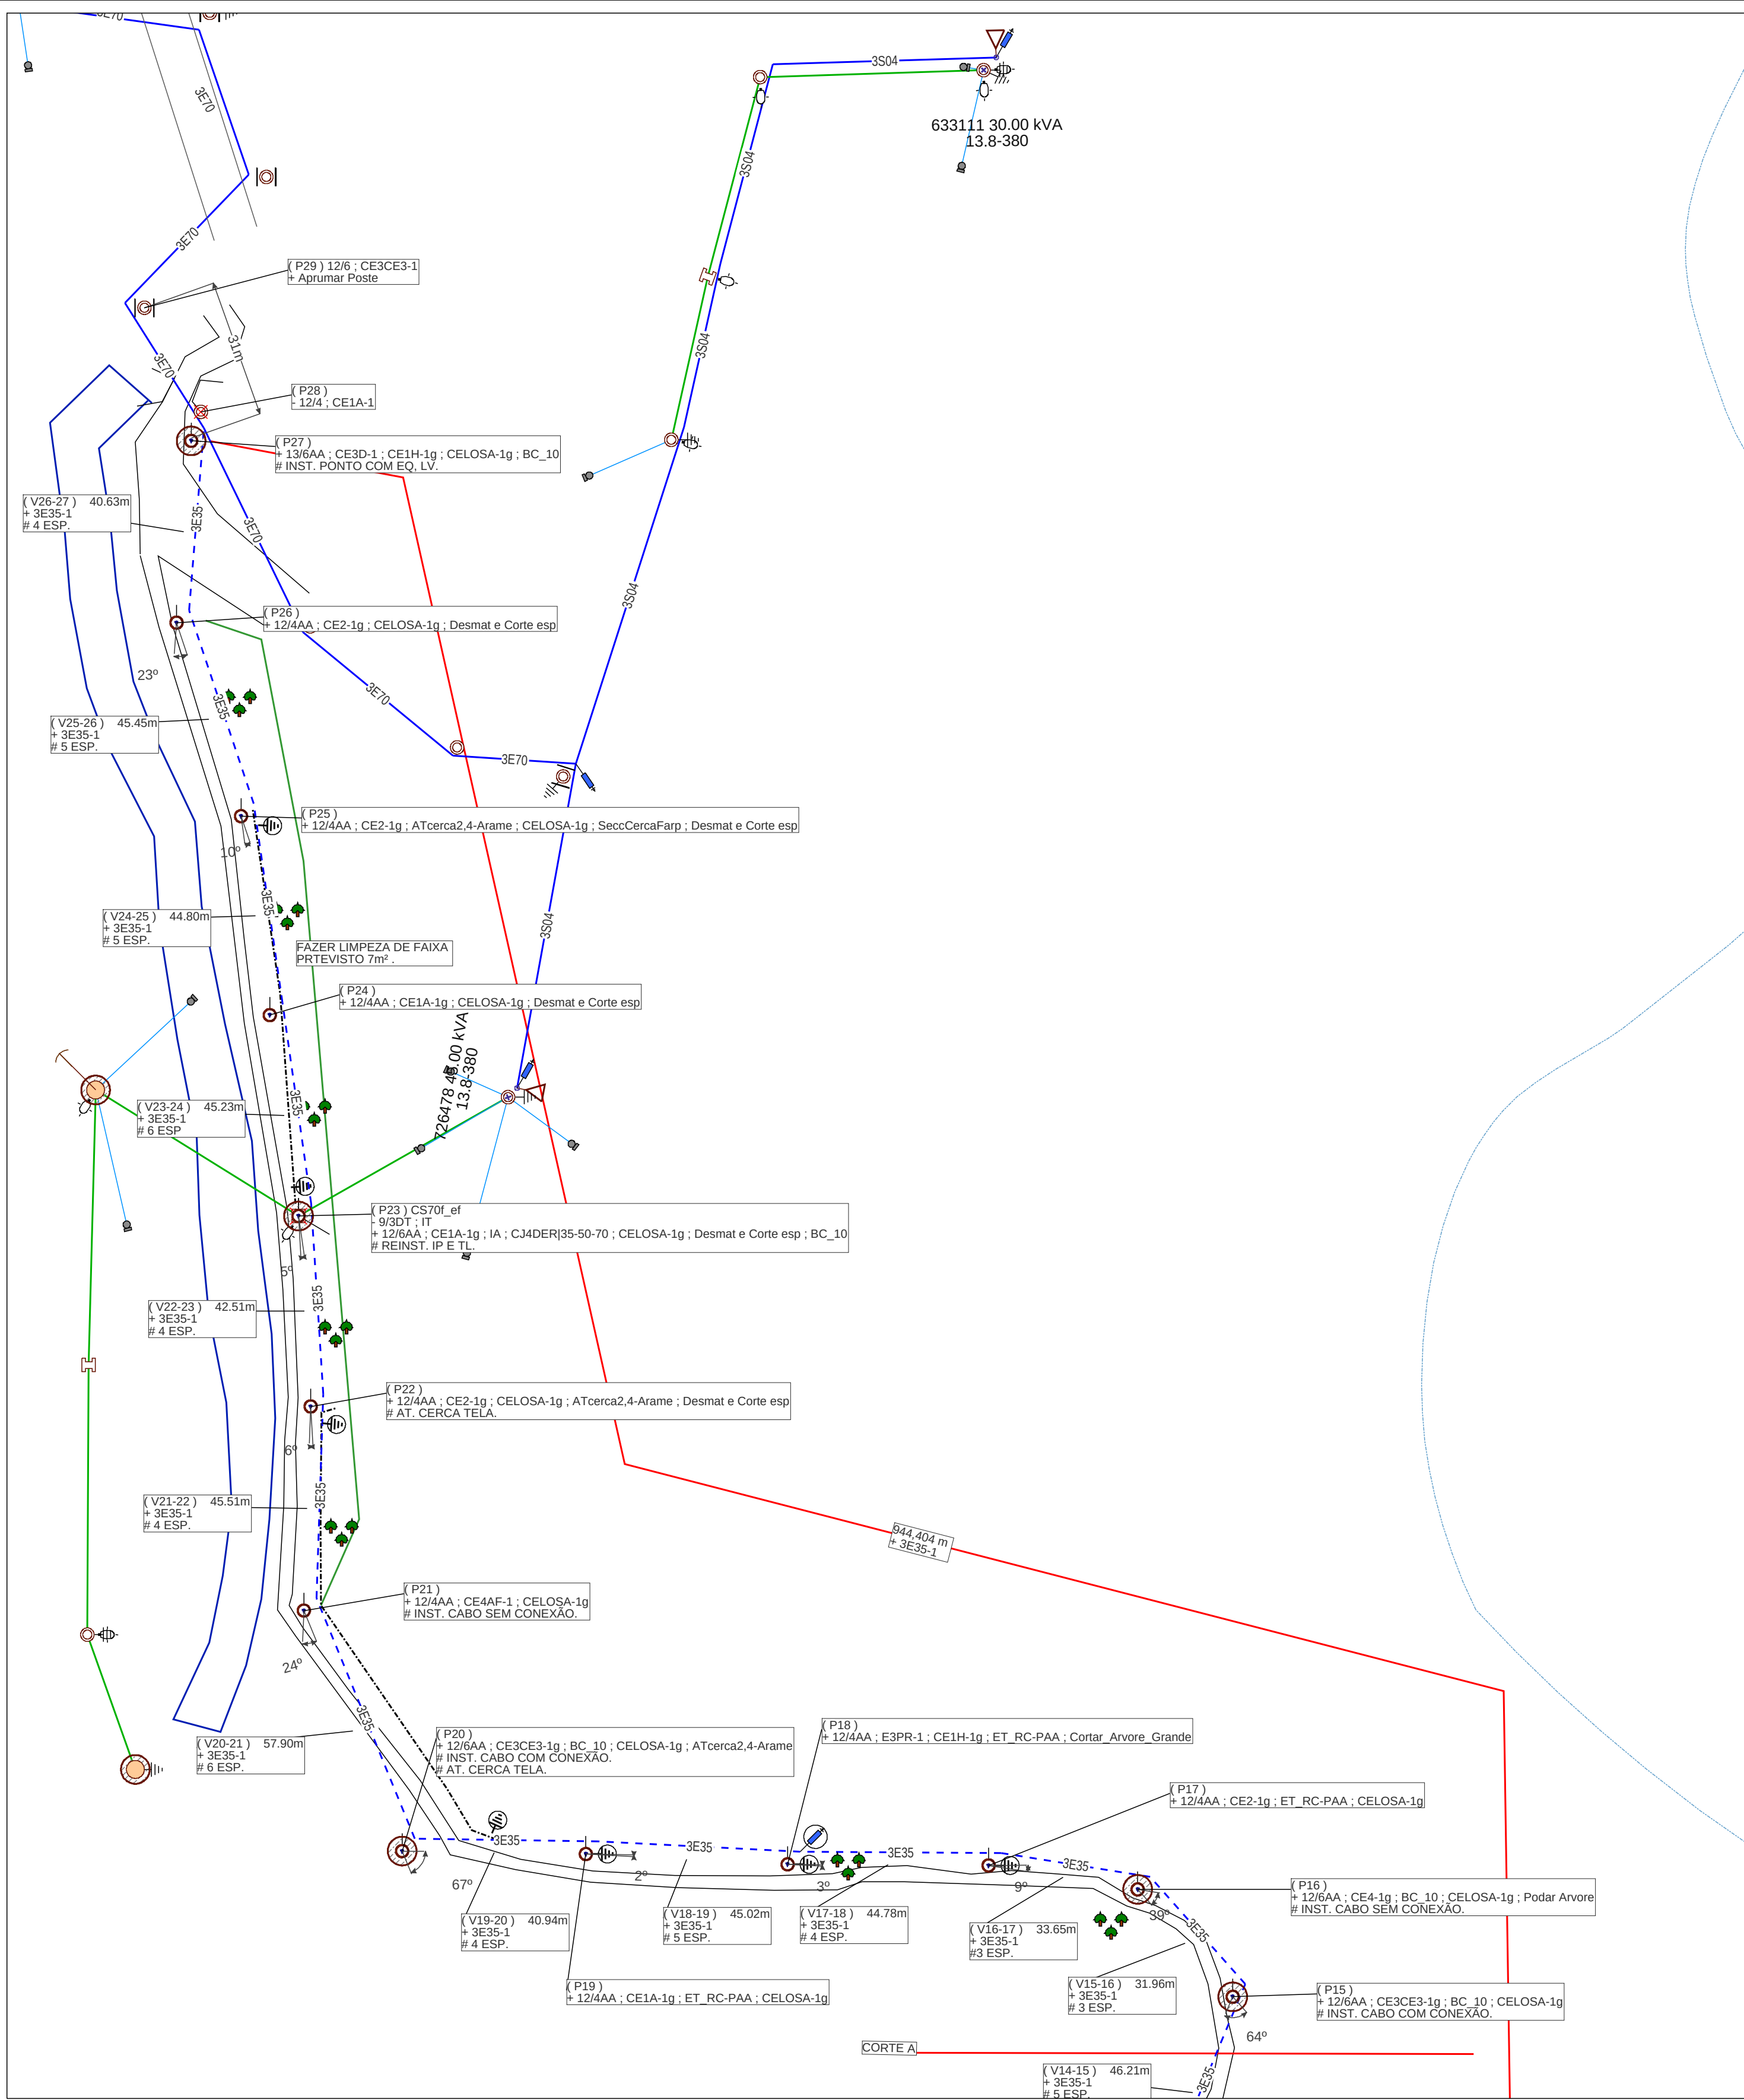


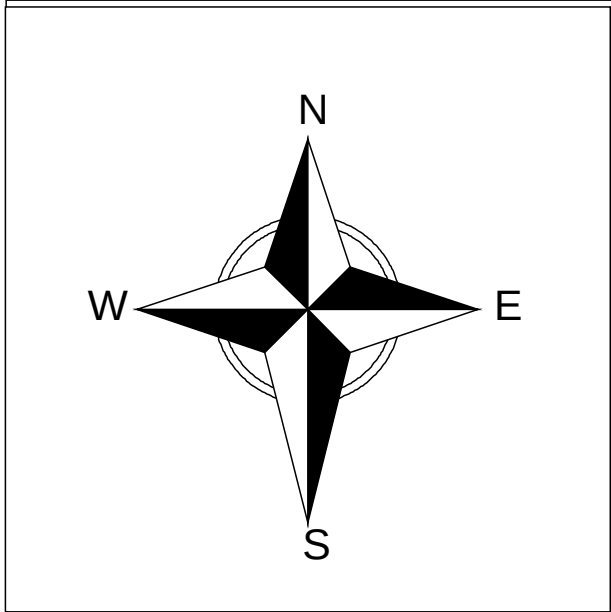

Atenção Licença Ambiental

Executar conforme Licença Ambiental anexada no SAP


Gerência de Processos de Obras e Manutenção | DROF

Técnico de Análise e Projetos

CFT: 837.082.780-20

PLANO DE EXECUÇÃO					
Executar a instalar de postes, extensão de rede MT, instalação de TR, para aligação nova BT, conforme projetado.					
Sugestão de monbra abaixo, com auxílio de eq. LV.					
Ação	Equipamento	Número	Clientes	Duração	CHI
Abriu	Transformador	726478	7	4	28
					0
					0
					0
					0
					0
Linha Viva?		Sim	CHI TOTAL		28
☐ Poste novo a ser instalado (quando indicado em planta)					
Inserir Nota	300001062315				

FeedBack Para Fábrica de Projetos

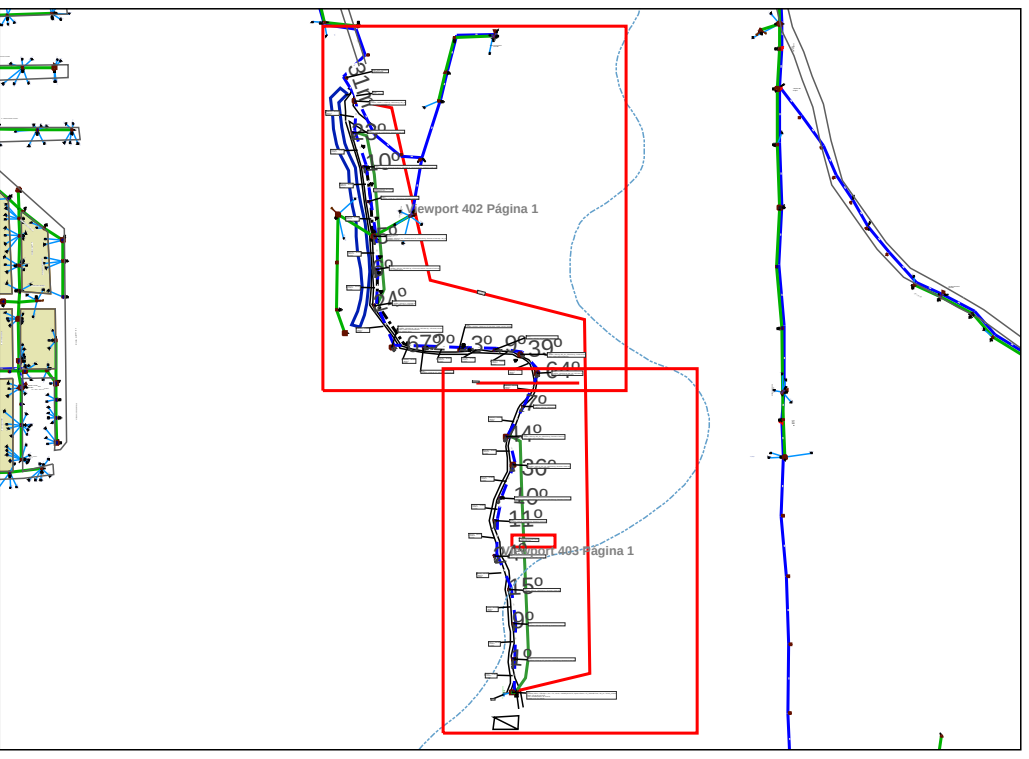

Funcionário inteligente, previne o acidente!

Planeje Use Teste Sinalize Aterre

Gerência de Obras e Manutenção		
Município: Caxias do Sul		
Cliente: PATNA PASTORAL DE APOIO AO TOXICOMANO NO		
Obra: ALTERAÇÃO DE FASE BT - RURAL		
Endereço: EST MUN JOAO ORESTES FAORO 120 95095-125 CAXIAS DO SUL BR RS		
Responsável Técnico:	Escala: 1:1000	Data: 18/07/2025
Eng. Ederson Paulo Vogel	Classe de Isolção: 15kV	AL: CXG24
CREA: RS195794	Projeto: TIAGO FAVERON	Folha 1
ART: 10911826	Projeto: 000007822431	Levantador: Adelar Miguel Ferreira Grafe