


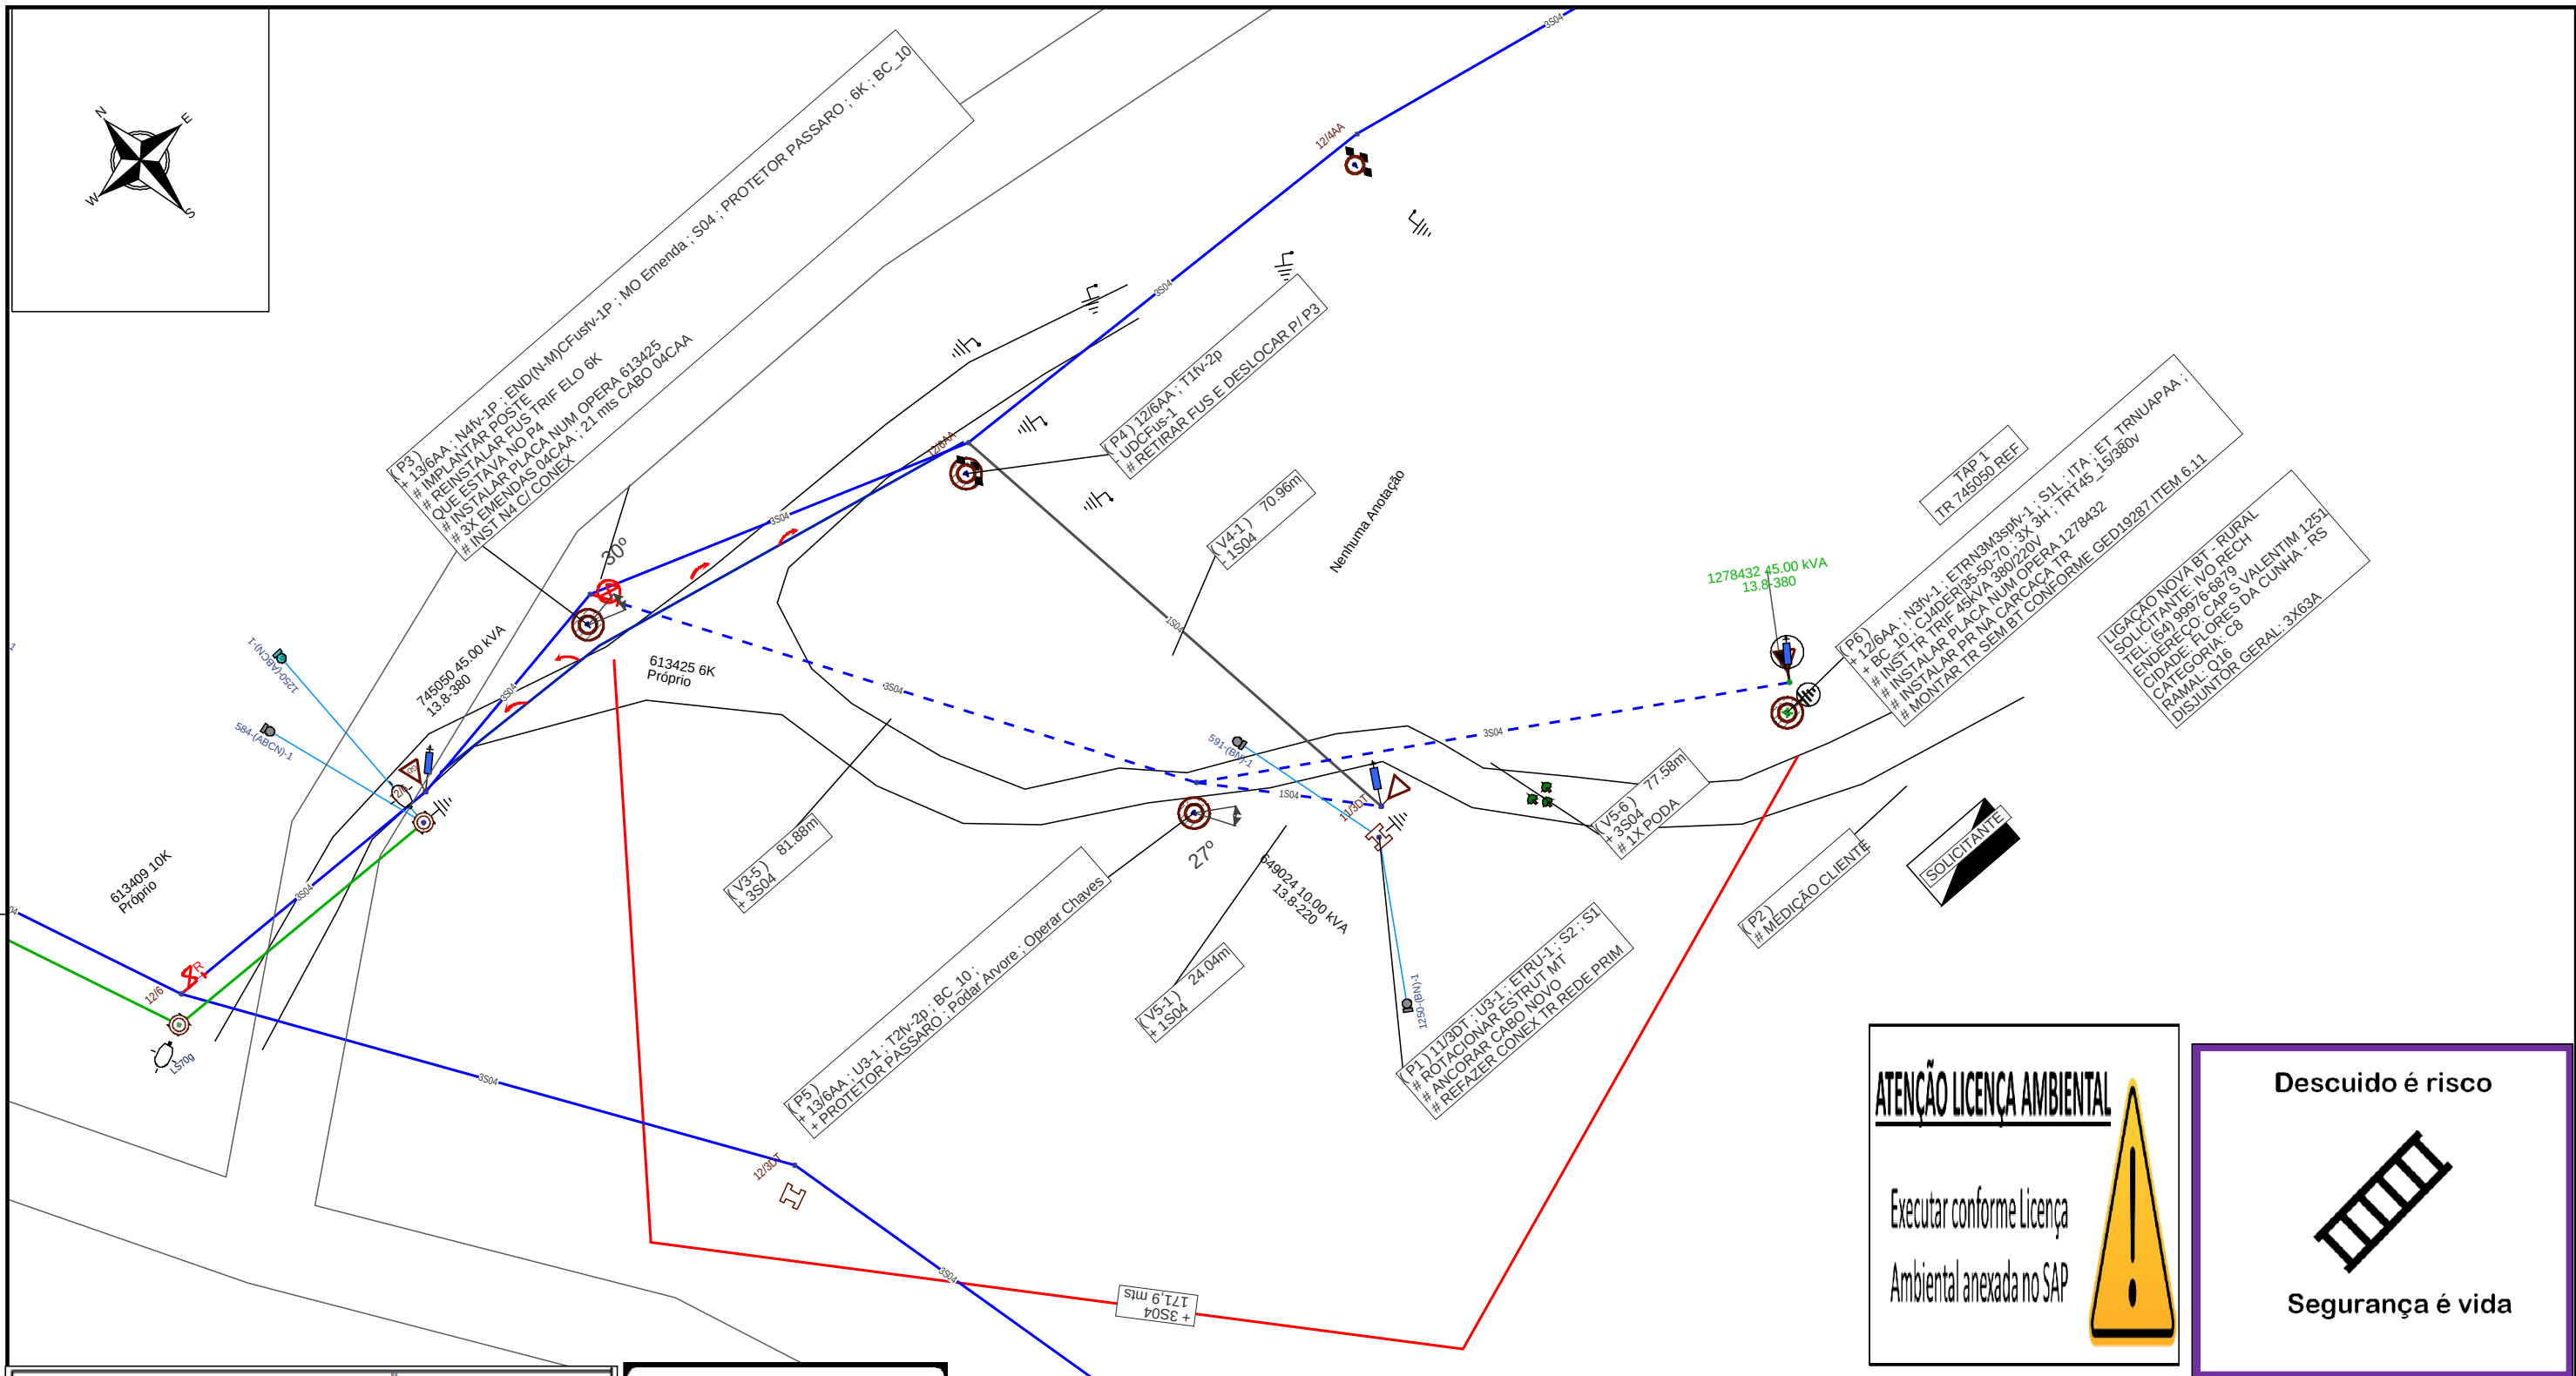

PLANO DE EXECUÇÃO

ESTENDER REDE DE MT TRIF E INST TR TRIF 45kVA 380/220V NO P6.

Executar as atividades conforme planejado, alterações solicitar via D.I.
MO para manobra paga no P5.

Realizar as operações com segurança !

Ação	Equipamento	Número	Clientes	Duração	CHI
Abrir	Chave Fusível	613409	67	6	402
					0
					0
					0
					0
					0
Linha Viva?		Não	CHI TOTAL		402

☐ Poste novo a ser instalado (quando indicado em planta)

FeedBack Para Fábrica de Projetos

Iury de Souza Deckmann

Gerência de Processos de Obras e Manutenção | DROP

Técnico de Análise e Projetos

CFT: 046.153340-52

	Gerência de Obras e Manutenção		
	Município: Flores da Cunha		
Cliente: IVO RECH			
Obra: LIGAÇÃO NOVA BT - RURAL			
Endereço: CAP S VALENTIM 1251 95270-000 FLORES DA CUNHA BR RS			
 Eng. Ederson Paulo Vogel CREA: RS135794 ART: 10911826	Escala: 1:850	Data: 10/07/2025	Nota: 300001064877
	Classe de isolamento: 15kV	AL: FCU12	Folha 1
	Projetista: Iury Deckmann	Projeto: 000007830568	Levantador: Marcio Bedin