
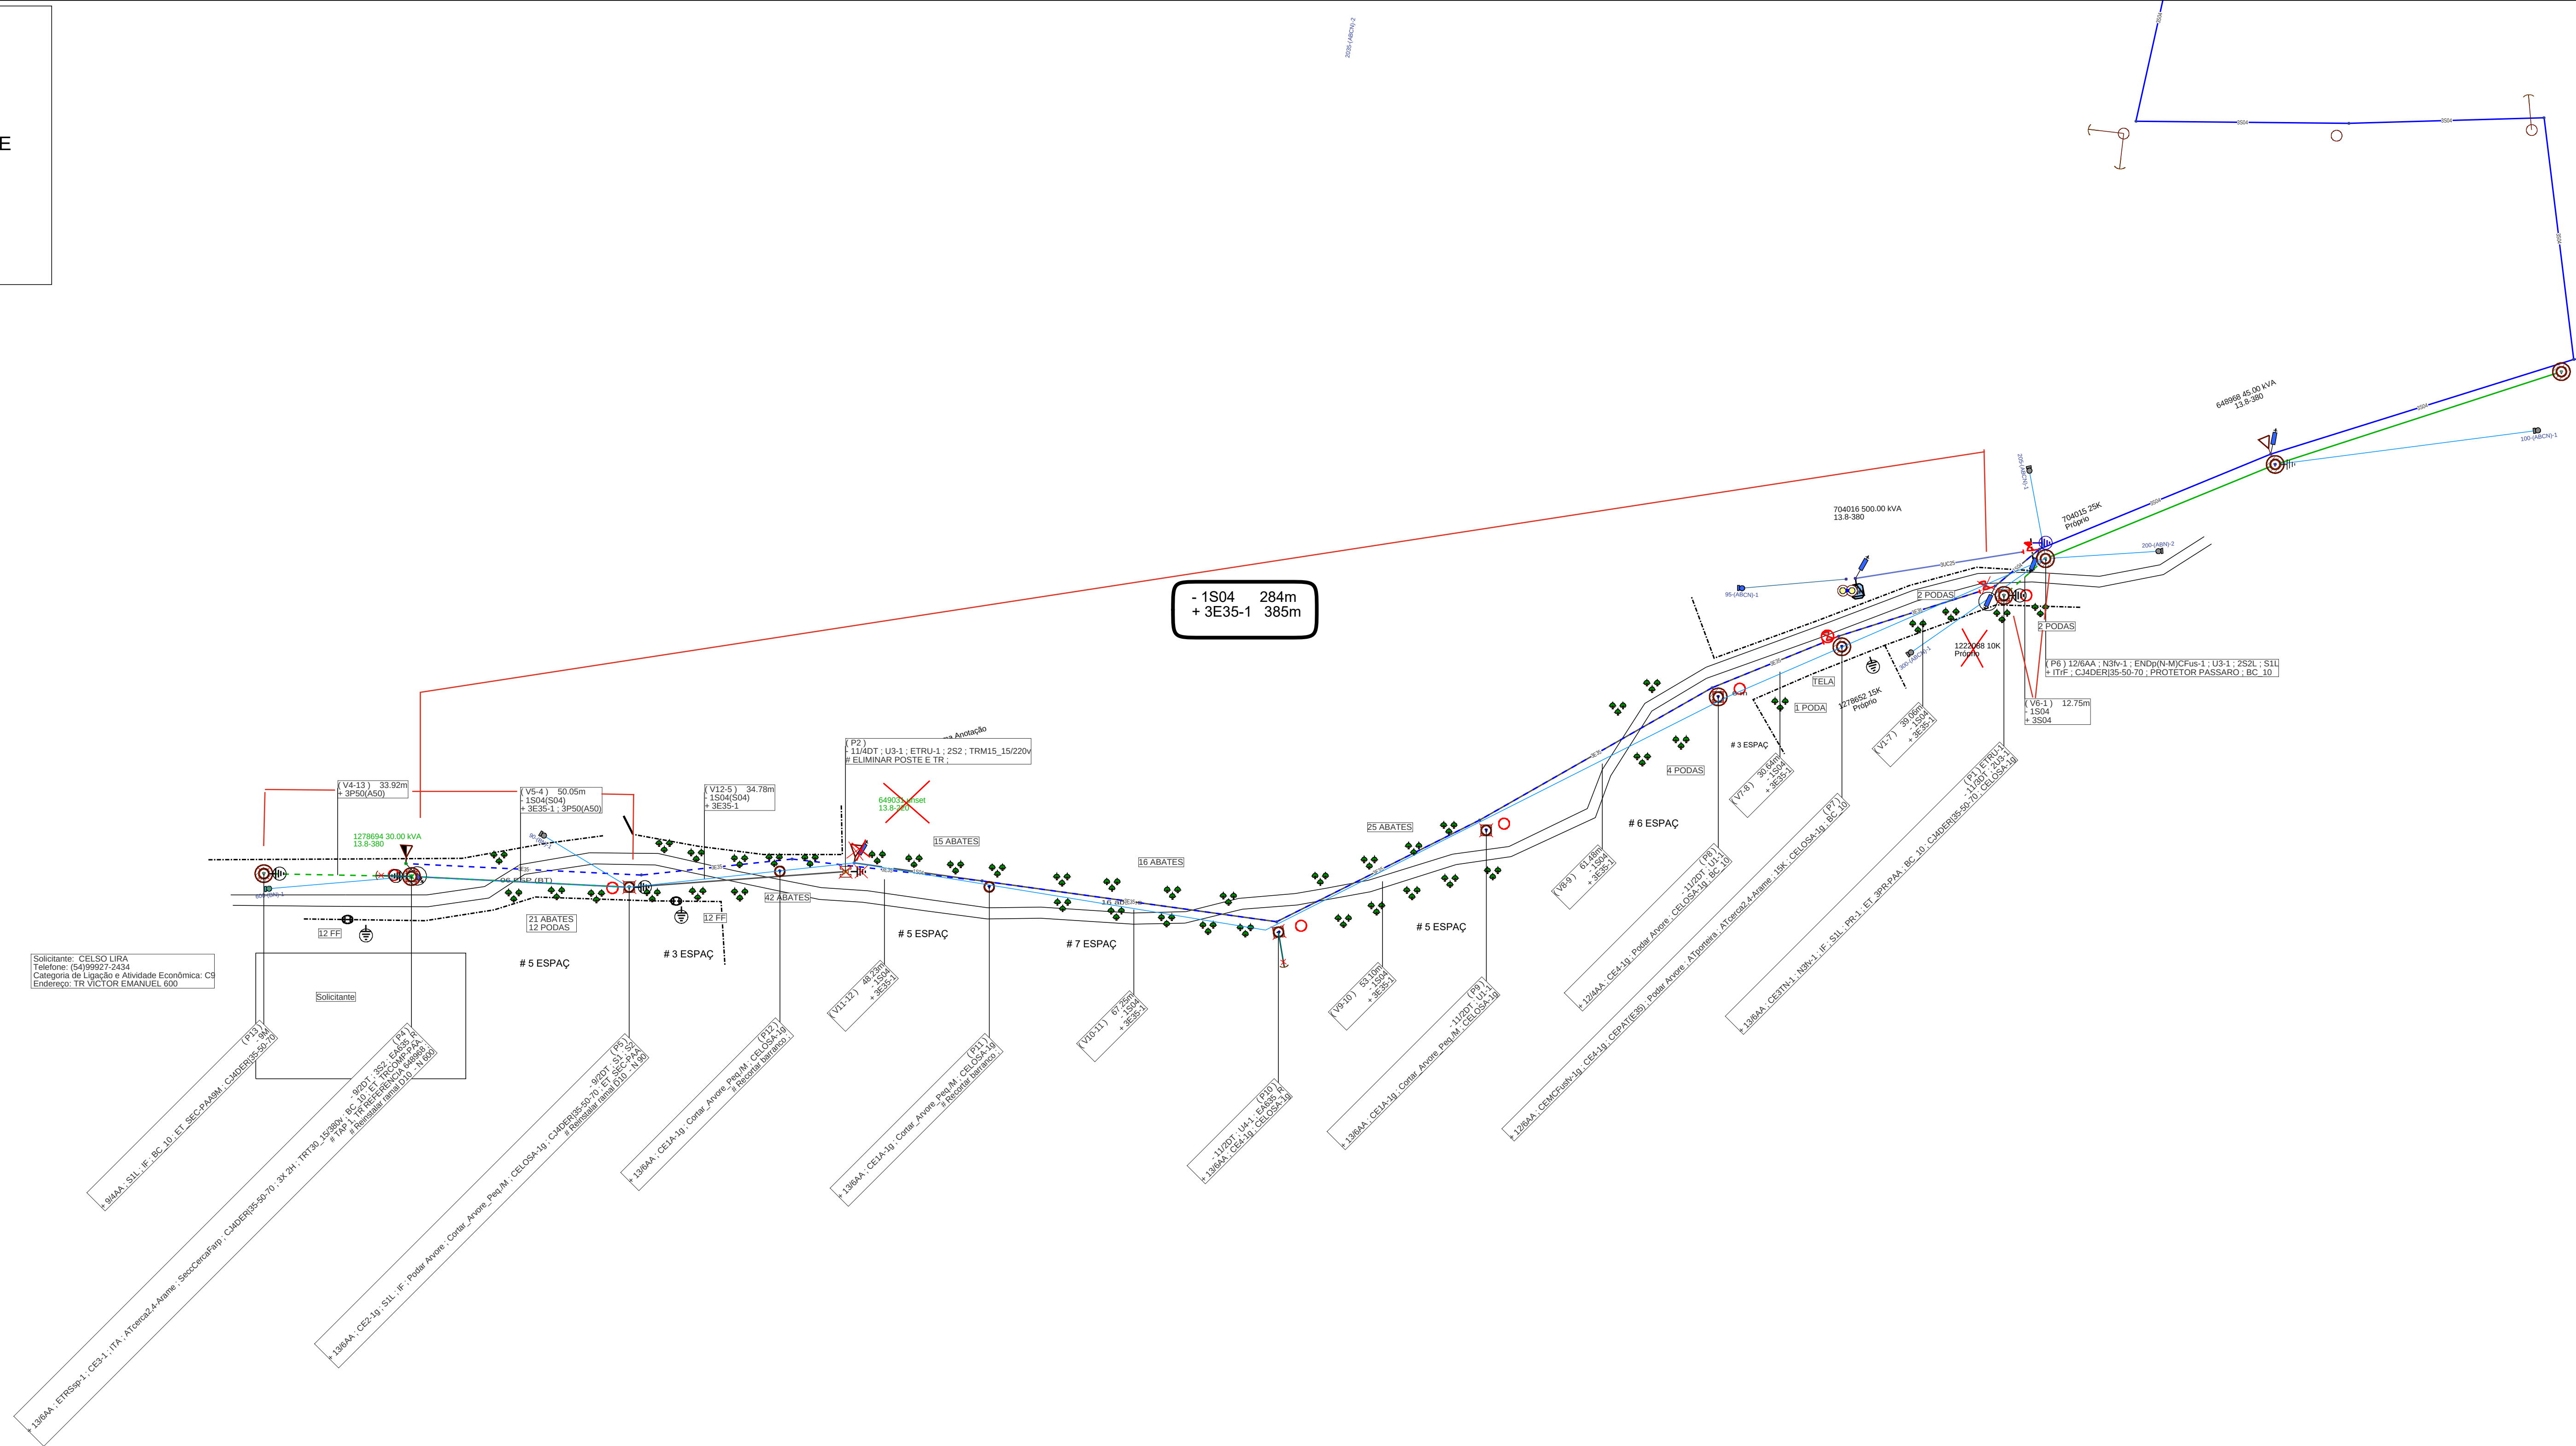


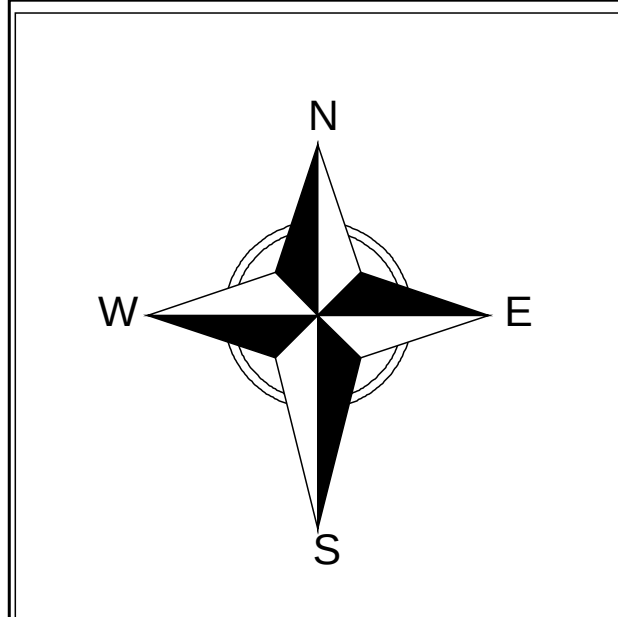

PLANO DE EXECUÇÃO

Trocar os postes P1, P8, P9, P10, P5, P4 e P13
 Instalar os postes P7, P11 e P12
 Retirar rede 1#ACAA entre os postes P6 e P2
 Instalar rede 3#ACAA entre os postes P6 e P1
 Instalar rede Compacta entre os postes P1 e P4
 Retirar rede BT Convencional entre os postes P2 e P4
 Instalar TR no poste P4
 Instalar rede Multiplexada entre os postes P5 e P13

Ação	Equipamento	Número	Clientes	Duração	CHI
Abriu	Chave Faca	613421	13	6	78
					0
					0
					0
					0
					0
Linha Viva?			CHI TOTAL		78


☐ Poste novo a ser instalado (quando indicado em planta)



FeedBack Para Fábrica de Projetos



**Funcionário
inteligente,
previne o
acidente!**

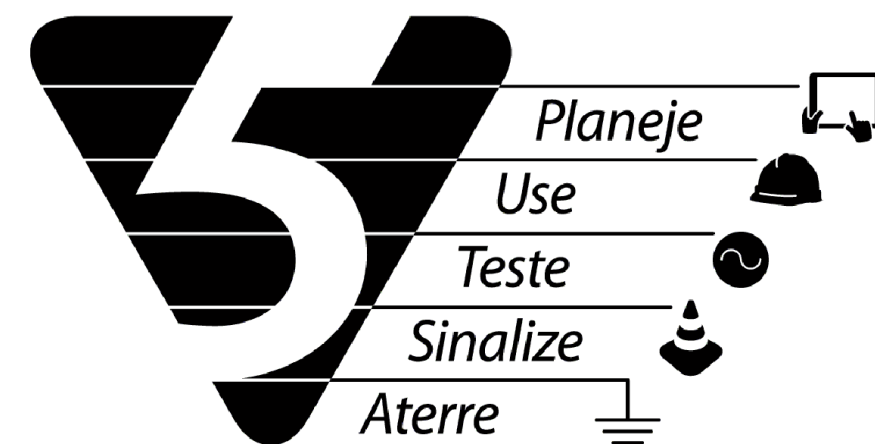

Gerência de Serviços de Rede: SERRA

Município: Caxias do Sul

Cliente: CELSO LIRA

Obra: ALTERAÇÃO DE FASE BT - RURAL

Endereço: TR VICTOR EMANUEL 600 CAXIAS DO SUL RS

Responsável Técnico:	
----------------------	--

Eng. Ederson Paulo Vogel
CREA: RS135794 ART: 10911826

Escala: 1:800

Classe de isolamento	
----------------------	--

Projeto: 000007829351	Projeto: 000007829351
-----------------------	-----------------------

Nota: 300001065048

Folha 1

Levantador:
ALESSANDRO SEVERI

Lucas A B da Rocha

Lucas Antonio Barbosa da Rocha

Gerência de Processos de Obras e Manutenção | DROP

Técnico de Análise e Projetos

CFT: 0226951200-6