

ALTERAÇÃO DE FASE BT - RURAL

12/6AA; N3v-1; ETRN3M3spv-1; ITA; S1L; BC_10; ET_ TRNUAPAA; 3X 2H; C34DER(35-50-70; TRT30_15(380V;
INSTALAR Nº OPERATIVO 1280894
TAP 1 REF 648936
MONTAR TR SEM BT CONFORME GED 19287 - ESTRUTURA DE TRANSFORMADOR SEM REDE SECUNDÁRIA

1280694 30.00 kVA
13.8-380

(V7-8) 71.86r
+ 3504

(P7)
+ 13/6AA; N3N3fv-1P; PROTETOR PASSARO; Podar Arvore; BC_10
PREVISTO 2 PODAS

(V6-7) 59.27m
+ 3504

+ 13/6AA ; T1n-2p ; PROTETOR PASSARO ; ATcerca2,4-Arame
PREVISTO 1 ATERRAMENTO DE CERCA PARALELO 6FF

(V5-6) 65.14m
+ 3S04

(P5)
+ 13/6AA; T2tv-2p; PROTETOR PASSARO; Cortar_Arvore_Grande; BC_10
PREVISTO 1 ABATE

(V4-5) 74.16m
+ 3S04

(P4)
+ 12/4AA ; T1fv-2p ; PROTETOR PASSARO ; Podar Arvore
W PREVISTO 1 PODA

(V3-4) 34.14m

(P11)
11/2DT ; N1-1 ; 2S2


{ P3 }
+ 136AA ; N3D(N-M)fv-1P ; N4fv-1P ; 4S1L ; PROTETOR PASSARO ; ATporteira ; ATcerca2,4-Arame ; Operar Chaves ; BC_1
DERIVAR REDE DE MT ATE P8
PREVISTO ATERRAMENTO DE CERCA 6FF PARA PORTEIRA

738722 45.00 KVA
12 8-380


INSTALAR 6 POSTES NOVOS
ESTENDER 304m DE REDE DE MT 3S04 DE P3 A P8
INSTALAR TR DE 30kVA NO P8

Executar as atividades com segurança respeitando normas e orientações, Não alterar o projeto sem solicitar ao projetista.

Ação	Equipamento	Número	Clientes	Duração	CHI
Abriu	Chave Faca	1102396	51	5	255
					0
					0
					0
					0
					0
Linha Viva?		Não	CHI TOTAL		255

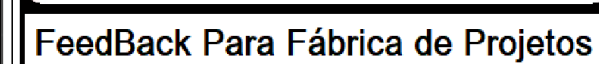

CFT: 04326448067

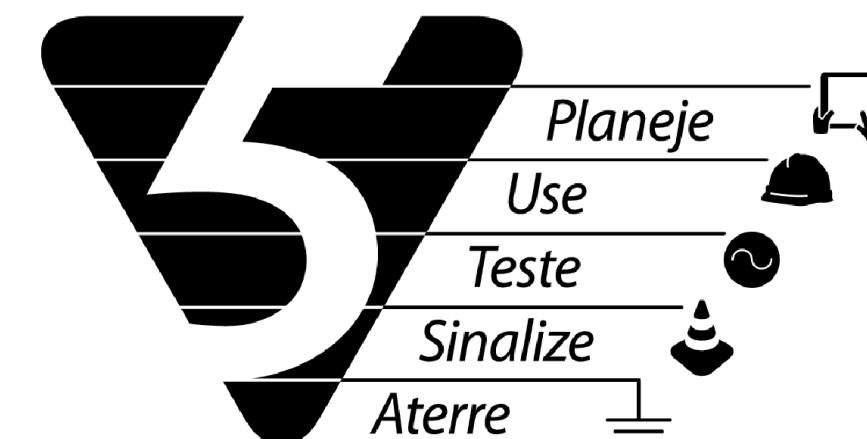

Endereço: CAP S CAETANO 111 95270-000 FLORES DA CUNHA BR RS

Responsável Técnico:  Eng. Ederson Paulo Vogel CREA: RS135794 ART: 10911826	Escala: 1:850	Data: 23/07/2025	Nota: 300001068407
	Classe de Isolação: 15kV	AL: FCU12	Folha 1
	Projetista: JEREMIAS DUARTE	Projeto: 000007836448	Levantador: Alessandro

DESCUIDO É RISCO,



SEGURANÇA É VIDA.