


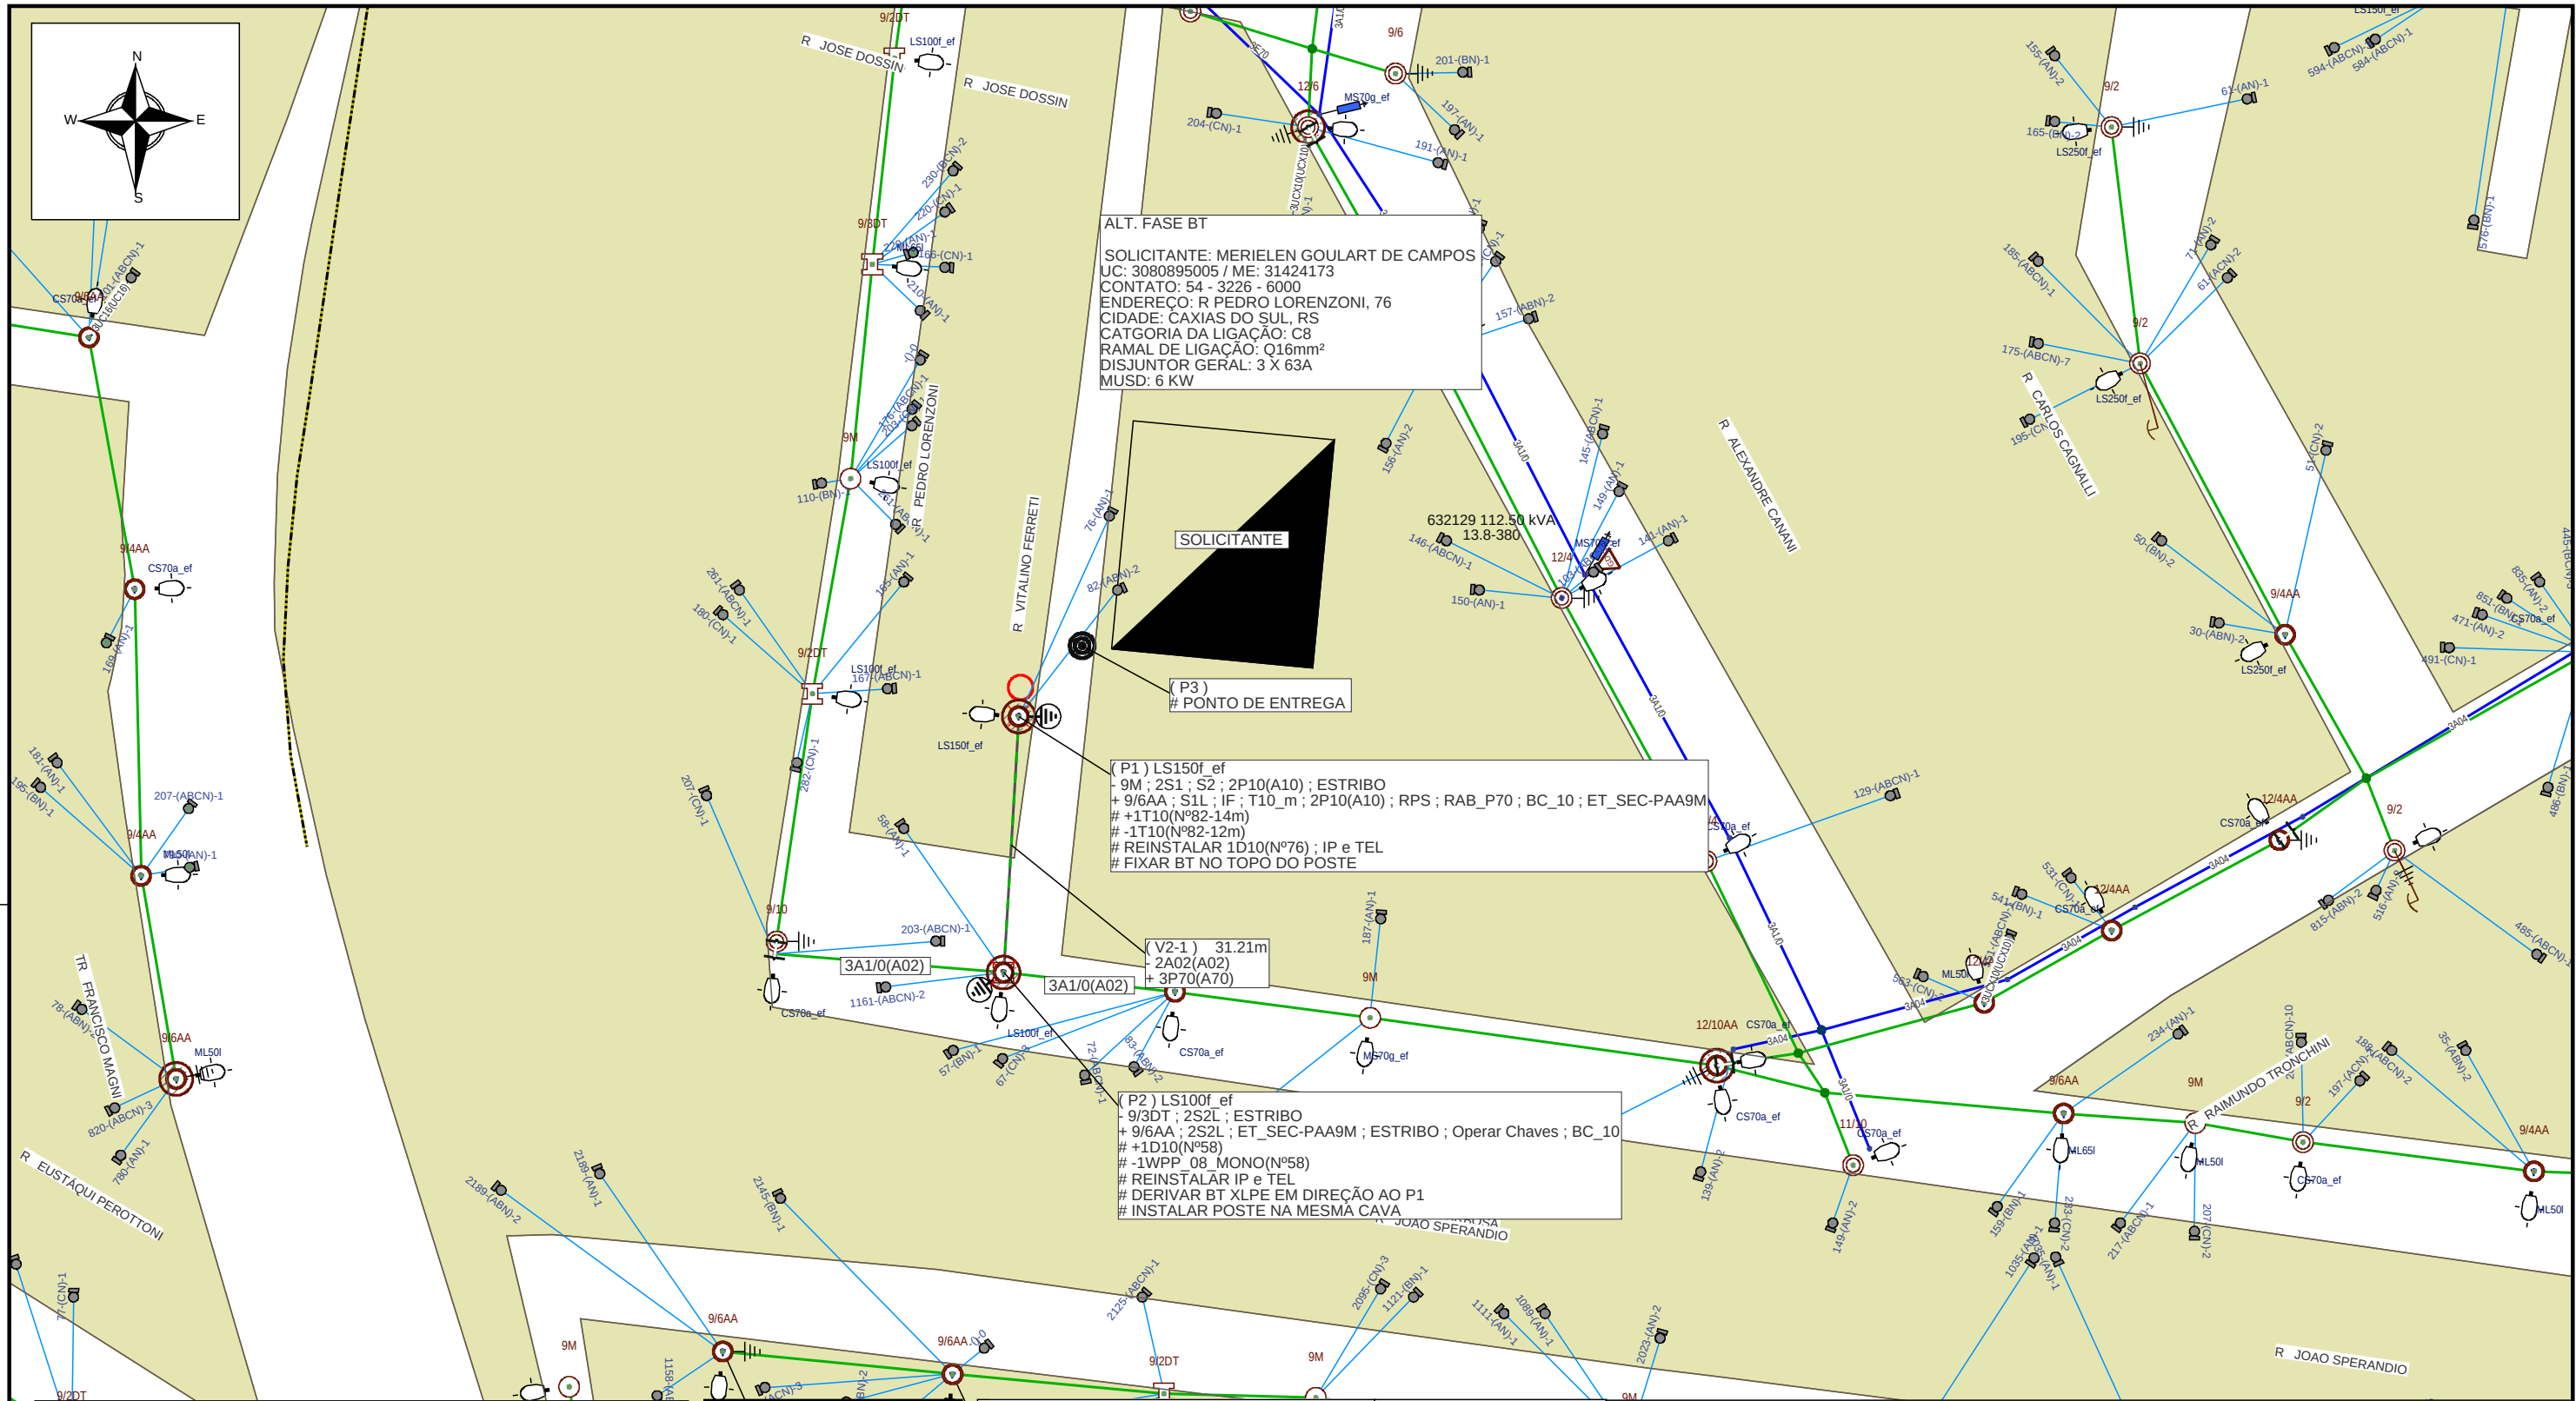

PLANO DE EXECUÇÃO					
Executar atividades com segurança, respeitando normas e orientações					
Abrir cavas e preparar as obras; MO da manobra paga no P2					
Recondutorar rede BT entre P2 e P1					
Recolher resíduos após o término das obras					
Qualquer alteração, solicitar via Desing I					
Ação	Equipamento	Número	Cientes	Duração	CHI
Abrir	Transformador	632129	65	4	260
					0
					0
					0
					0
					0
Linha Viva?					260

FeedBack Para Fábrica de Projetos

SEGURANÇA SE OBTÉM...

...COM COLABORAÇÃO

Planeje
Use
Teste
Sinalize
Aterre

DIEGO SOUZA RIBEIRO

Gerência de Processos de Obras e Manutenção | DROP

Técnico de Análise e Projetos

CFT: 021.824.880-65

Gerência de Obras e Manutenção

Município: CAXIAS DO SUL

Cliente: MERIELEN GOULART DE CAMPOS

Obra: ALTERAÇÃO DE FASE BT

Endereço: R PEDRO LORENZONI 76 95099-480 CAXIAS DO SUL BR RS

Responsável Técnico:

Eng. Ederson Paulo Vogel
CREA: RS135794 ART: 10911826

Escala: 1:800

Classe de isolamento:
15kV

Projetista: DIEGO RBEIRO

Data: 18/12/2025

AL: CXA36

Projeto: 000007946940

Nota:
300001068506

Folha 1

Levantador:
REINHOLDO BRULINGER