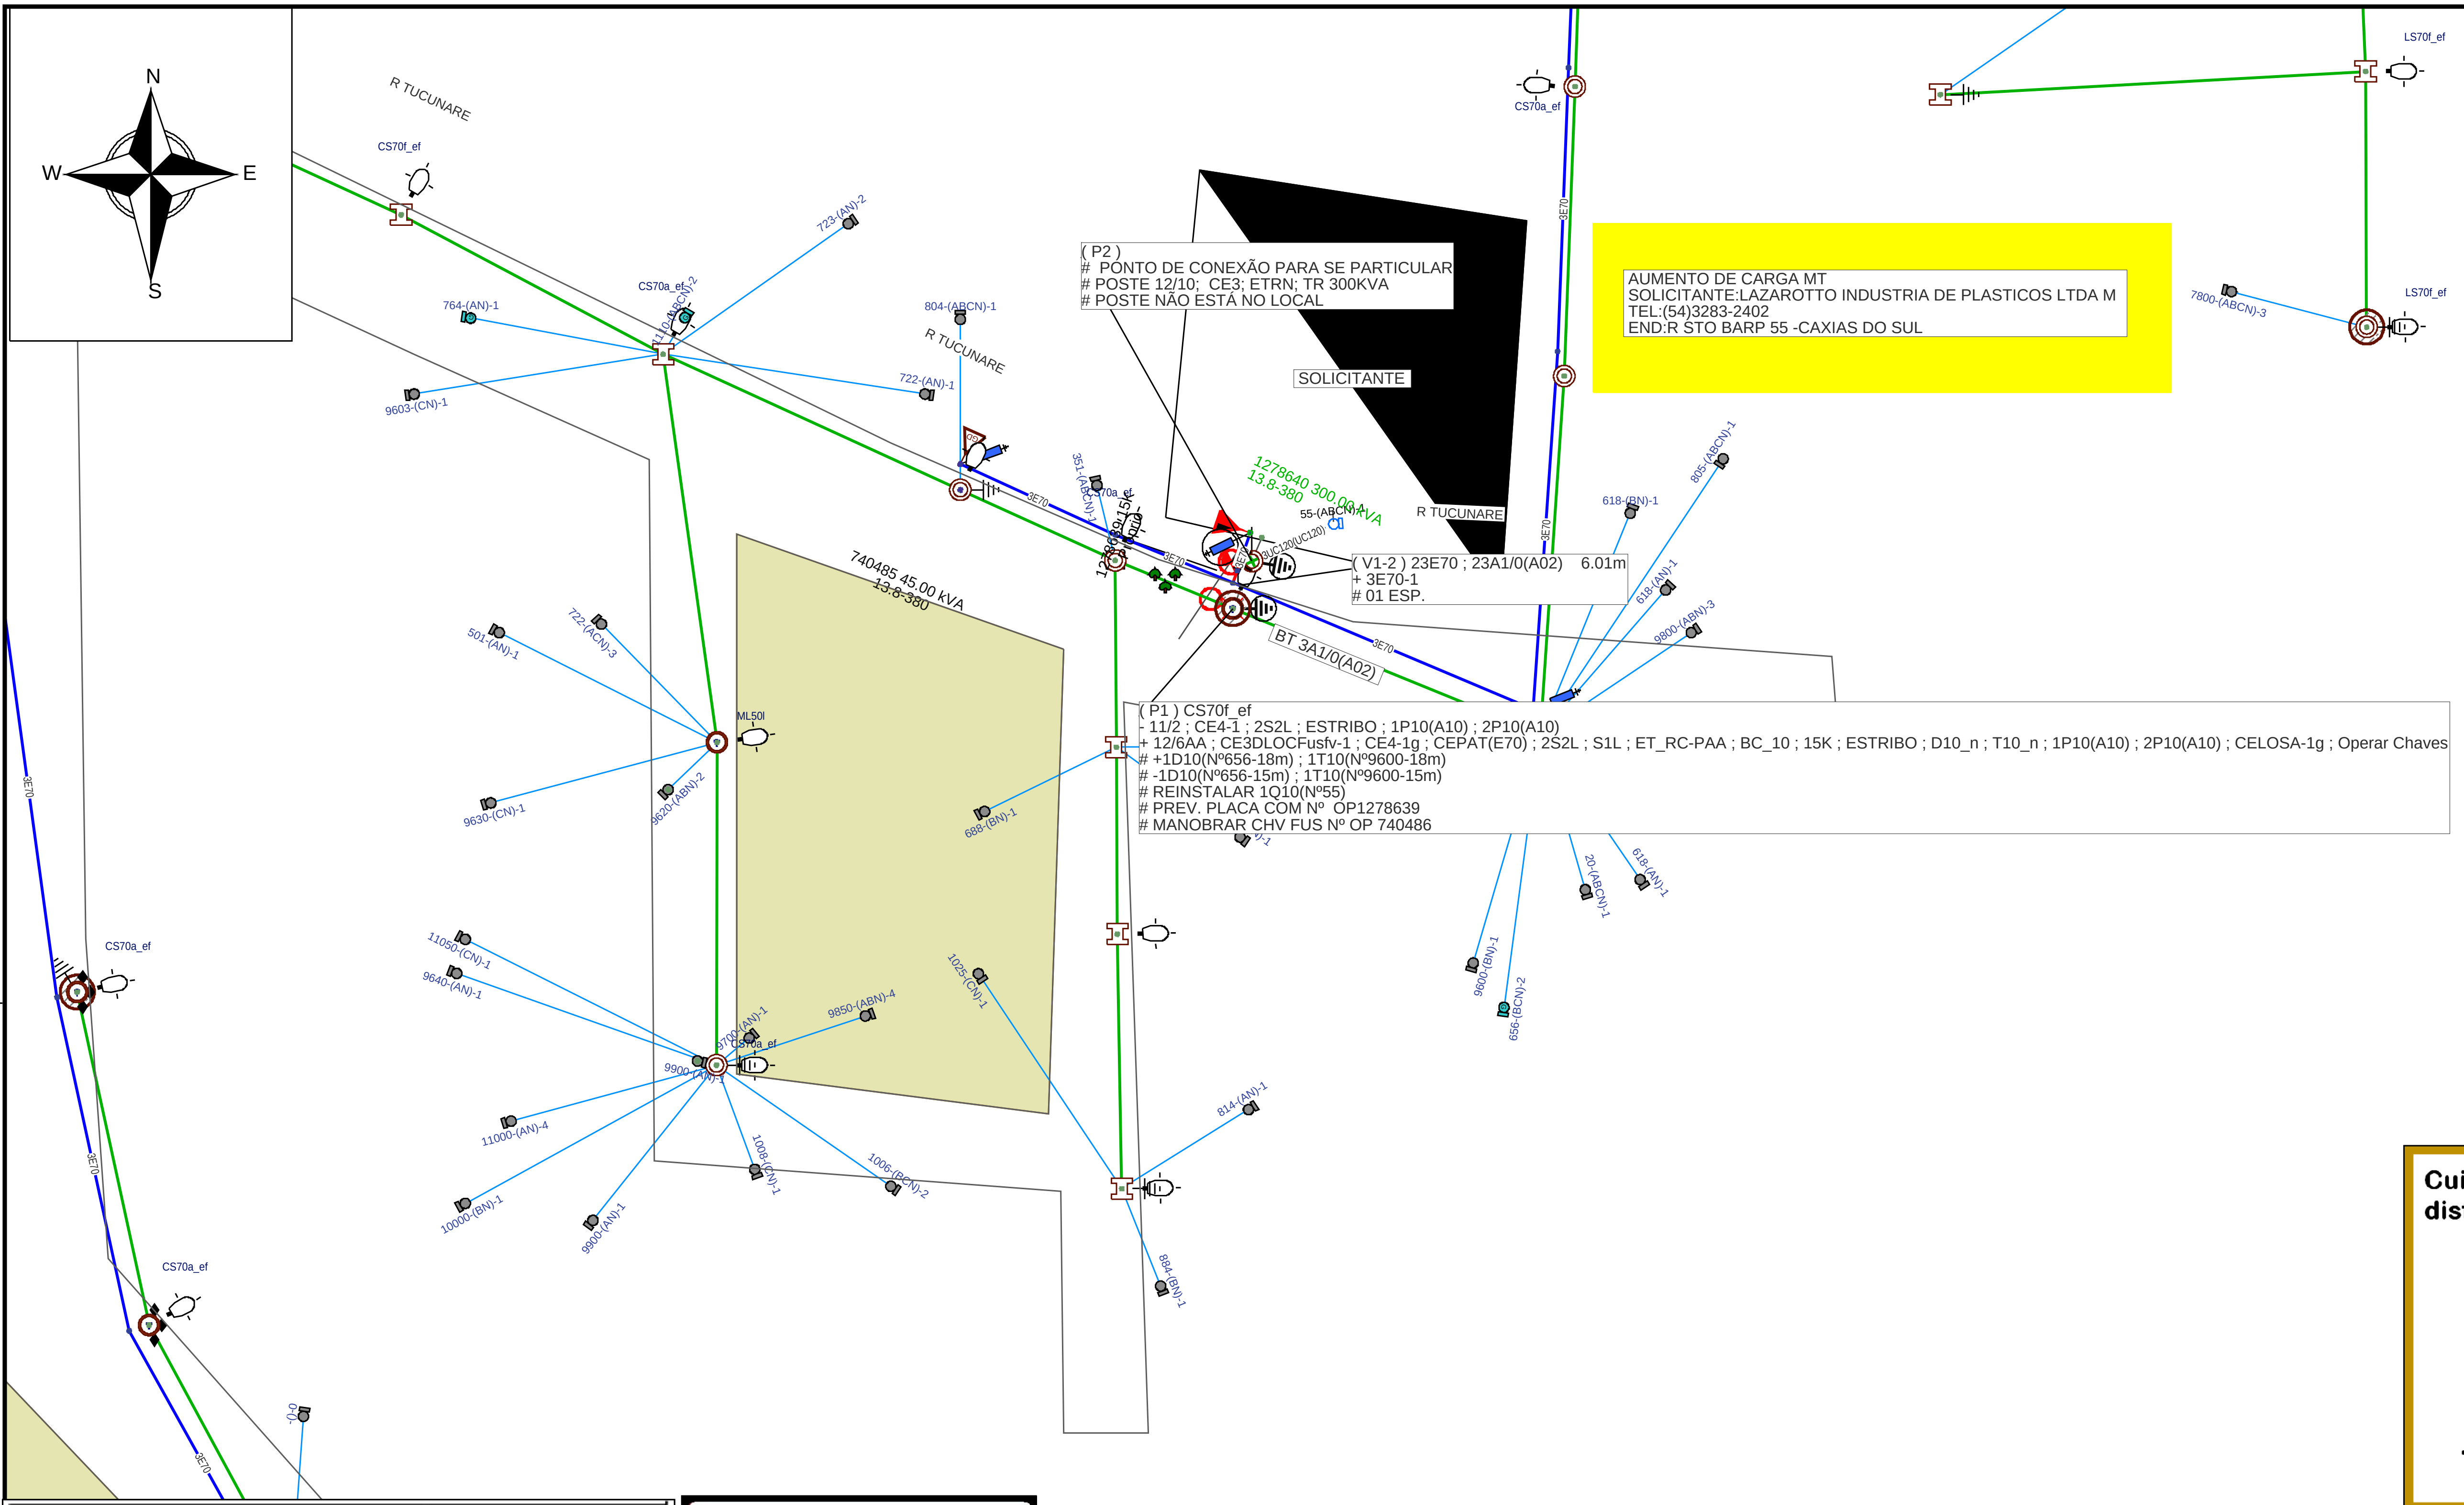
N
W
E
S
R TUCUNARE
CS70f_ef
723-(AN)-2
CS70a_ef
1110-(ABCN)-2
764-(AN)-1
9603-(CN)-1
804-(ABCN)-1
R TUCUNARE
722-(AN)-1
351-(ABCN)-1
CS70a_ef
3E70
1278639 15k
1278640 300.00 kVA
13.8-380
55-(ABCN)-1
3UC120(UC120)
R TUCUNARE
SOLICITANTE
740485 45.00 kVA
13.8-380
BT 3A1/0(A02)
3E70
CS70a_ef
3E70
618-(BN)-1
805-(ABCN)-1
618-(AN)-1
9800-(ABN)-3
501-(AN)-1
722-(ACN)-3
ML50I
9630-(CN)-1
9620-(ABN)-2
688-(BN)-1
20-(ABCN)-1
618-(AN)-1
9600-(BN)-1
656-(BCN)-2
LS70f_ef
LS70f_ef
7800-(ABCN)-3
3E70
CS70a_ef
11050-(CN)-1
9640-(AN)-1
1025-(CN)-1
9850-(ABN)-4
9700-(AN)-1
CS70a_ef
9900-(AN)-1
11000-(AN)-4
10000-(BN)-1
9900-(AN)-1
1008-(CN)-1
1006-(BCN)-2
814-(AN)-1
884-(BN)-1
3E70
CS70a_ef
0-()-0
3E70

(P2)
PONTO DE CONEXÃO PARA SE PARTICULAR
POSTE 12/10; CE3; ETRN; TR 300KVA
POSTE NÃO ESTÁ NO LOCAL

AUMENTO DE CARGA MT
SOLICITANTE:LAZAROTTO INDUSTRIA DE PLASTICOS LTDA M
TEL:(54)3283-2402
END:R STO BARP 55 -CAXIAS DO SUL

(V1-2) 23E70 ; 23A1/0(A02) 6.01m
+ 3E70-1
# 01 ESP.

(P1) CS70f_ef
- 11/2 ; CE4-1 ; 2S2L ; ESTRIBO ; 1P10(A10) ; 2P10(A10)
+ 12/6AA ; CE3DLOCFusfv-1 ; CE4-1g ; CEPAT(E70) ; 2S2L ; S1L ; ET_RC-PAA ; BC_10 ; 15K ; ESTRIBO ; D10_n ; T10_n ; 1P10(A10) ; 2P10(A10) ; CELOSA-1g ; Operar Chaves
# +1D10(Nº656-18m) ; 1T10(Nº9600-18m)
# -1D10(Nº656-15m) ; 1T10(Nº9600-15m)
# REINSTALAR 1Q10(Nº55)
# PREV. PLACA COM Nº OP1278639
# MANOBRAR CHV FUS Nº OP 740486

Cuidado com os perigos disfarçados...

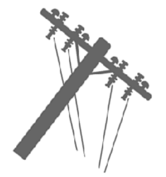

...Uma rede tombada, ainda pode estar energizada!

PLANO DE EXECUÇÃO

Executar a obra seguindo todos os passos de segurança

Substituir os postes conforme projetodo, para execução, manobrar os equipamentos descritos abaixo

Ação	Equipamento	Número	Clientes	Duração	CHI
Abrir	Chave Fusivel	740486	62	4	248
					0
					0
					0
					0
					0
Linha Viva?		Não	CHI TOTAL		248

○ Poste novo a ser instalado (quando indicado em planta)

FeedBack Para Fábrica de Projetos

Planeje
Use
Teste
Sinalize
Aterre

Rodrigo de Vargas Santos

Rodrigo De Vargas Santos
Gerência de Processos de Obras e Manuntenção | DROP
Técnico de Análise e Projetos
CFT: 00235489085

CPFL ENERGIA

Gerência de Obras e Manutenção

Município: Caxias do Sul

Cliente: LAZAROTTO INDUSTRIA DE PLASTICOS LTDA ME

Obra: AUMENTO DE CARGA MT

Endereço: R STO BARP 55 95055-075 CAXIAS DO SUL BR RS

Responsável Técnico:
Eng. Ederson Paulo Vogel
CREA: RS135794 ART: 10911826

Escala: 1:850	Data: 11/07/2025	Nota: 300001076323
Classe de isolação: 15kV	AL: KCS26	Folha 1
Projetista: Rodrigo Santos	Projeto: 000007862618	Levantador: ALESSANDRO SEVERO DE OLIVEIRA