



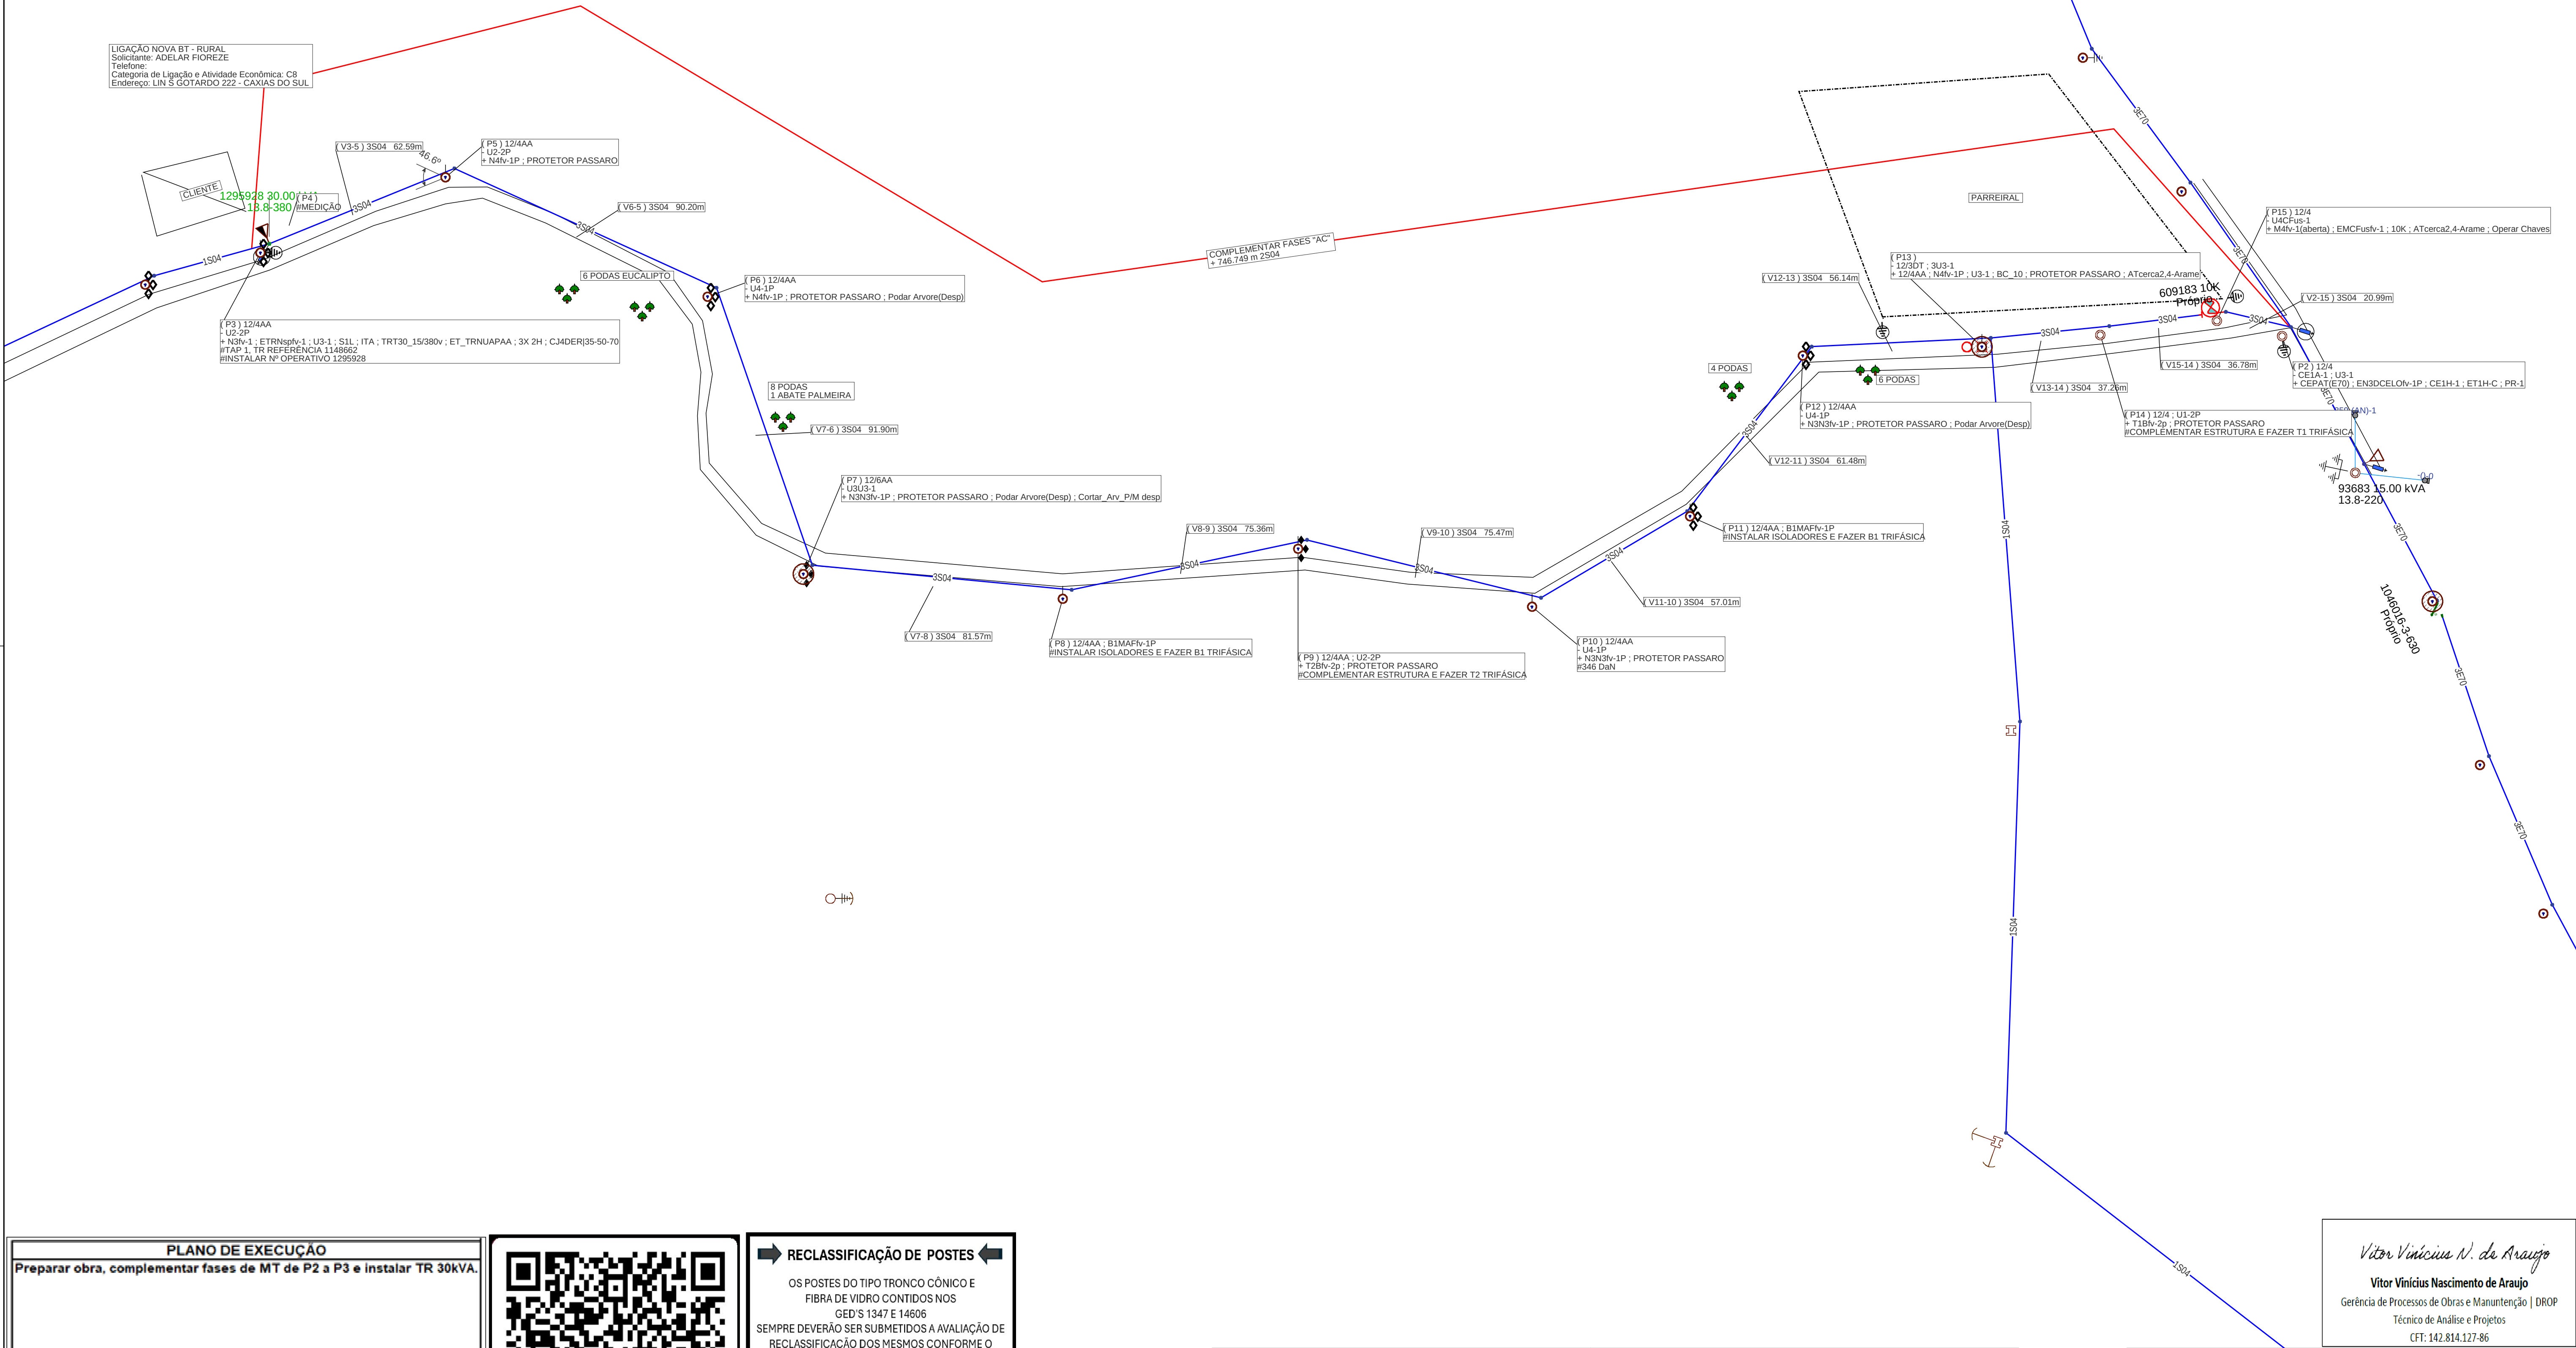

PLANO DE EXECUÇÃO					
Preparar obra, complementar fases de MT de P2 a P3 e instalar TR 30kVA.					
Executar as atividades com segurança e excelência.					
Ação	Equipamento	Número	Clientes	Duração	CHI
Abrir	Chave Fusível	117418	22	5	110
					0
					0
					0
					0
					0
Linha Viva?	Não		CHI TOTAL		110
Poste novo a ser instalado (quando indicado em planta)					

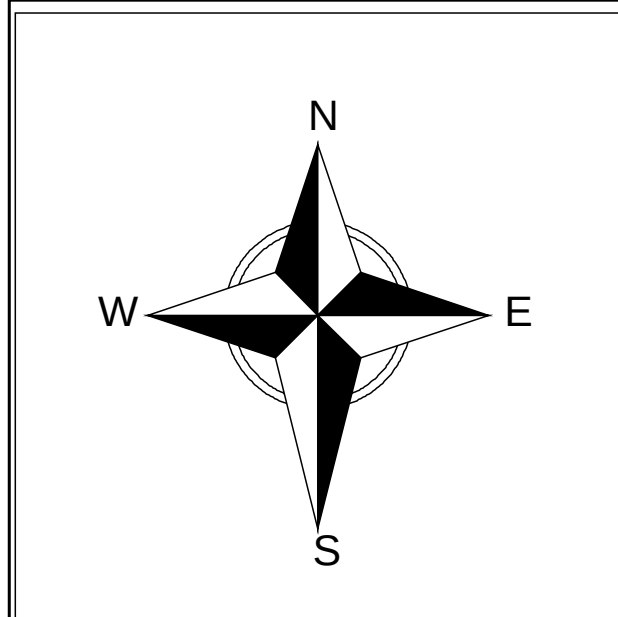

FeedBack Para Fábrica de Projetos

RECLASSIFICAÇÃO DE POSTES

OS POSTES DO TIPO TRONCO CÔNICO E FIBRA DE VIDRO CONTIDOS NOS GED'S 1347 E 14606 SEMPRE DEVERÃO SER SUBMETIDOS A AVALIAÇÃO DE RECLASSIFICAÇÃO DOS MESMOS CONFORME O GED 18968

DEVERÃO SEMPRE SER AVALIADOS 3 PARÂMETROS:
CARACTERÍSTICAS TÉCNICAS;
FISSURAS;
APARÊNCIAS.

O DETALHAMENTO DE CADA PARÂMETRO DEVE SER VERIFICADO JUNTO AO GED 18968.

Seja a mudança que você quer ver na segurança do trabalho.

Planeje

Use

Teste

Sinalize

Aterre

Gerência de Serviços de Rede: SERRA

Município: Caxias do Sul

Cliente: ADELAR FIOREZE

Obra: LIGAÇÃO NOVA BT - RURAL

Endereço: LIN S GOTARDO 222 95140-000 CAXIAS DO SUL BR RS

Responsável Técnico:
Eng. Ederson Paulo Vogel
CREA: RS195794

Escala: 1:1000
Classe de Isolção: 15kV
Projetista: Vitor Vinicius

Data: 24/11/2025
AL: CXD13
Projeto: 000007930234

Nota: 300001077623
Folha 1
Levantador: Reinhold Brulinger