


REUTILIZAR CABOS
NO DESLOCAMENTO
REINST. ESP.

REMOÇÃO DE REDE POSTE AFASTAMENTO
EQUIPAMENTO REFERENCIA:TR 698382
SOLICITANTE:ELIGIO ANTONIO BOFF
TEL:(54)99105-9990
END:TVS LEOPOLDINA, 966 - CAXIAS DO SUL

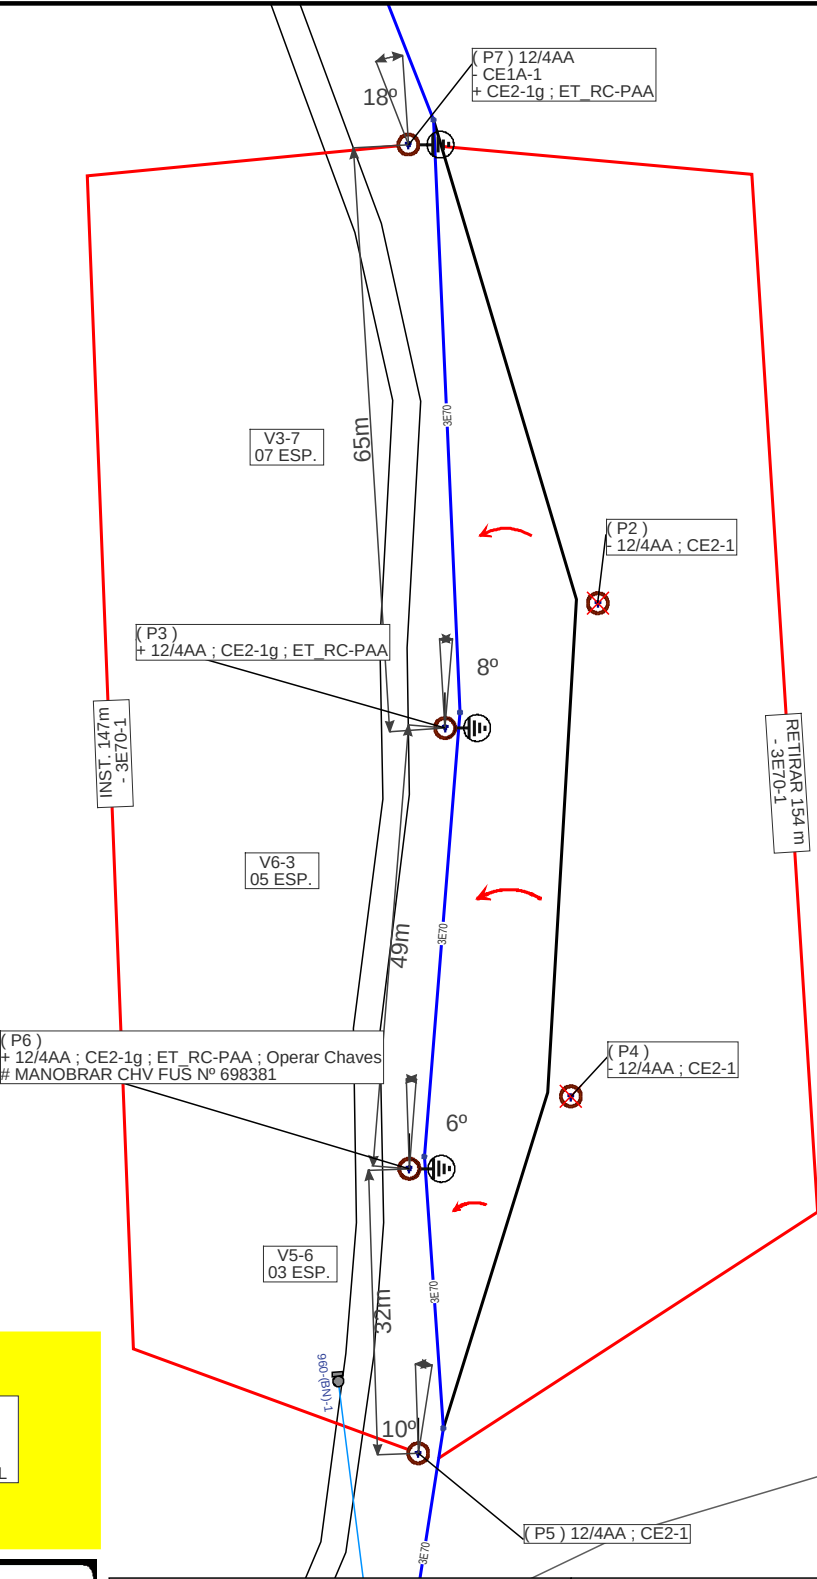

Cuidado com os perigos
disfarçados...



...Uma rede tombada, ainda
pode estar energizada!

PLANO DE EXECUÇÃO

Executar a obra seguindo todos os passos de segurança


Substituir os postes conforme projetado, para execução, manobrar os equipamentos descritos abaixo

Ação	Equipamento	Número	Clientes	Duração	CHI
Abrir	Chave Fusível	698381	4	5	20
					0
					0
					0
					0
					0
Linha Viva?		Não	CHI TOTAL		20

Poste novo a ser instalado (quando indicado em planta)



FeedBack Para Fábrica de Projetos

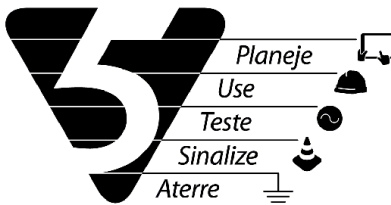

Rodrigo De Vargas Santos
Gerência de Processos de Obras e Manutenção | DROP
Técnico de Análise e Projetos
CFT: 00235489085



Gerência de Obras e Manutenção

Município: Caxias do Sul

Cliente: ELIGIO ANTONIO BOFF

Obra: REMOÇÃO DE REDE POSTE AFASTAMENTO

Endereço: TVS LEOPOLDINA 966 95100-000 CAXIAS DO SUL BR RS

Responsável Técnico:

Eng. Ederson Paulo Vogel
CREA: RS135794 ART: 10911826

Escala: 1:850

Classe de isolamento:

15kV
Projetista: Rodrigo Santos

Data: 04/09/2025

AL: CXD22

Projeto: 000007871678

Nota:
300001078282

Folha 1

Levantador: ALESSANDRO SEVERO DE OLIVEIRA