


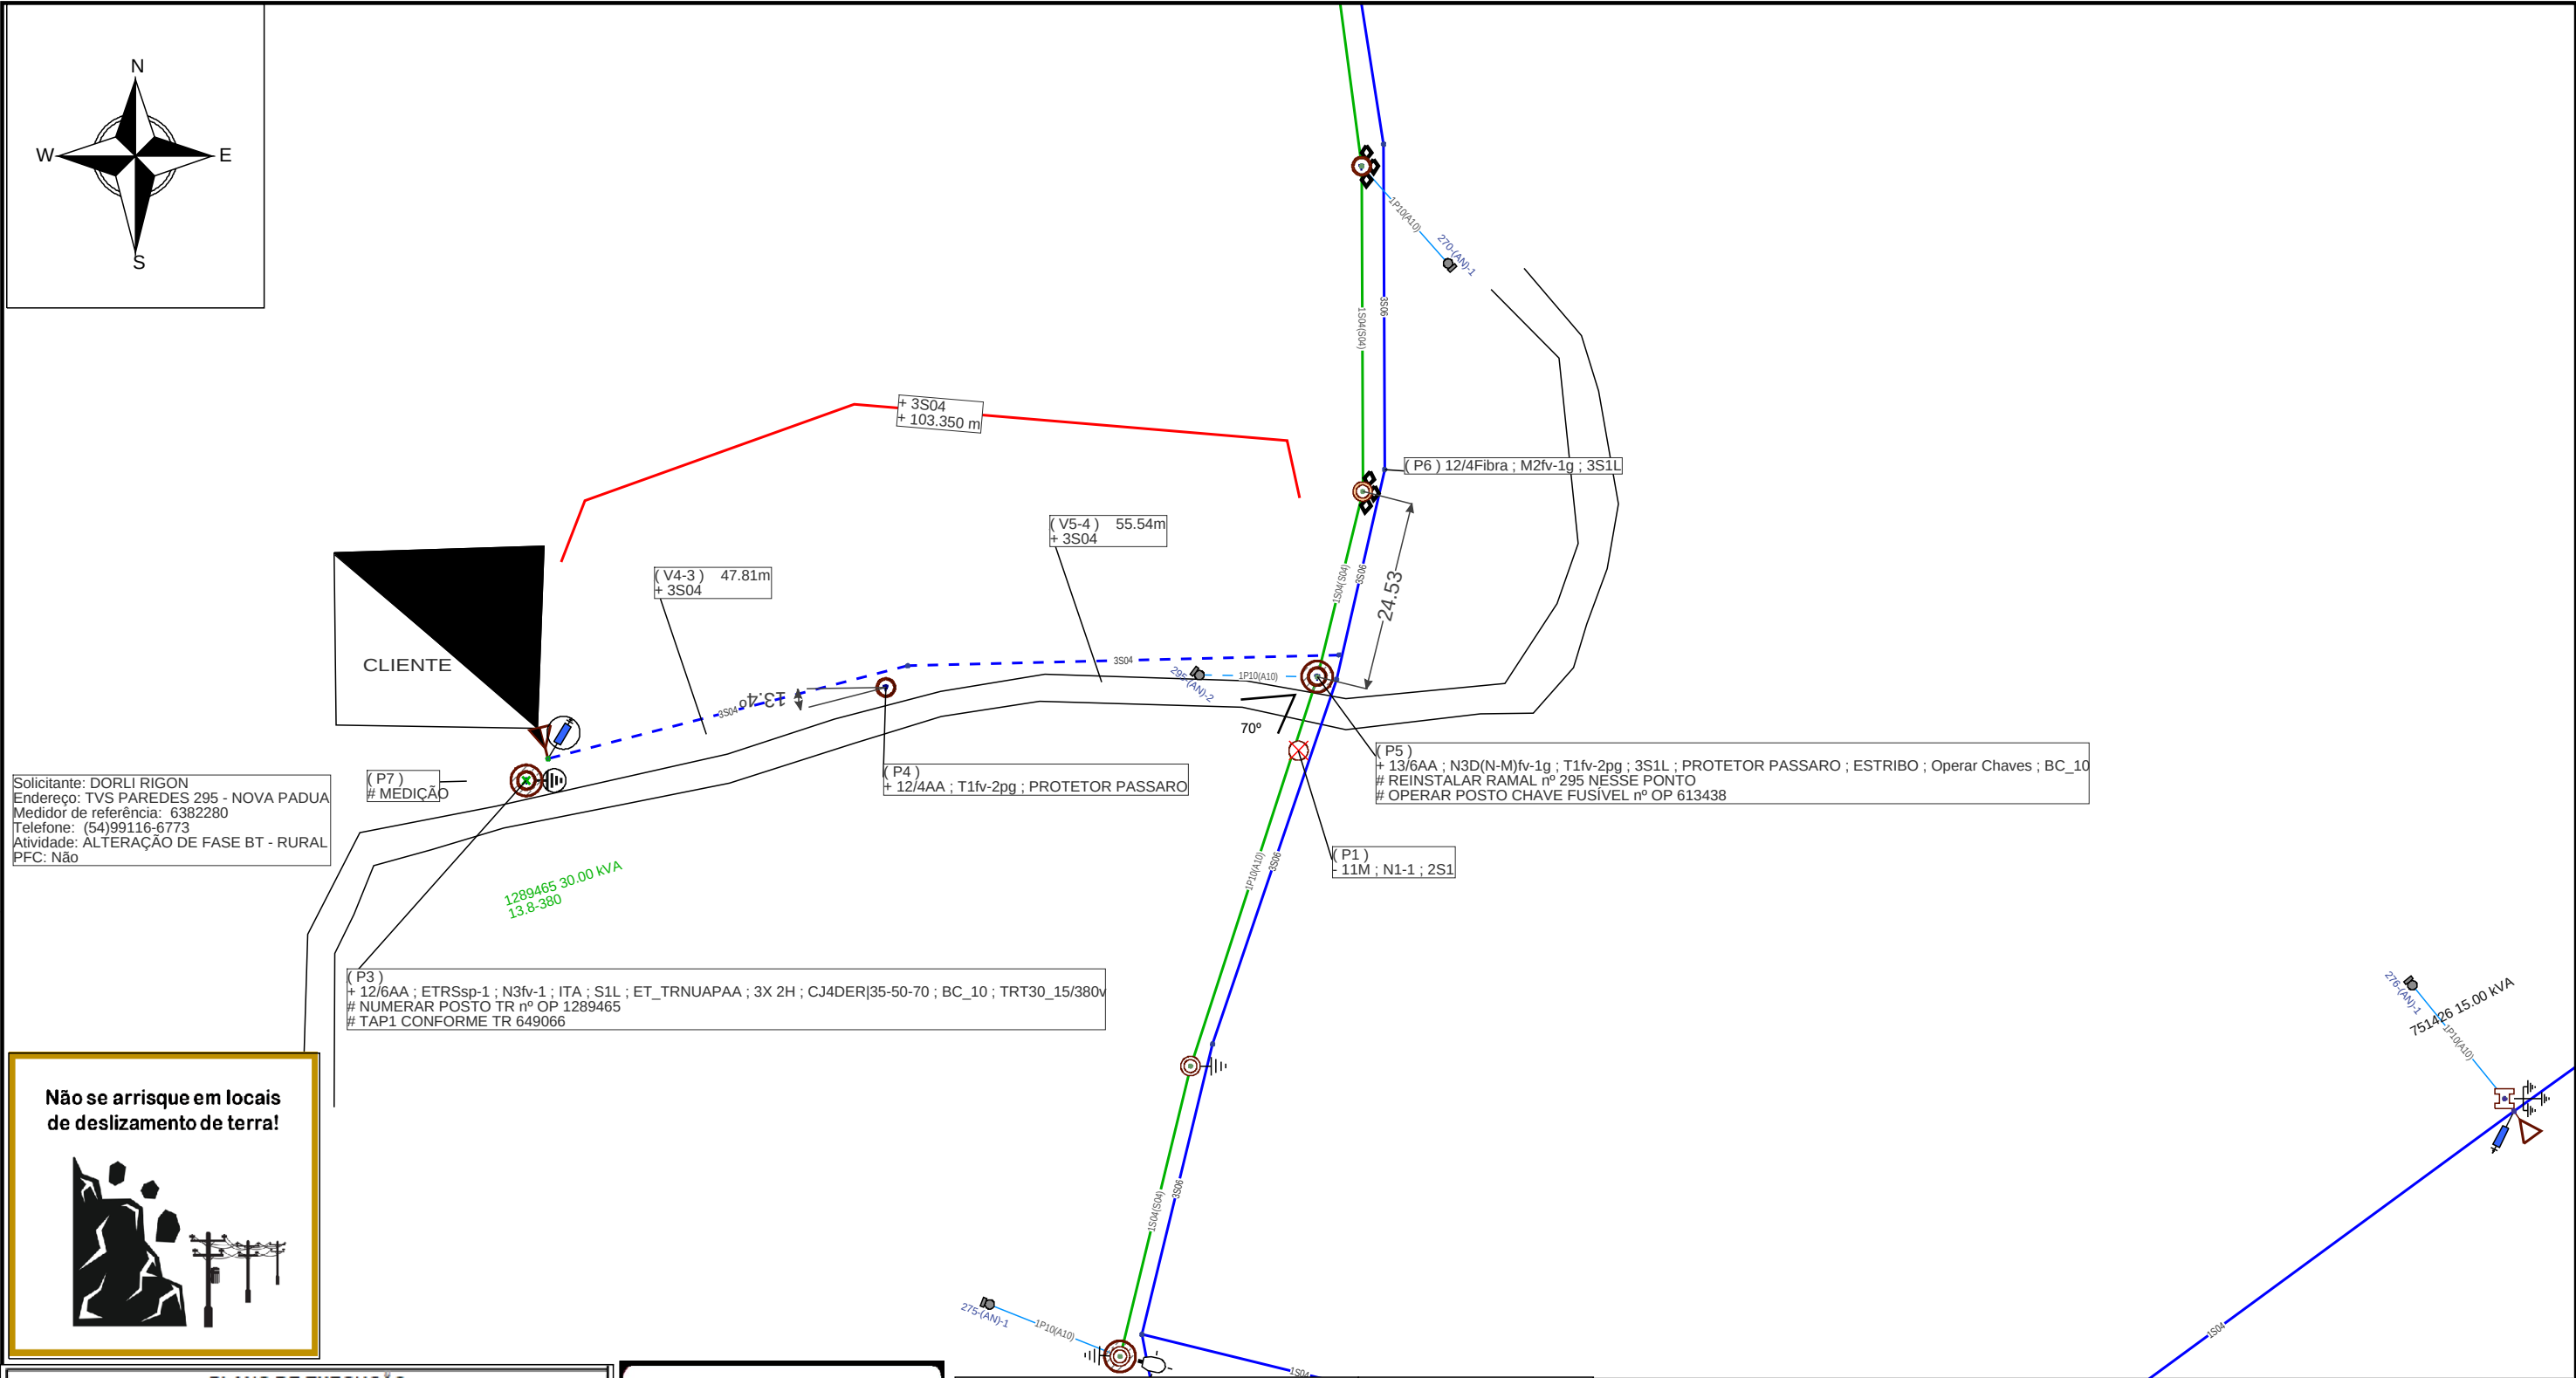

Não se arrisque em locais de deslizamento de terra!

PLANO DE EXECUÇÃO					
Executar a obra seguindo todos os passos de segurança!					
Abrir o equipamento indicado ABAIXO e executar a obra em LM					
Executar atividades de acordo com o projeto.					
Ação	Equipamento	Número	Clientes	Duração	CHI
Abrir	Chave Fusível	613438	99	4	396
Linha Viva?		Não	CHI TOTAL		396
☐ Poste novo a ser instalado (quando indicado em planta)					

FeedBack Para Fábrica de Projetos

Gerência de Obras e Manutenção

Município: Nova Pádua

Planeje
Use
Teste
Sinalize
Aterre

Felipe Gaspari Souza
Felipe Gaspari Souza
Gerência de Processos de Obras e Manutenção | DROP
Técnico de Análise e Projetos
CFT: 028.654.060-67

Cliente: DORLI RIGON

Obra: ALTERAÇÃO DE FASE BT - RURAL

Endereço: TVS PAREDES 295 95275-000 NOVA PADUA BR RS

Responsável Técnico: Eng. Ederson Paulo Vogel CREA: RS135794 ART: 10911826	Escala: 1:850	Data: 22/09/2025	Nota: 300001078424
	Classe de isolamento: 15kV	AL: FCU14	Folha 1
	Projetista: FELIPE GASPARI	Projeto: 000007886222	Levantador REINHOLDO BRULINGER