
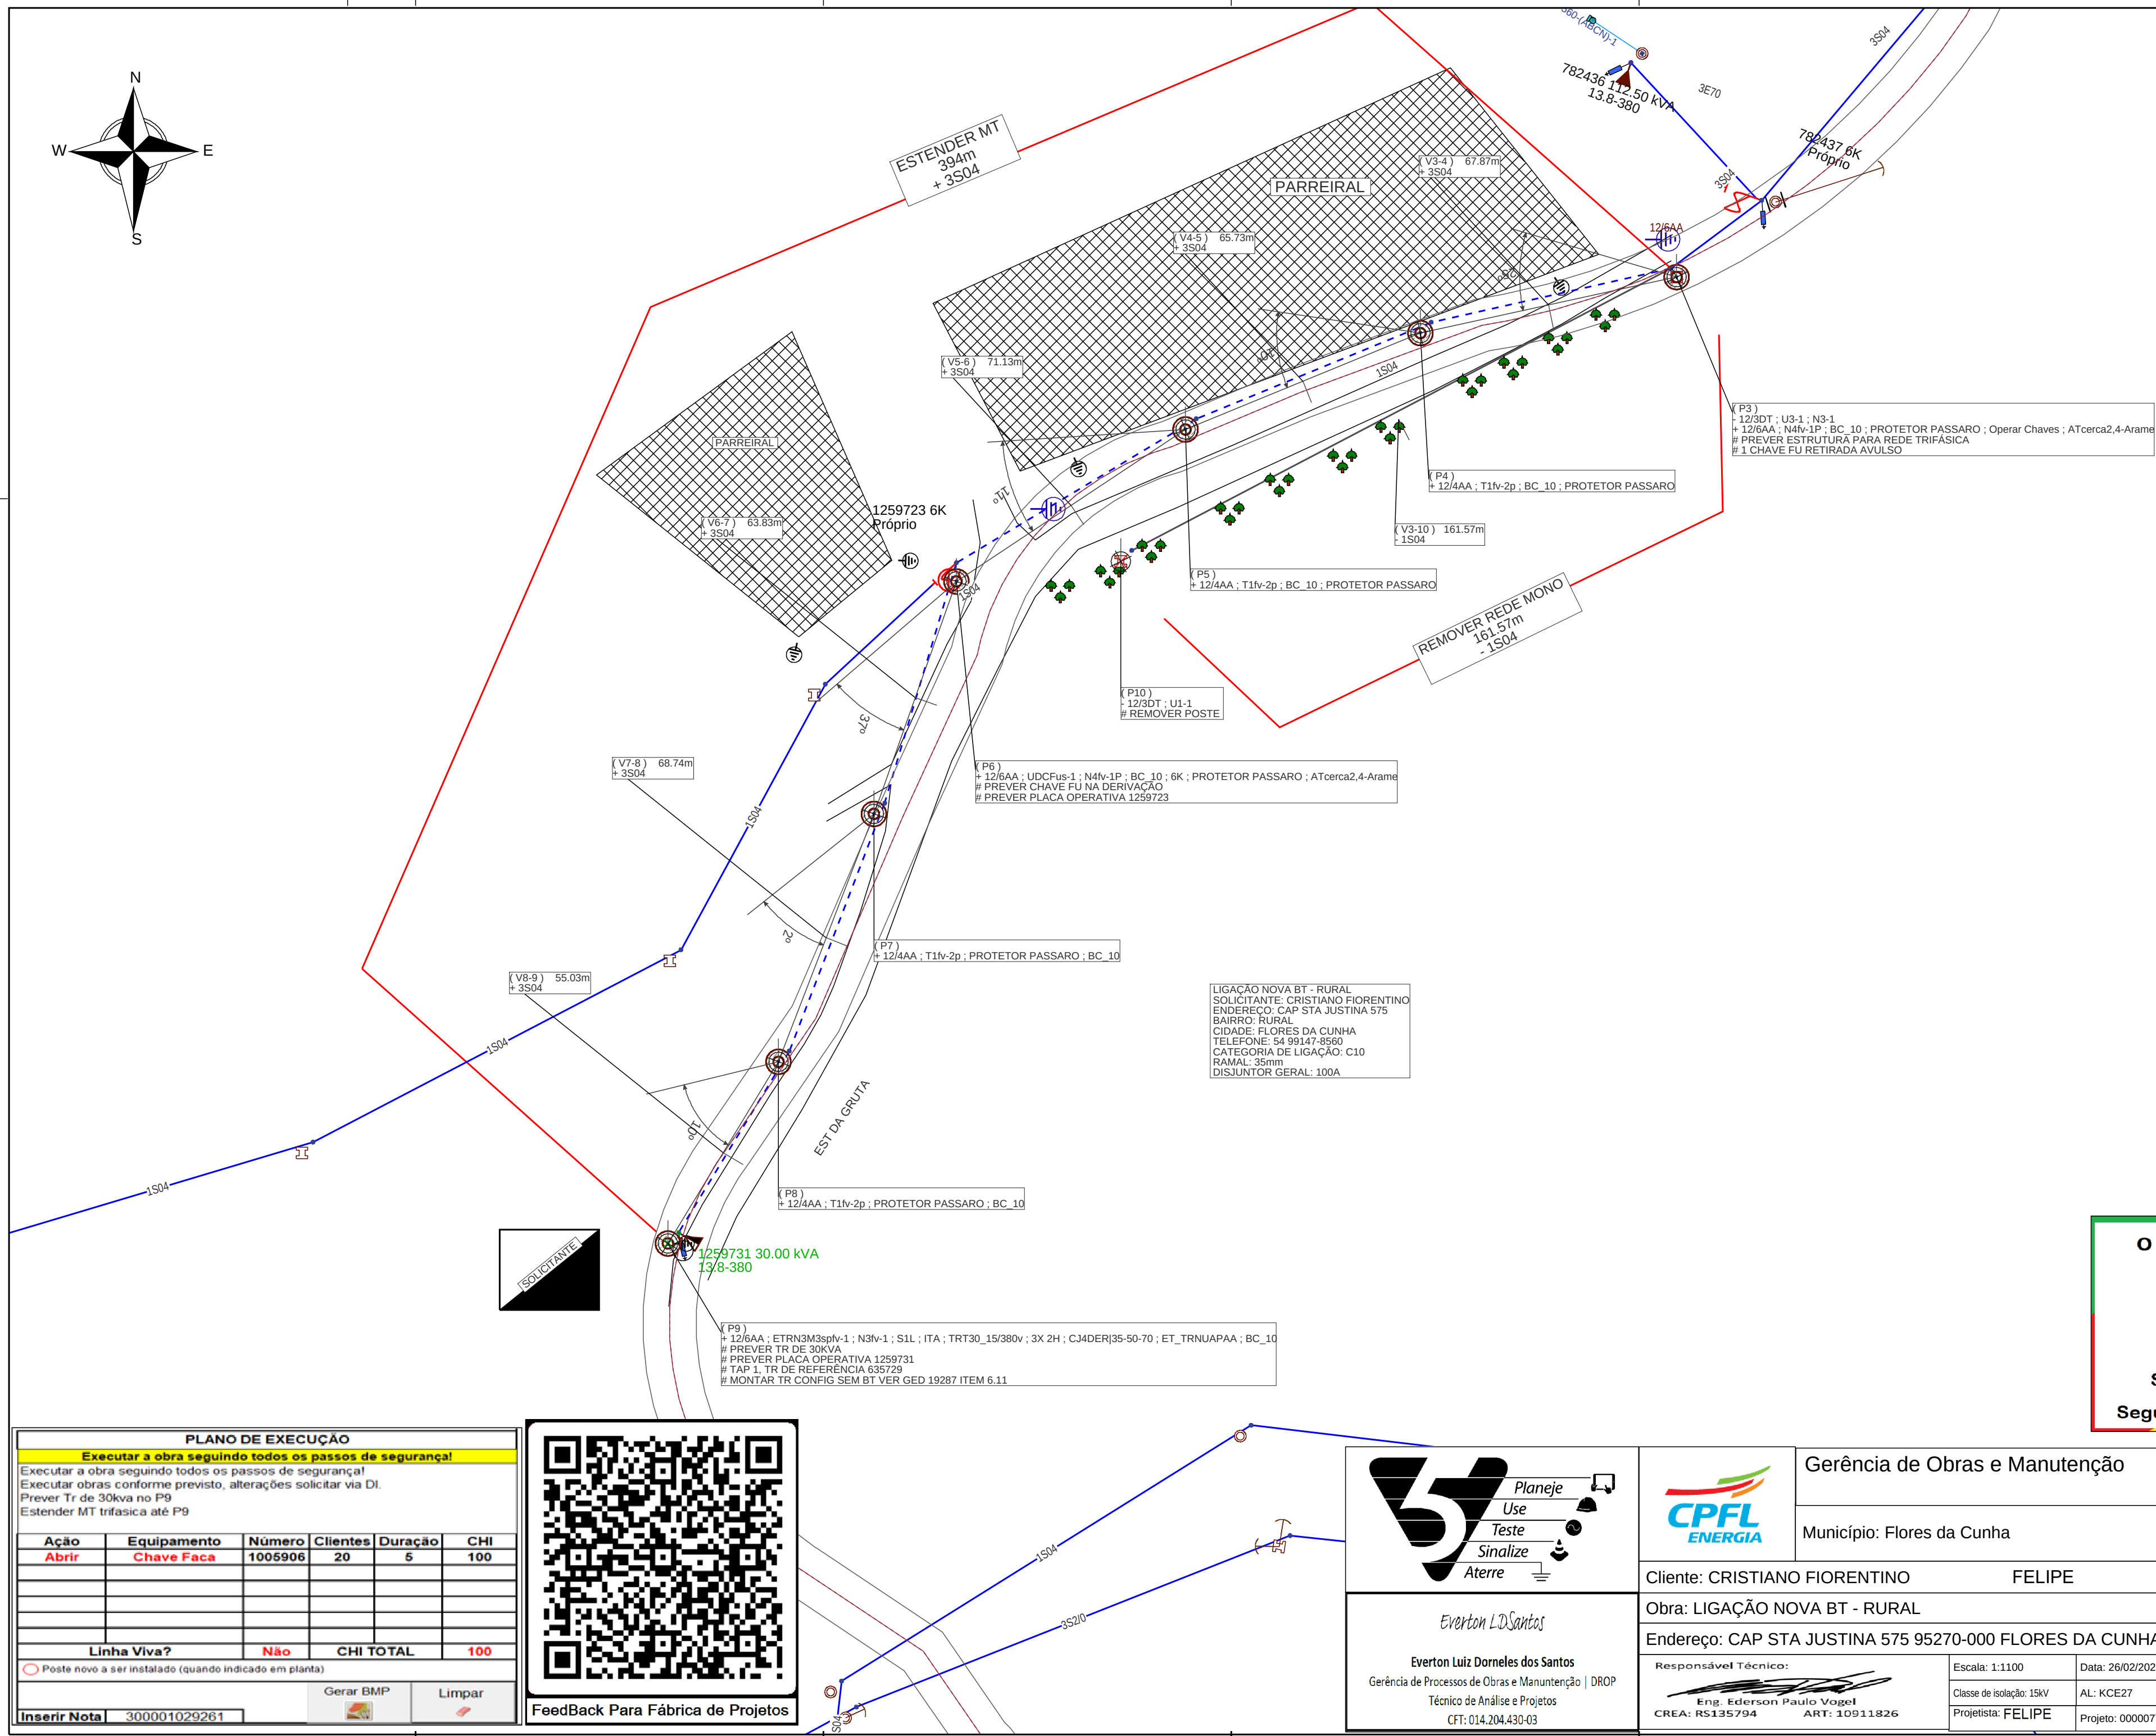


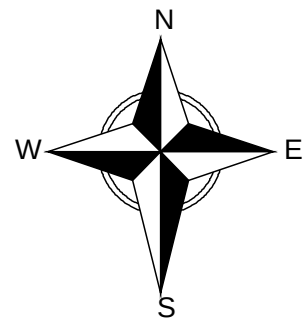

O futuro vai chegar,

Se no presente a
Segurança você adotar!

PLANO DE EXECUÇÃO					
Executar a obra seguindo todos os passos de segurança!					
Executar a obra seguindo todos os passos de segurança!					
Executar obras conforme previsto, alterações solicitar via DI.					
Prever Tr de 30kva no P9					
Estender MT trifasica até P9					
Ação	Equipamento	Número	Clientes	Duração	CHI
Abrir	Chave Faca	1005906	20	5	100
Linha Viva?		Não	CHI TOTAL		100
☐ Poste novo a ser instalado (quando indicado em planta)					
			Gerar BMP	Limpar	
Inserir Nota	300001029261				

FeedBack Para Fábrica de Projetos

Planeje
Use
Teste
Sinalize
Aterre

Everton L.D.Santos
Gerência de Processos de Obras e Manutenção | DROP
Técnico de Análise e Projetos
CFT: 014.204.430-03

Gerência de Obras e Manutenção

Município: Flores da Cunha

Cliente: CRISTIANO FIORENTINO FELIPE

Obra: LIGAÇÃO NOVA BT - RURAL

Endereço: CAP STA JUSTINA 575 95270-000 FLORES DA CUNHA BR RS

Responsável Técnico:

Eng. Ederson Paulo Vogel
CREA: RS135794 ART: 10911826

Escala: 1:1100
Classe de isolamento: 15kV
Projetista: FELIPE

Data: 26/02/2025
AL: KCE27
Projeto: 000007734417

Nota: : 300001079691
Folha 1
Levantador: RICARDO QUEVEDO