


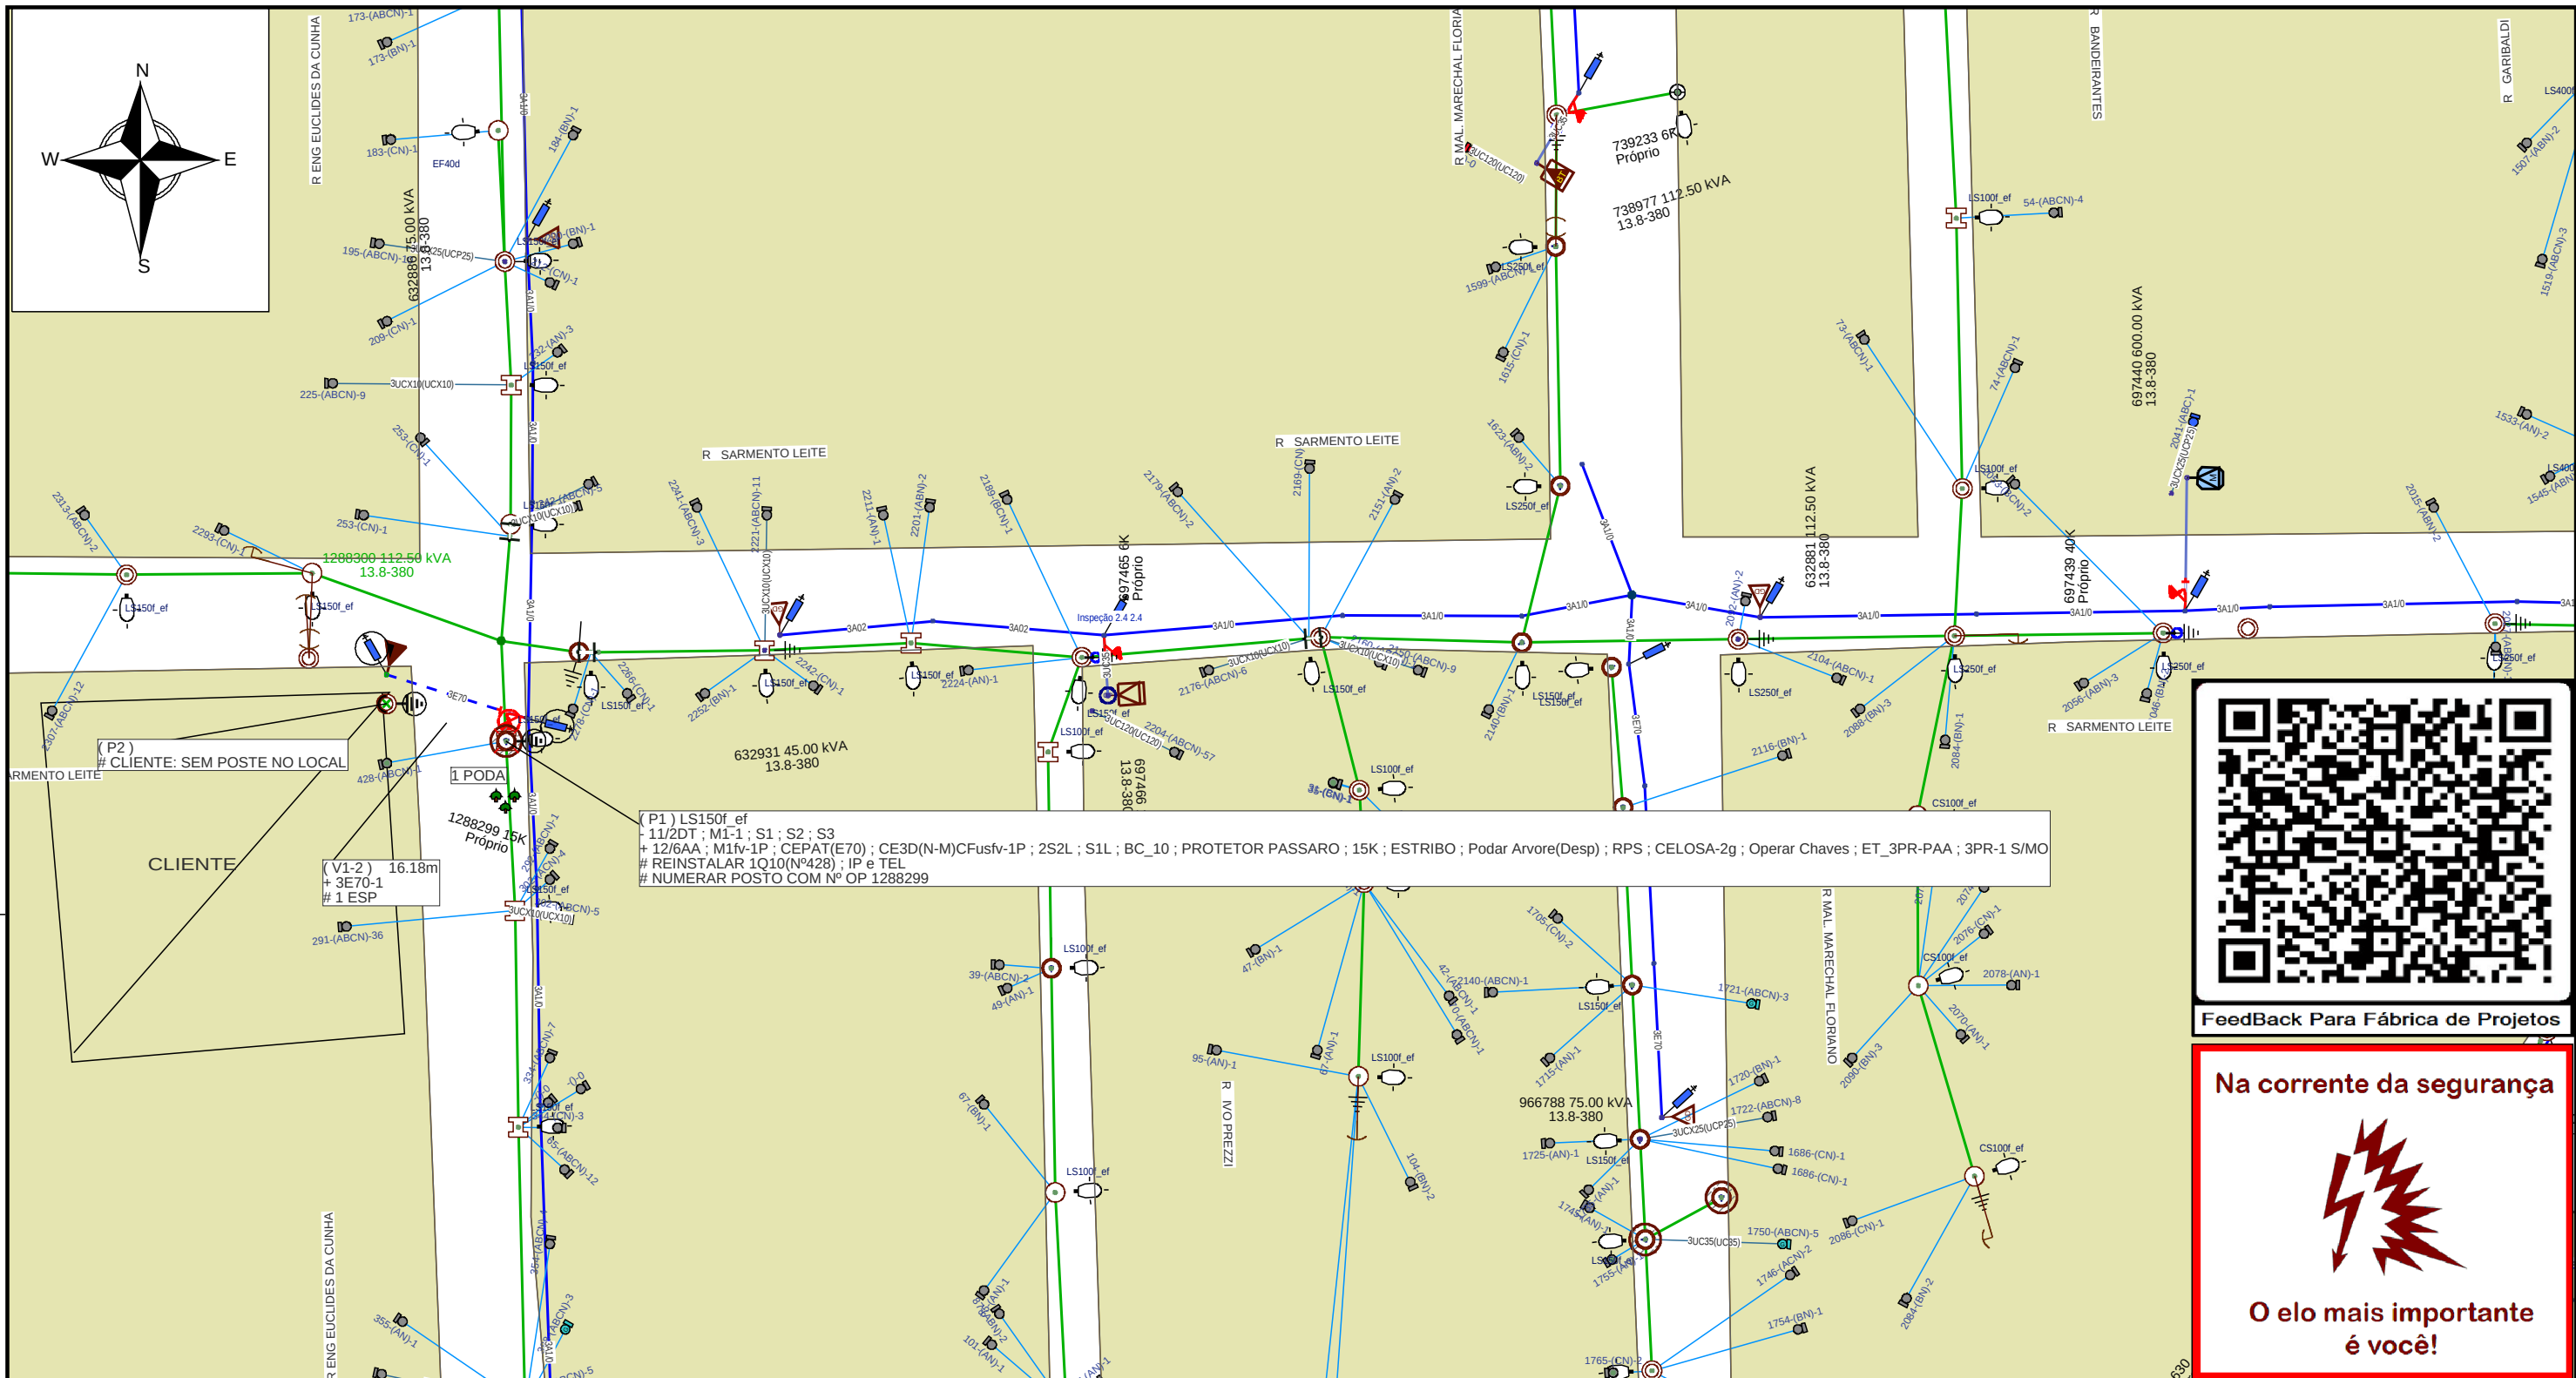

PLANO DE EXECUÇÃO					
Executar a obra seguindo todos os passos de segurança!					
Utilizar equipe de LV para instalar P1. Abrir os equipamentos indicados ABAIXO e executar a obra com LM. Executar atividades de acordo com o projeto. Alterações necessárias no projeto, solicitar via D.I.					
Ação	Equipamento	Número	Clientes	Duração	CHI
Abrir	Transformador	632864	143	4	572
Linha Viva?		Sim	CHI TOTAL		572
 Poste novo a ser instalado (quando indicado em planta)					

Planeje
Use
Teste
Sinalize
Aterre

Luana Candido da Silva

Gerência de Processos de Obras e Manutenção | DROP

Técnico de Análise e Projetos

CFT: 025.291.090-79

	Gerência de Obras e Manutenção		
	Município: Caxias do Sul		
Cliente: SECRETARIA DE EDUCAÇÃO - ESCOLA 1º GRAU			
Obra: ALTERAÇÃO DE CARGA OPTANTE GRUPO B			
Endereço: R ENG EUCLIDES DA CUNHA 428 95084-110 CAXIAS DO SUL BR RS			
 Eng. Ederson Paulo Vogel CREA: RS135794 ART: 10911826	Escala: 1:850	Data: 22/09/2025	Nota: 300001082616
	Classe de isolamento: 15kV	AL: CXG22	Folha 1
	Projetista: Luana Candido	Projeto: 000007885164	Levantador: Reinhold Brulinger