


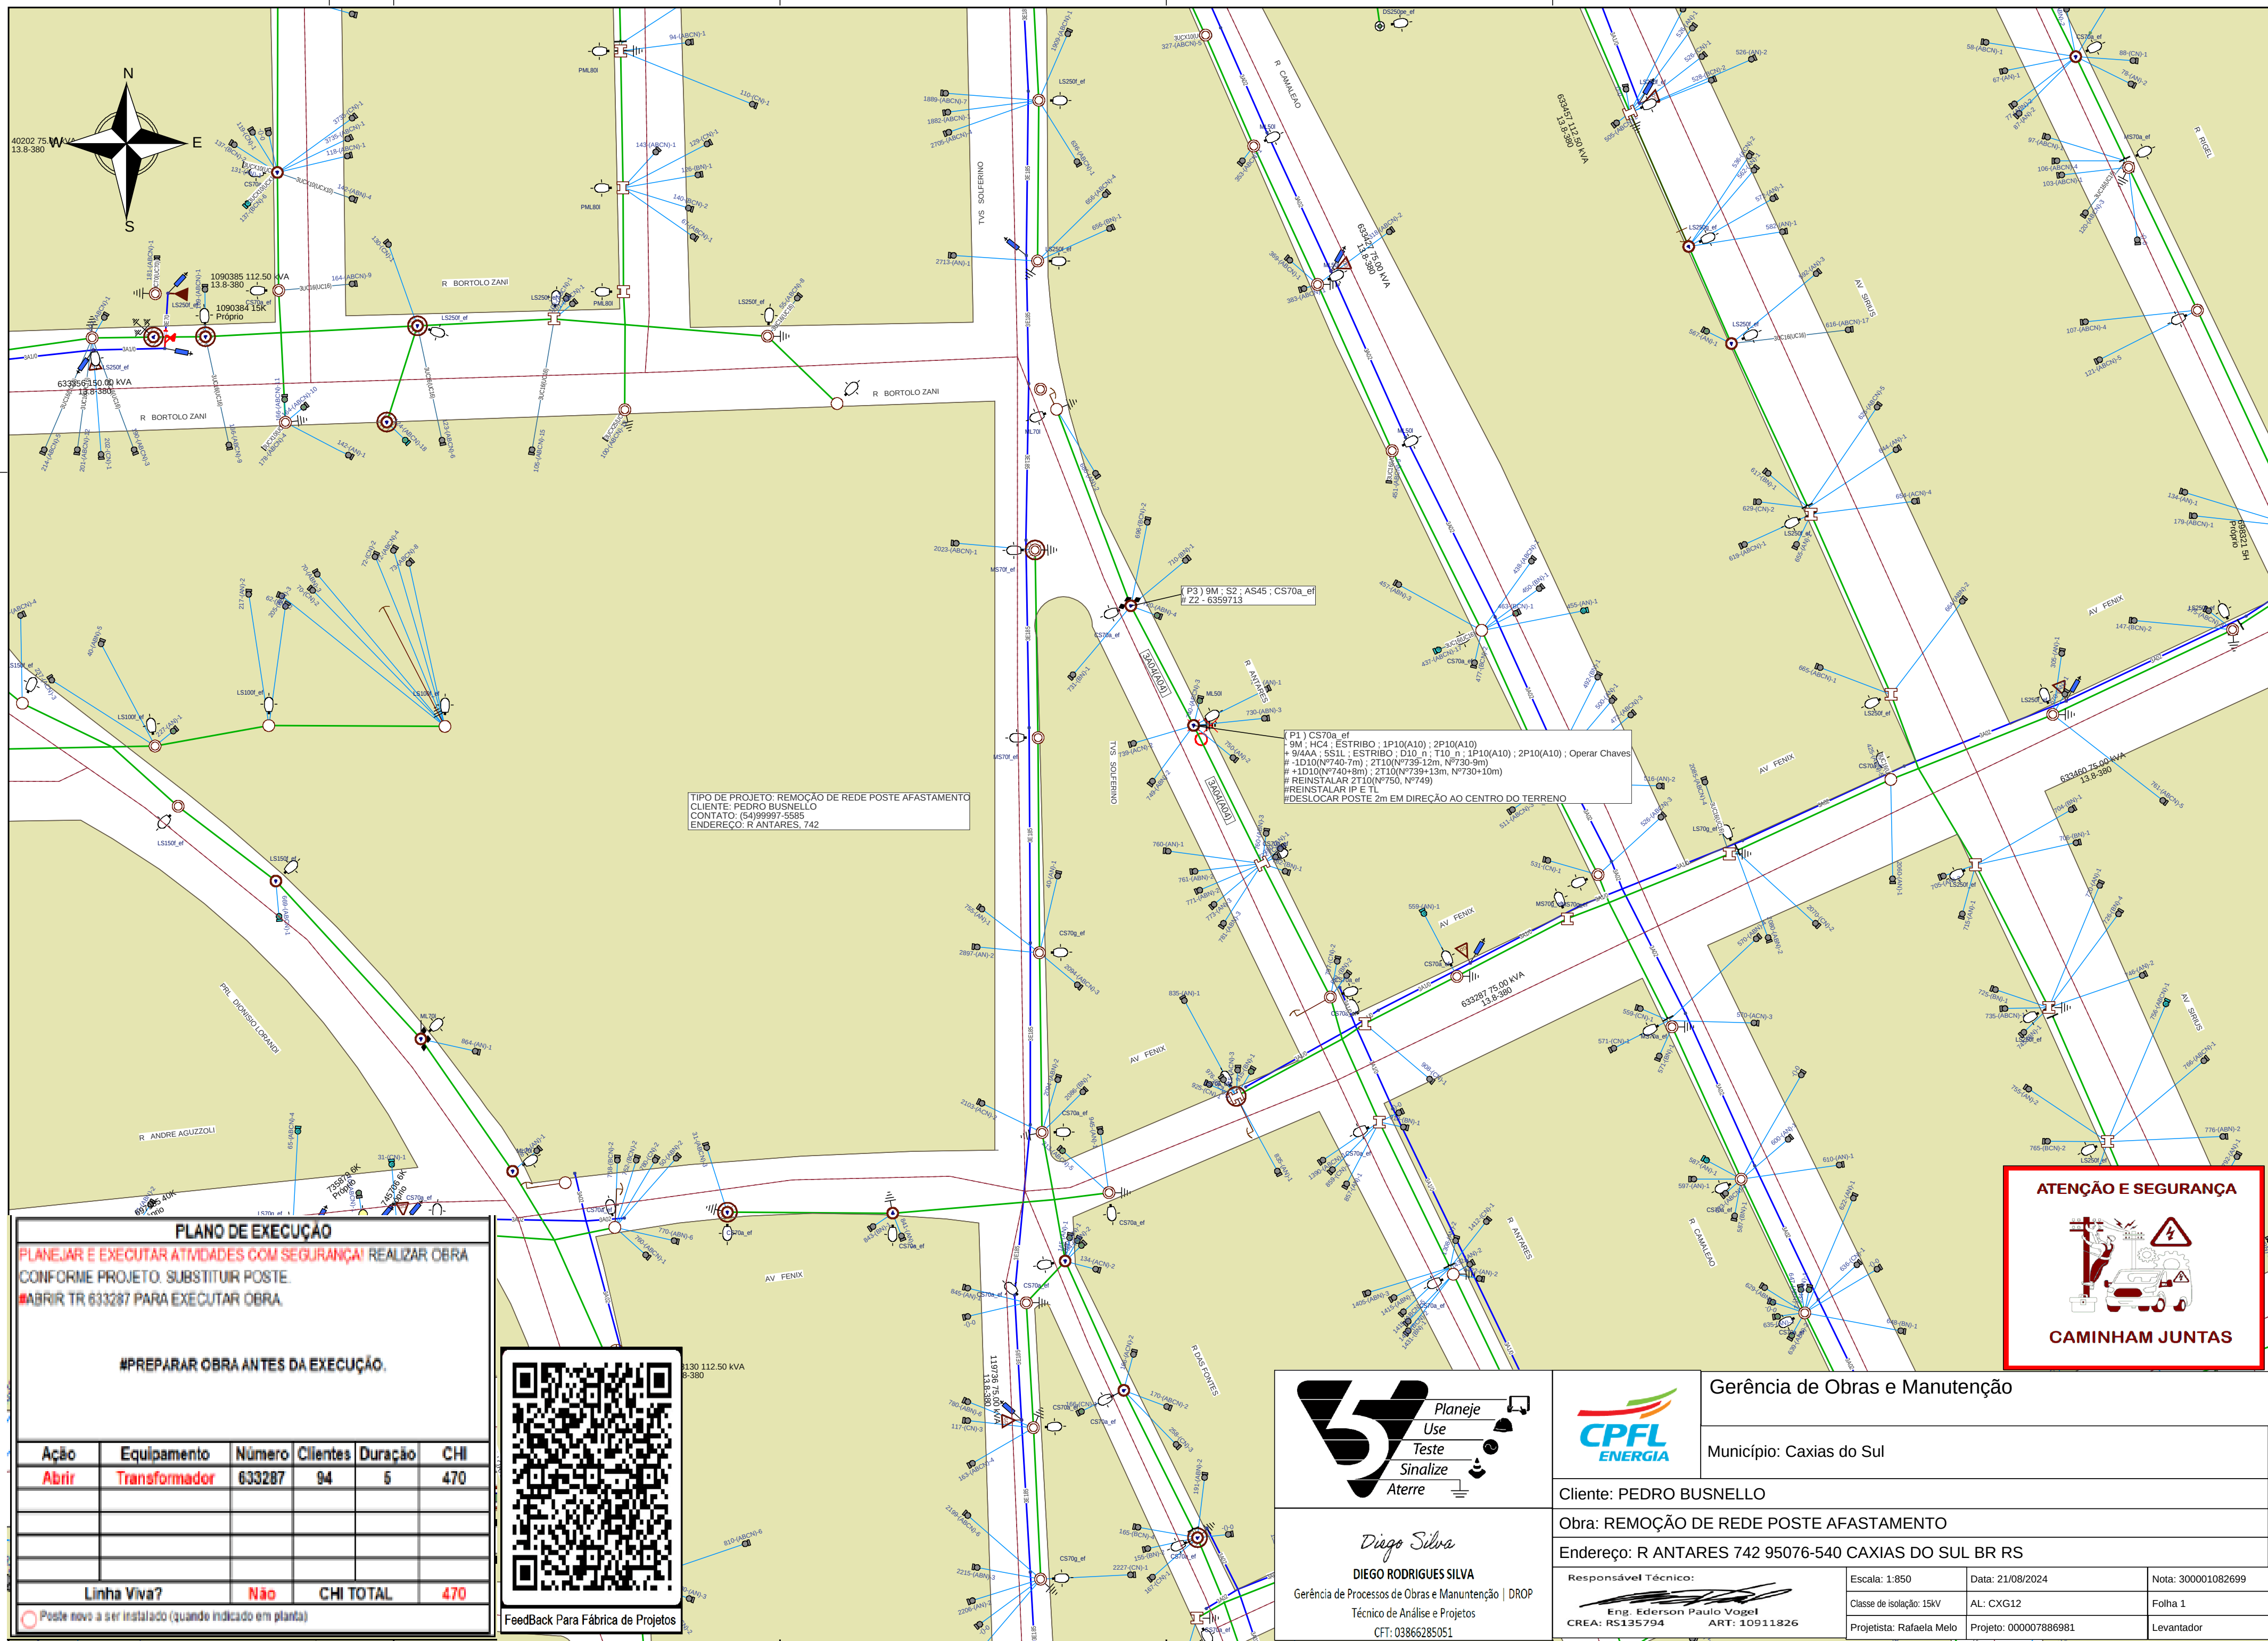

TIPO DE PROJETO: REMOÇÃO DE REDE POSTE AFASTAMENTO
CLIENTE: PEDRO BUSNELLO
CONTATO: (54)99997-5585
ENDEREÇO: R ANTARES, 742

Planeje
Use
Teste
Sinalize
Aterre

Diego Silva

DIEGO RODRIGUES SILVA

Gerência de Processos de Obras e Manutenção | DROP

Técnico de Análise e Projetos

CFT: 03866285051

Gerência de Obras e Manutenção

Município: Caxias do Sul

Cliente: PEDRO BUSNELLO

Obra: REMOÇÃO DE REDE POSTE AFASTAMENTO

Endereço: R ANTARES 742 95076-540 CAXIAS DO SUL BR RS

Responsável Técnico:

Eng. Ederson Paulo Vogel
CREA: RS135794 ART: 10911826

Escala: 1:850
Classe de isolamento: 15KV
Projetista: Rafaela Melo

Data: 21/08/2024
AL: CXG12
Projeto: 000007886981

Nota: 300001082699
Folha 1
Levantador

PLANO DE EXECUÇÃO					
PLANEJAR E EXECUTAR ATMDADES COM SEGURANÇA! REALIZAR OBRA CONFORME PROJETO. SUBSTITUIR POSTE.					
#ABRIR TR 633287 PARA EXECUTAR OBRA.					
#PREPARAR OBRA ANTES DA EXECUÇÃO.					
Ação	Equipamento	Número	Clientes	Duração	CHI
Abrir	Transformador	633287	94	5	470
Linha Viva?		Não	CHI TOTAL		470
☐ Poste novo a ser instalado (quando indicado em planta)					

FeedBack Para Fábrica de Projetos

ATENÇÃO E SEGURANÇA

CAMINHAM JUNTAS