


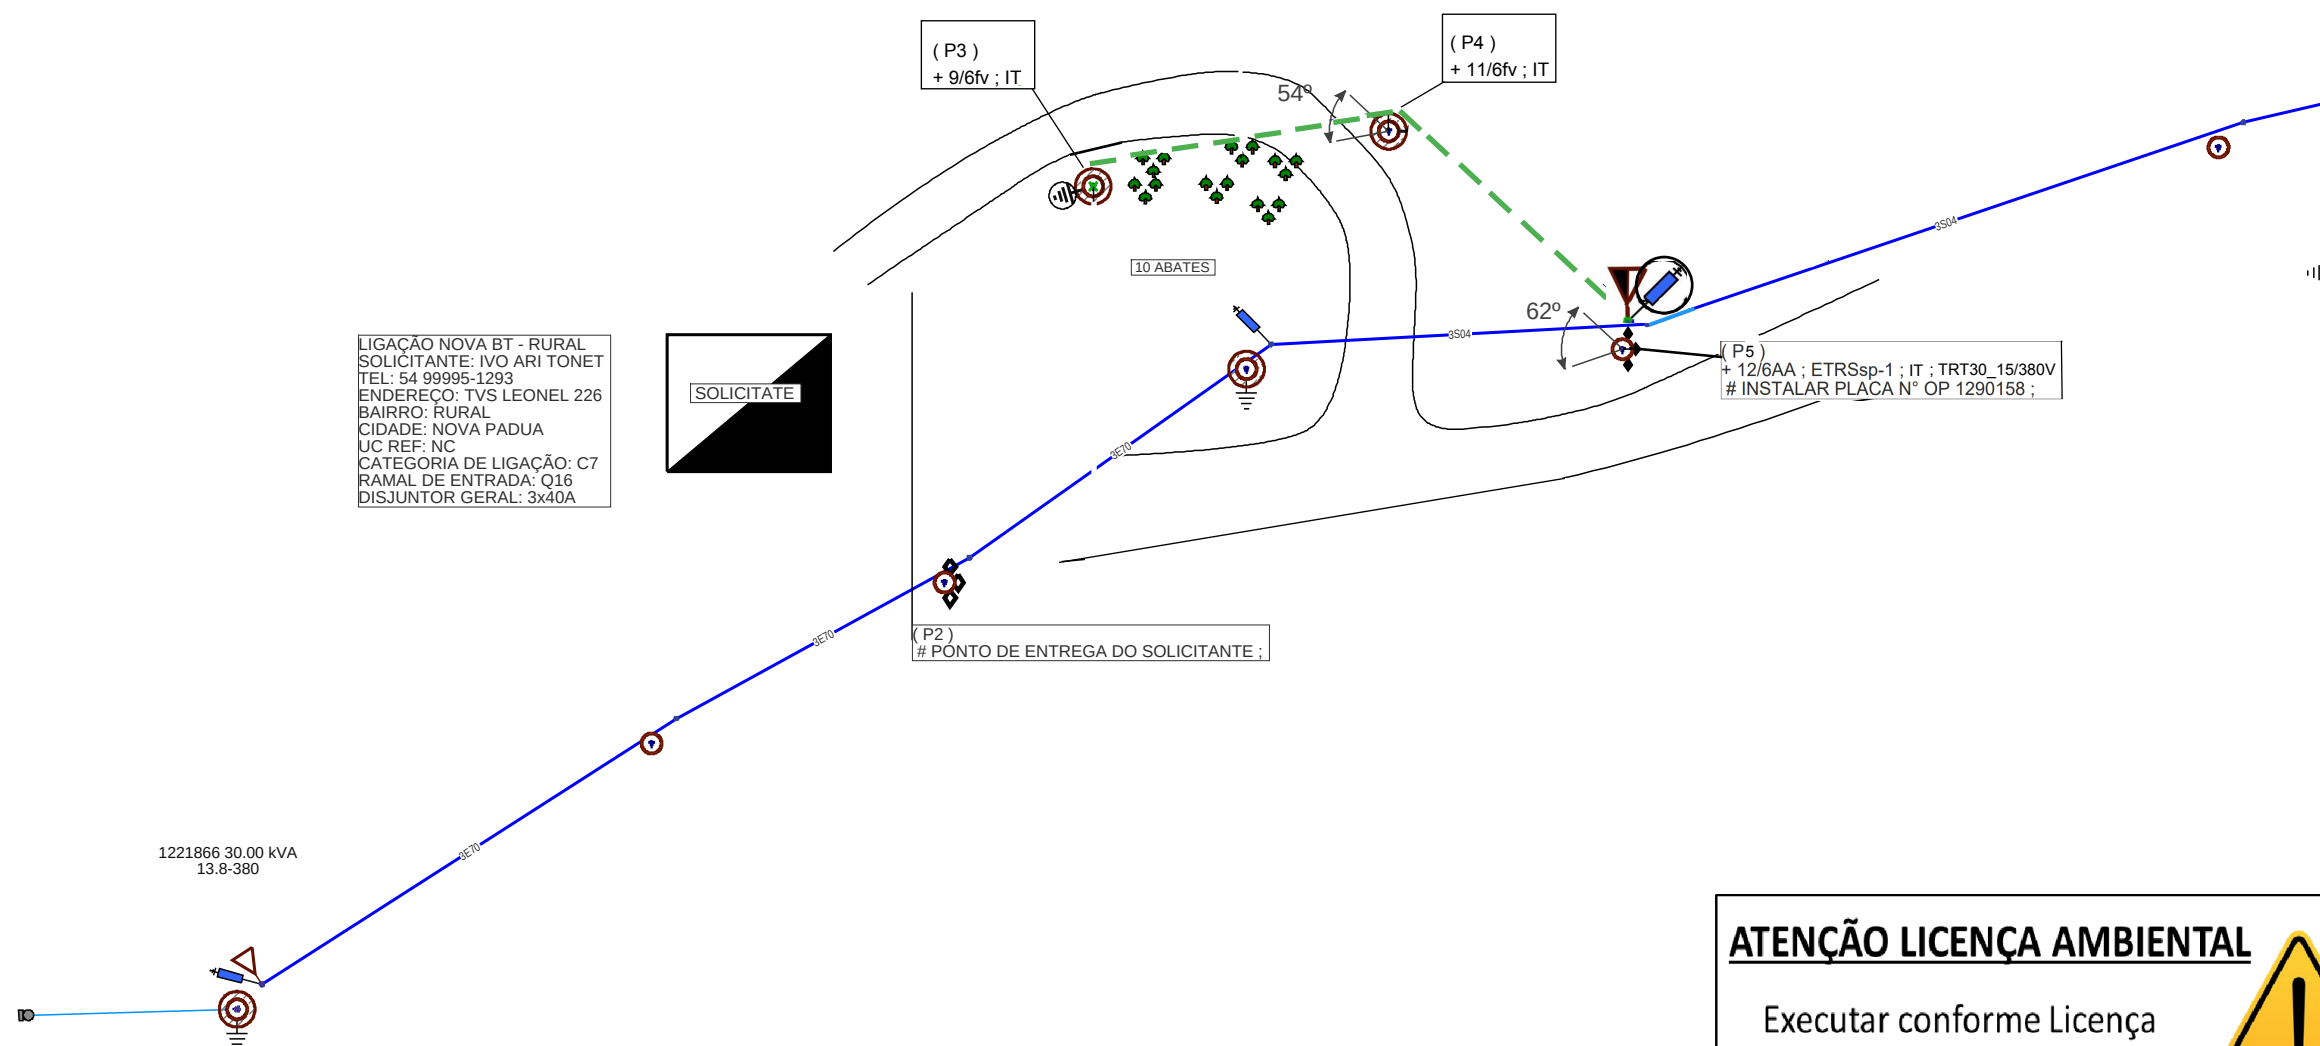


LIGAÇÃO NOVA BT - RURAL
SOLICITANTE: IVO ARI TONET
TEL: 54 99995-1293
ENDEREÇO: TVS LEONEL 226
BAIRRO: RURAL
CIDADE: NOVA PADUA
UC REF: NC
CATEGORIA DE LIGAÇÃO: C7
RAMAL DE ENTRADA: Q16
DISJUNTOR GERAL: 3x40A



Abrir cavas e preparar a obra. Para atividades em Mt e Bt utilizar LM.
Planejado manobrar os equipamentos citados abaixo para execução da obra.
Previsto estender rede Mt para atender nova ligação.
Executar as atividades conforme projeto, demais alterações solicitar via D.I.
MO para manobras paqas em P3.

Ação	Equipamento	Número	Clientes	Duração	CHI
Abrir	Chave Fusível	609400	46	5	230
Linha Viva?		Não	CHI TOTAL		230

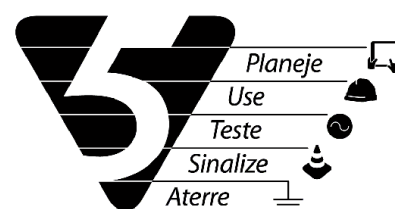

Marcelo da Fontoura Machado
Gerência de Processos de Obras e Manutenção | DROP
Técnico de Análise e Projetos
CFT: 054.031.390-44



Executar conforme Licença
Ambiental anexada no SAP



SEGURANÇA É VIDA.

Município: Nova Pádua

Cliente: IVO ARI TONET

Obra: LIGAÇÃO NOVA BT - RURAL

Endereço: TVS LEONEL 226 95275-000 NOVA PADUA BR RS

Responsável Técnico:

Eng. Ederson Paulo Vogel
CREA: RS135794 ART: 10911826

Escala: 1:850

Classe de isolamento:	
-----------------------	--

15KV
Projetista: Marcelo Machado

	Data: 03/10/2025
--	------------------

AL: FCU21

Projeto: 000007894058

Nota:	300001082889
-------	--------------

Folha 1

Levantador: Marcio Bedin
