


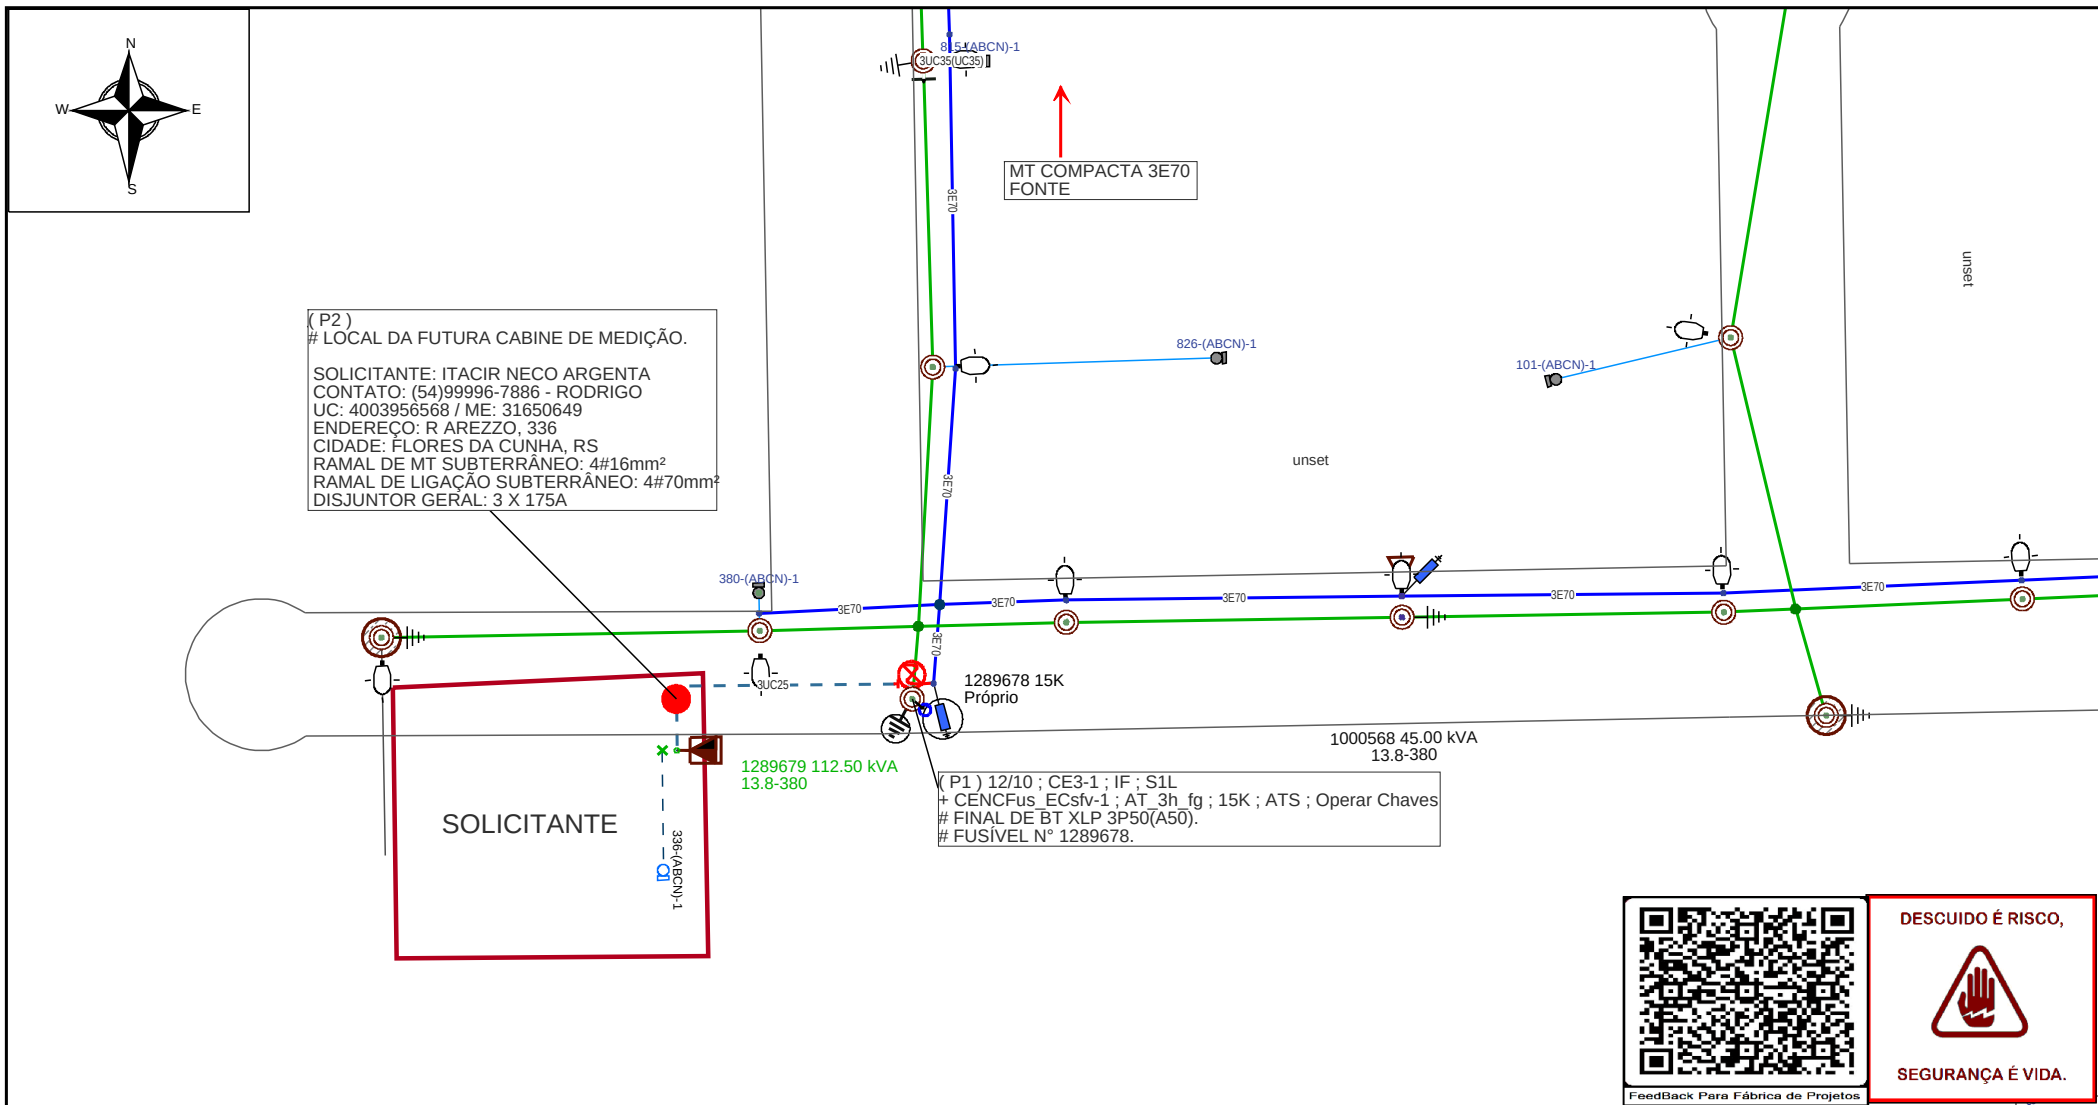

PLANO DE EXECUÇÃO					
EXECUTAR ATIVIDADES COM SEGURANÇA!					
INSTALAR CHAVE FUSIVEL COM ENTRADA SUBTERRÂNEA PARA MUFLA PARTICULAR.					
EXECUTAR ATIVIDADES DE ACORDO COM O PROJETO. ALTERAÇÕES, SOLICITAR D.I.					
Ação	Equipamento	Número	Clientes	Duração	CHI
Abrir	Chave Fusível	897542	33	5	165
Linha Viva?		Não	CHI TOTAL		165

Planeje
Use
Teste
Sinalize
Aterre

Edson Dilmar Papalia Flores
Edson Dilmar Papalia Flores
Gerência de Processos de Obras e Manutenção | DROP
Técnico de Análise e Projetos
CFT: 220.942.817-3

CPFL ENERGIA

Gerência de Obras e Manutenção

Município: Flores da Cunha

Obra: ALTERAÇÃO DE CARGA OPTANTE GRUPO B

Cliente: ITACIR NECO ARGENTA

Endereço: R AREZZO 336 95270-000 FLORES DA CUNHA BR RS

Responsável Técnico:	Escala: 1:800	Data: 29/09/2025	Nota: 300001084373
Eng. Ederson Paulo Vogel CREA: RS135794 ART: 10911826	Classe de isolamento: 15kV	AL: FCU25	Folha 1
Projetista: EDSON PAPALIA	Projeto: 000007890259	Levantador: RICARDO DE ALBUQUERQUE	