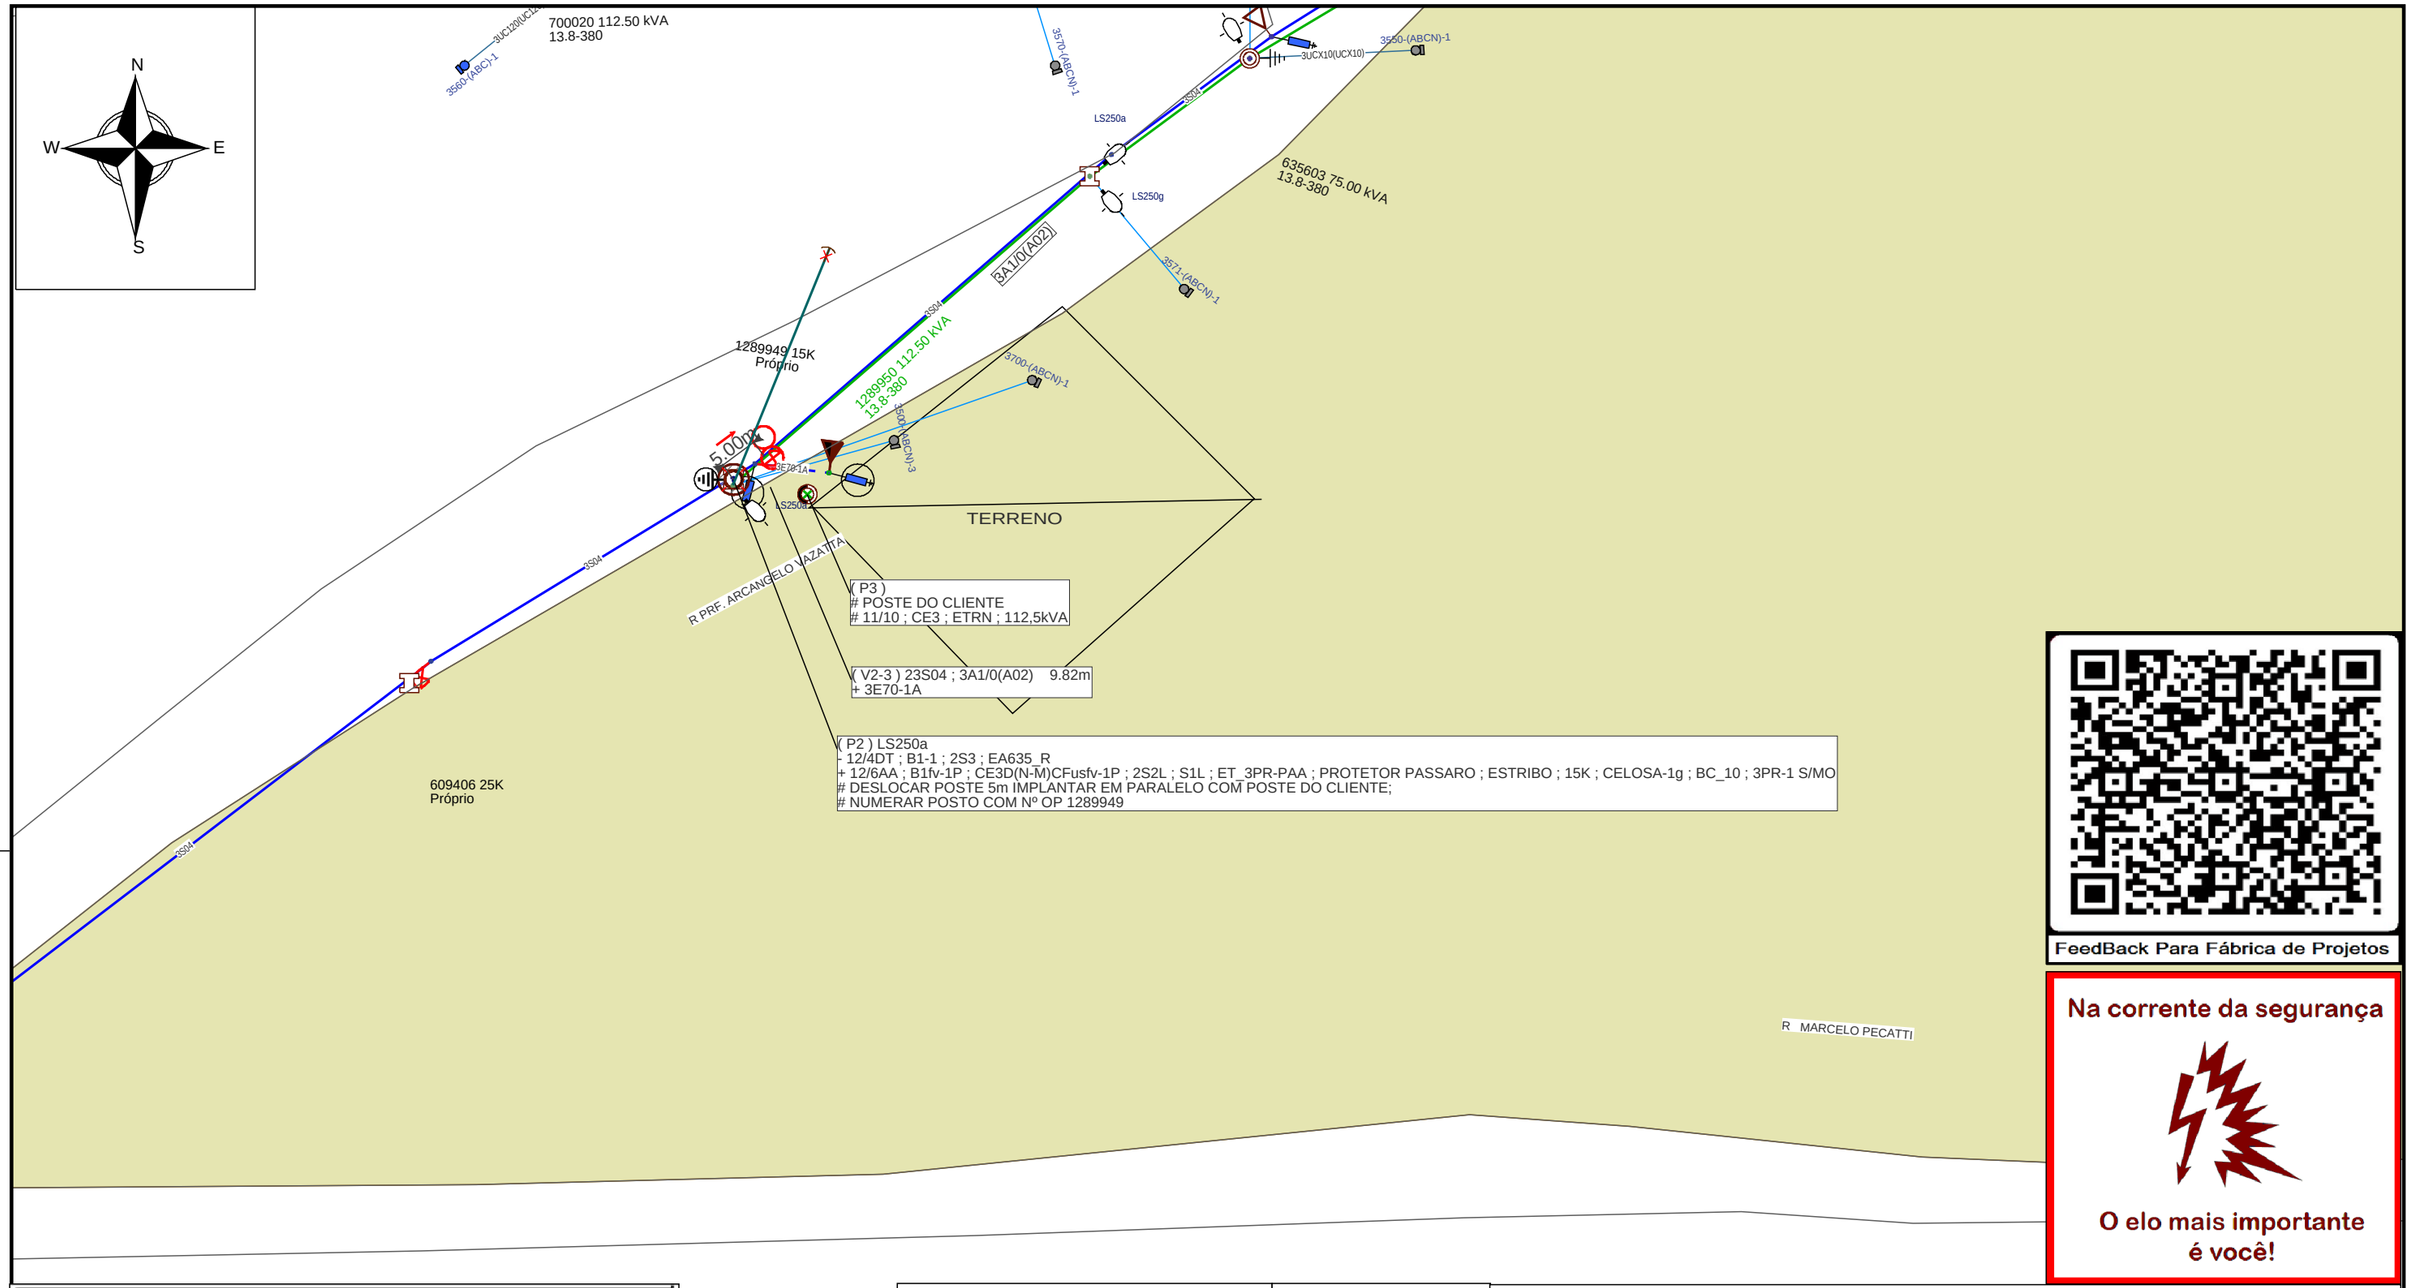

FeedBack Para Fábrica de Projetos

Na corrente da segurança

O elo mais importante é você!

PLANO DE EXECUÇÃO

Executar a obra seguindo todos os passos de segurança!

Abrir os equipamentos indicados ABAIXO e executar a obra com LM.
Executar atividades de acordo com o projeto.
Alterações necessárias no projeto, solicitar via D.I.

Ação	Equipamento	Número	Clientes	Duração	CHI
Abrir	Chave Faca	604169	148	5	740
Abrir	Religador	916614	0	5	0
Fechar	Religador	1050257	0	5	0
Linha Viva?		Não	CHI TOTAL		740

◯ Poste novo a ser instalado (quando indicado em planta)

Planeje
Use
Teste
Sinalize
Aterre

Luana Candido da Silva

Luana Candido da Silva
Gerência de Processos de Obras e Manuntenção | DROP
Técnico de Análise e Projetos
CFT: 025.291.090-79

CPFL ENERGIA

Gerência de Obras e Manutenção

Município: Nova Pádua

Cliente: LEANDRO SALVADOR

Obra: ALTERAÇÃO DE CARGA OPTANTE GRUPO B

Endereço: R PROF ARCANGELO VAZATTA 3700 95275-000 NOVA PADUA BR RS

Responsável Técnico:
Eng. Ederson Paulo Vogel
CREA: RS135794 ART: 10911826

Escala: 1:800	Data: 02/10/2025	Nota: 300001085257
Classe de isolação: 15kV	AL: FCU21	Folha 1
Projetista: Luana Candido	Projeto: 000007893770	Levantador: Marcio Bedin