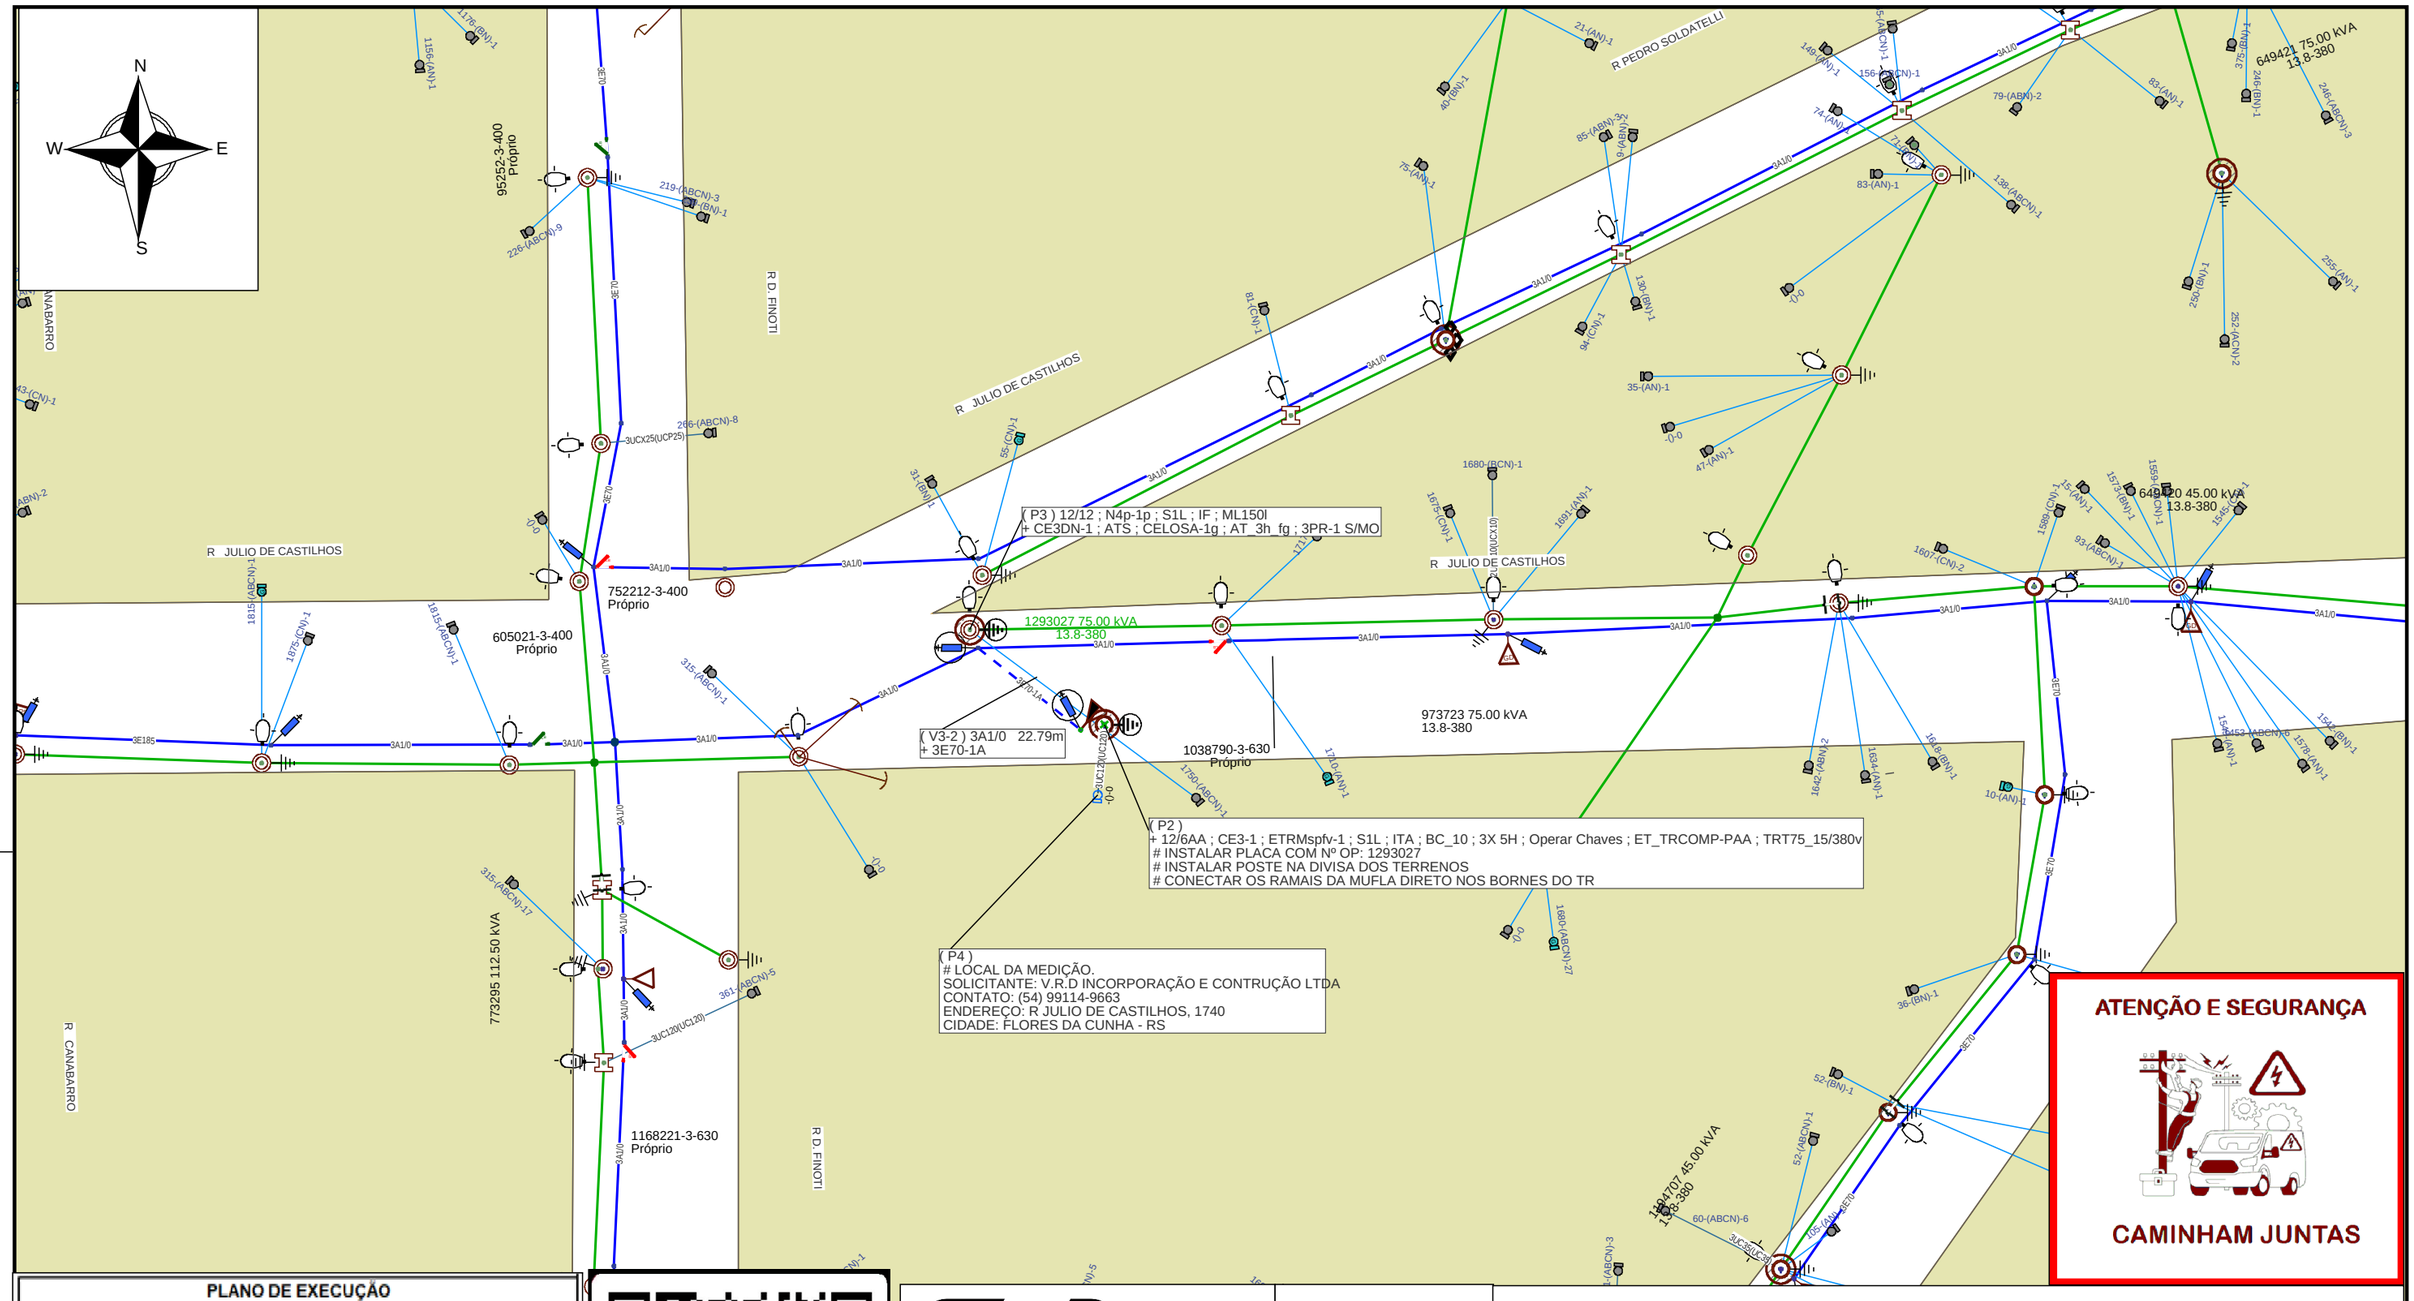

PLANO DE EXECUÇÃO

Executar a obra seguindo todos os passos de segurança!

SUGERIDO A EXECUÇÃO DA OBRA COM LINHA VIVA NO P3, DESLIGANDO A BT, E NO P2 EXECUTAR COM LM

Ação	Equipamento	Número	Clientes	Duração	CHI
Desligar	Transformador	973723	39	5	195
Linha Viva?		Sim	CHI TOTAL		195

◯ Poste novo a ser instalado (quando indicado em planta)

FeedBack Para Fábrica de Projetos

Planeje
Use
Teste
Sinalize
Aterre

Luiz F. j. de Moraes

Luiz Felipe Jardim de Moraes
Gerência de Processos de Obras e Manuntenção | DROP
Técnico de Análise e Projetos
CFT: 03762632022

CPFL ENERGIA

Gerência de Obras e Manutenção

Município: Flores da Cunha

Cliente: V.R.D INCORPORACAO E CONSTRUCAO LTDA

Obra: LIGAÇÃO NOVA EDIFICIO - COLETIVO

Endereço: R ENDERECO PROVISORIO S/N1 99999-999 FLORES DA CUNHA BR RS

Responsável Técnico:
Eng. Ederson Paulo Vogel
CREA: RS135794 ART: 10911826

Escala: 1:850	Data: 23/10/2025	Nota: 300001090718
Classe de isolação: 15kV	AL: FCU23	Folha 1
Projetista: Luiz Felipe	Projeto: 000007907887	Levantador: Marcio Bedin