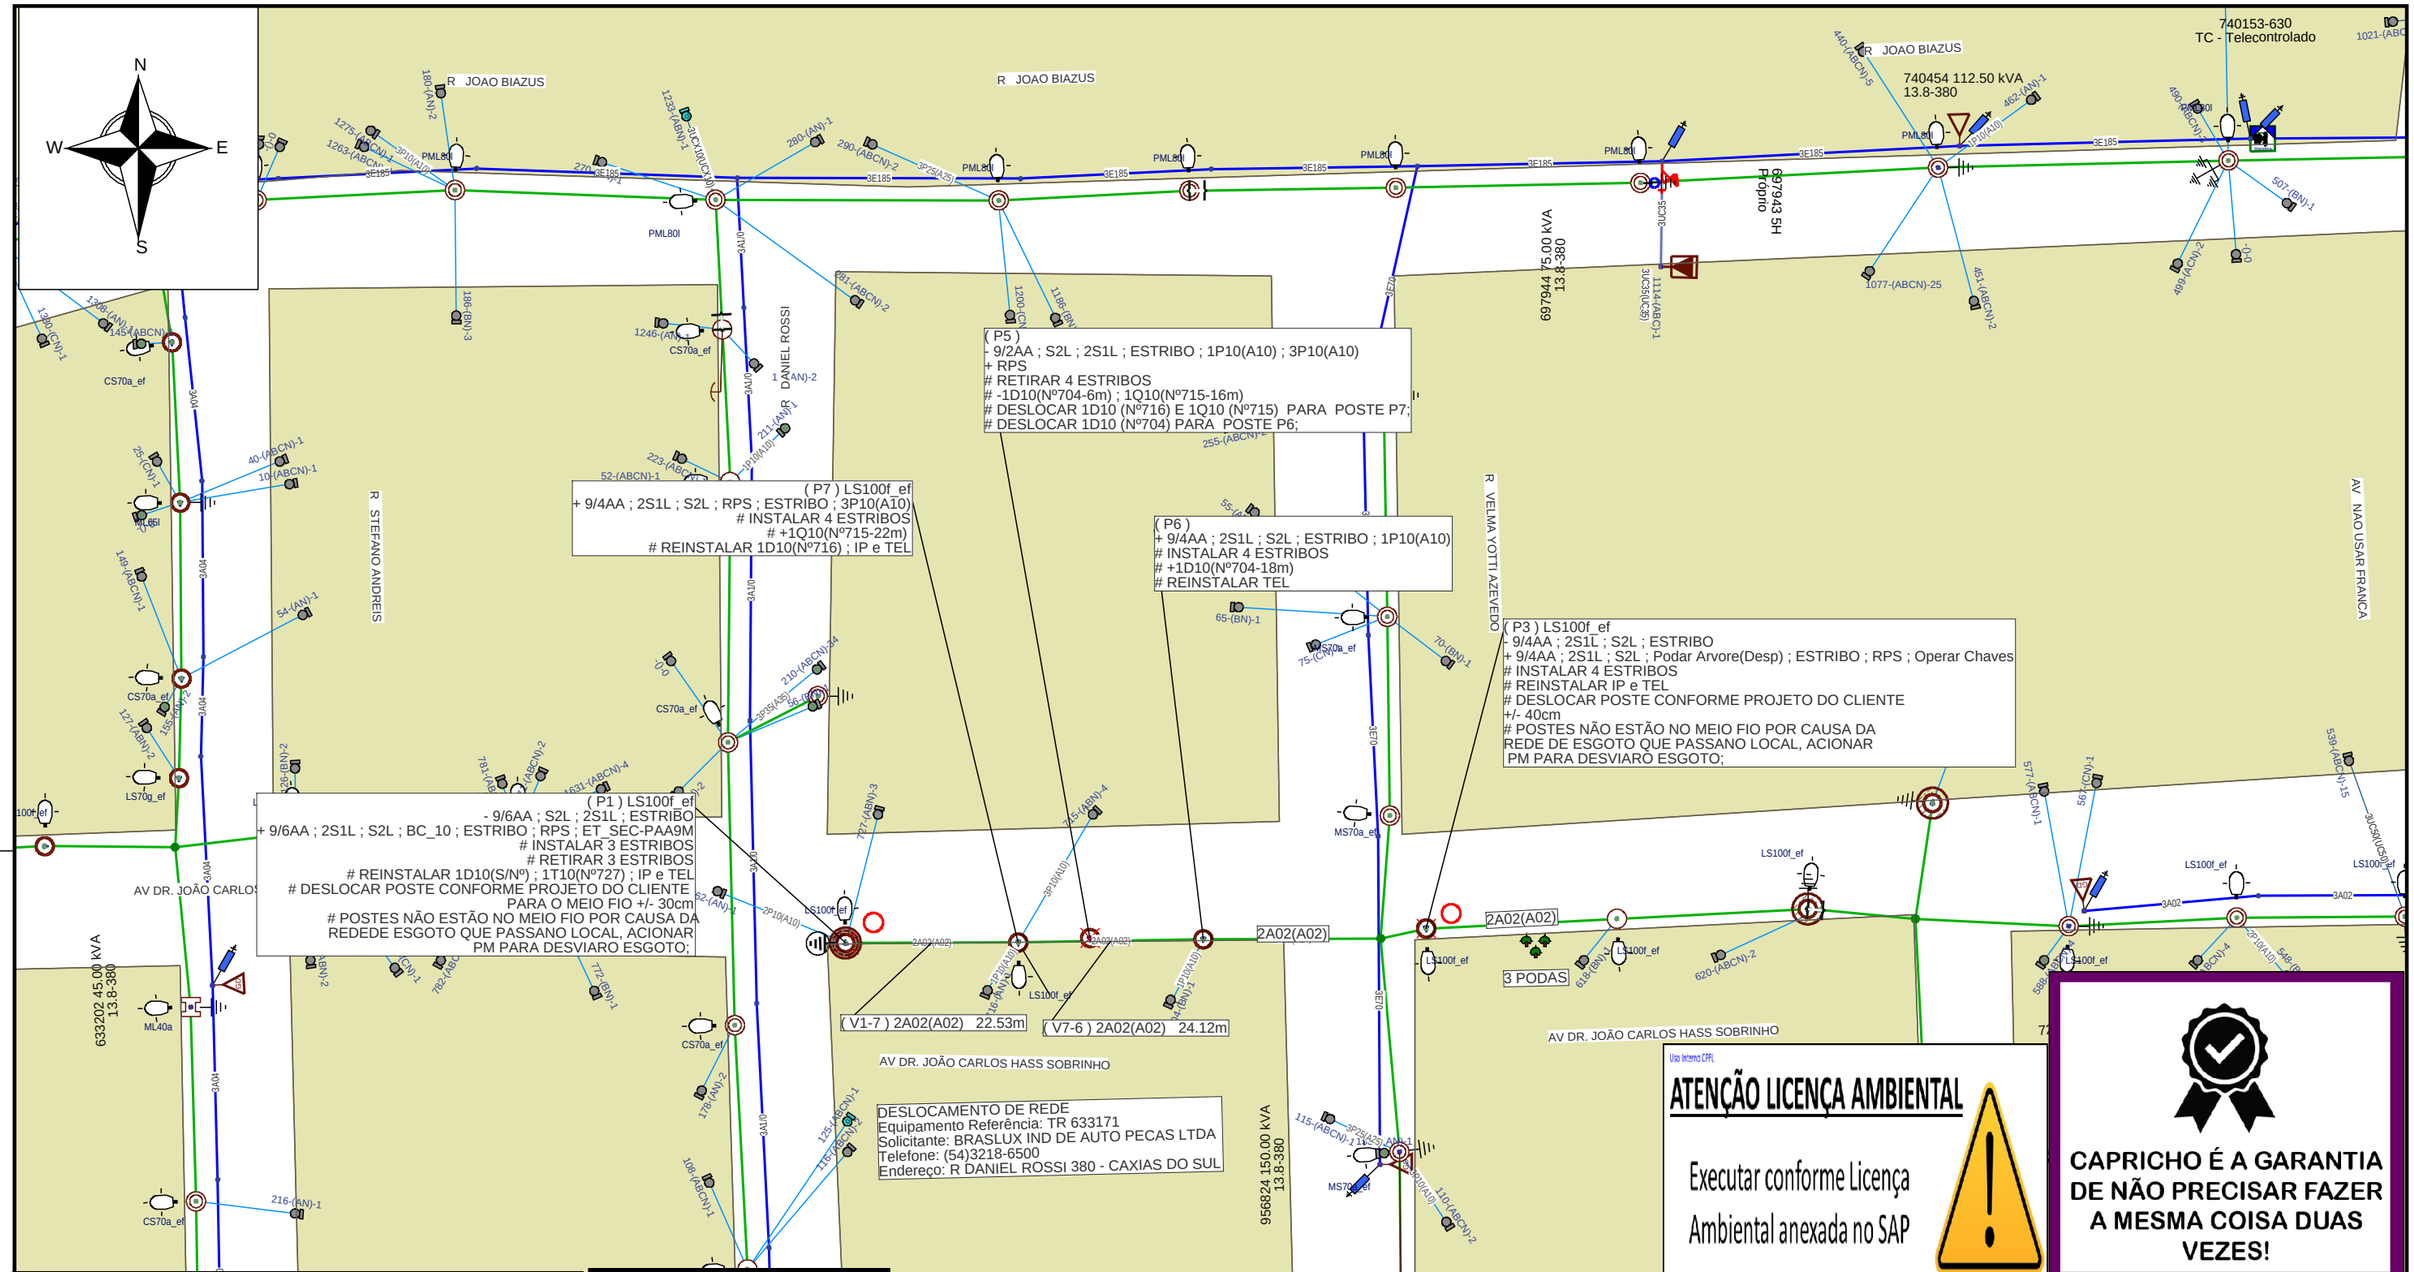

PLANO DE EXECUÇÃO

ABRIR CAVAS E PREPARAR OBRA PARA INSTALAÇÃO DE POSTES
REALIZAR TRABALHOS COM SEGURANÇA

P1: DESLOCAR O POSTE PARA O MEIO FIO (+OU- 30 cm);
P7 E P6: INSTALAR POSTE;
P5: RETIRAR POSTE;
P3: DESLOCAR POSTE PARA O MEIO FIO (+ OU- 40 cm);

Ação	Equipamento	Número	Clientes	Duração	CHI
Abrir	Transformador	956824	35	4	140
Linha Viva?		Não	CHI TOTAL		140

◯ Poste novo a ser instalado (quando indicado em planta)

FeedBack Para Fábrica de Projetos

Planeje
Use
Teste
Sinalize
Aterre

Ana Paula Bloedorn
Gerência de Processos de Obras e Manutenção | DROP
Técnico de Projetos II
CFT: 002.795.320-32

CPFL ENERGIA

Gerência de Obras e Manutenção

Município: Caxias do Sul

Cliente: BRASLUX IND DE AUTO PECAS LTDA

Obra: REMOÇÃO DE REDE POSTE AFASTAMENTO

Endereço: R DANIEL ROSSI 380 95076-100 CAXIAS DO SUL BR RS

Responsável Técnico:
Eng. Ederson Paulo Vogel
CREA: RS135794 ART: 10911826

Escala: 1:800	Data: 04/11/2025	Nota: 300001091200
Classe de isolação: 15kV	AL: CXC12	Folha 1
Projetista: Ana Paula	Projeto: 000007915189	Levantador REINHOLDO BRULINGER