


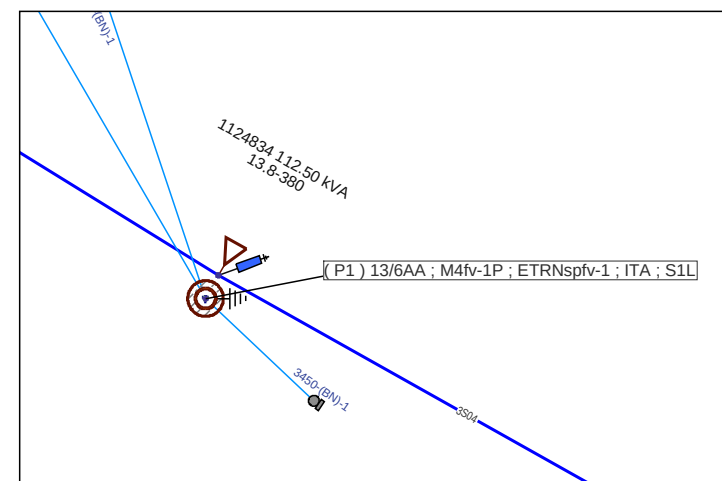

TIPO DE NOTA: LIGAÇÃO NOVA BT - RURAL
SOLICITANTE: MARLON DE SOUZA
TELEFONE: (51) 99884-0453
ENDEREÇO: EST MUN GUILHERME SCHUMANN 50
EQUIPAMENTO DE REFERÊNCIA: TR1124834
ALIMENTADOR: CXD22
CATEGORIA DE LIGAÇÃO: C8
RAMAL AEREO: Q16
DISJUNTOR: 1x63A



SOLICITANTE

AL: CXD2
CARGA

1301106 30.00 kV
13.8-380

(P3) 12/4; T1cl-2P
+ ETRBspfv-1; S1L; ITA; 3X 2H; ATS; ET_Trt; TRT30_15/380v
INSTALAR TR DE 30kVA
INSTALAR PLACA DE Nº OP: 1301106
MONTAR TR SEM BT CONFORME GED 19287
TAP 1 TR 1124834 DE REFERÊNCIA

AL: CXD22
FONTE




**Funcionário
inteligente,
previne o
acidente!**

Executar a obra seguindo todos os passos de segurança!

Manobrar equipamento abaixo para realizar a obra.

☐ Poste novo a ser instalado (quando indicado em planta)

FeedBack Para Fábrica de Projetos

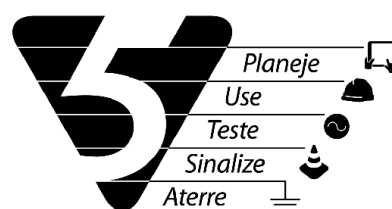

Wellerson Avila

Wellerson Amaral Avila

Gerência de Processos de Obras e Manutenção | DROP

Técnico de Análise e Projetos

CFT: 04993185014



Gerência de Obras e Manutenção

Município: Caxias do Sul

Cliente: MARLON DE SOUZA

Obra: LIGAÇÃO NOVA BT

Endereço: EST MUN GUILHERME SCHUMANN 50 95100-000 CAXIAS DO SUL BR RS

Responsável Técnico:

Eng. Ederson Paulo Vogel
CREA: RS135794 ART: 10911826

Escala: 1:850

Data: 07/01/2026

Nota:	300001092946
-------	--------------

Classe de isolamento:	15kV
Projetista:	Wellerson Avila

AL: CXD22

	3000010
	Folha 1

Projeto: 000007958229

	Levantador Ricardo Quevedo
--	----------------------------