
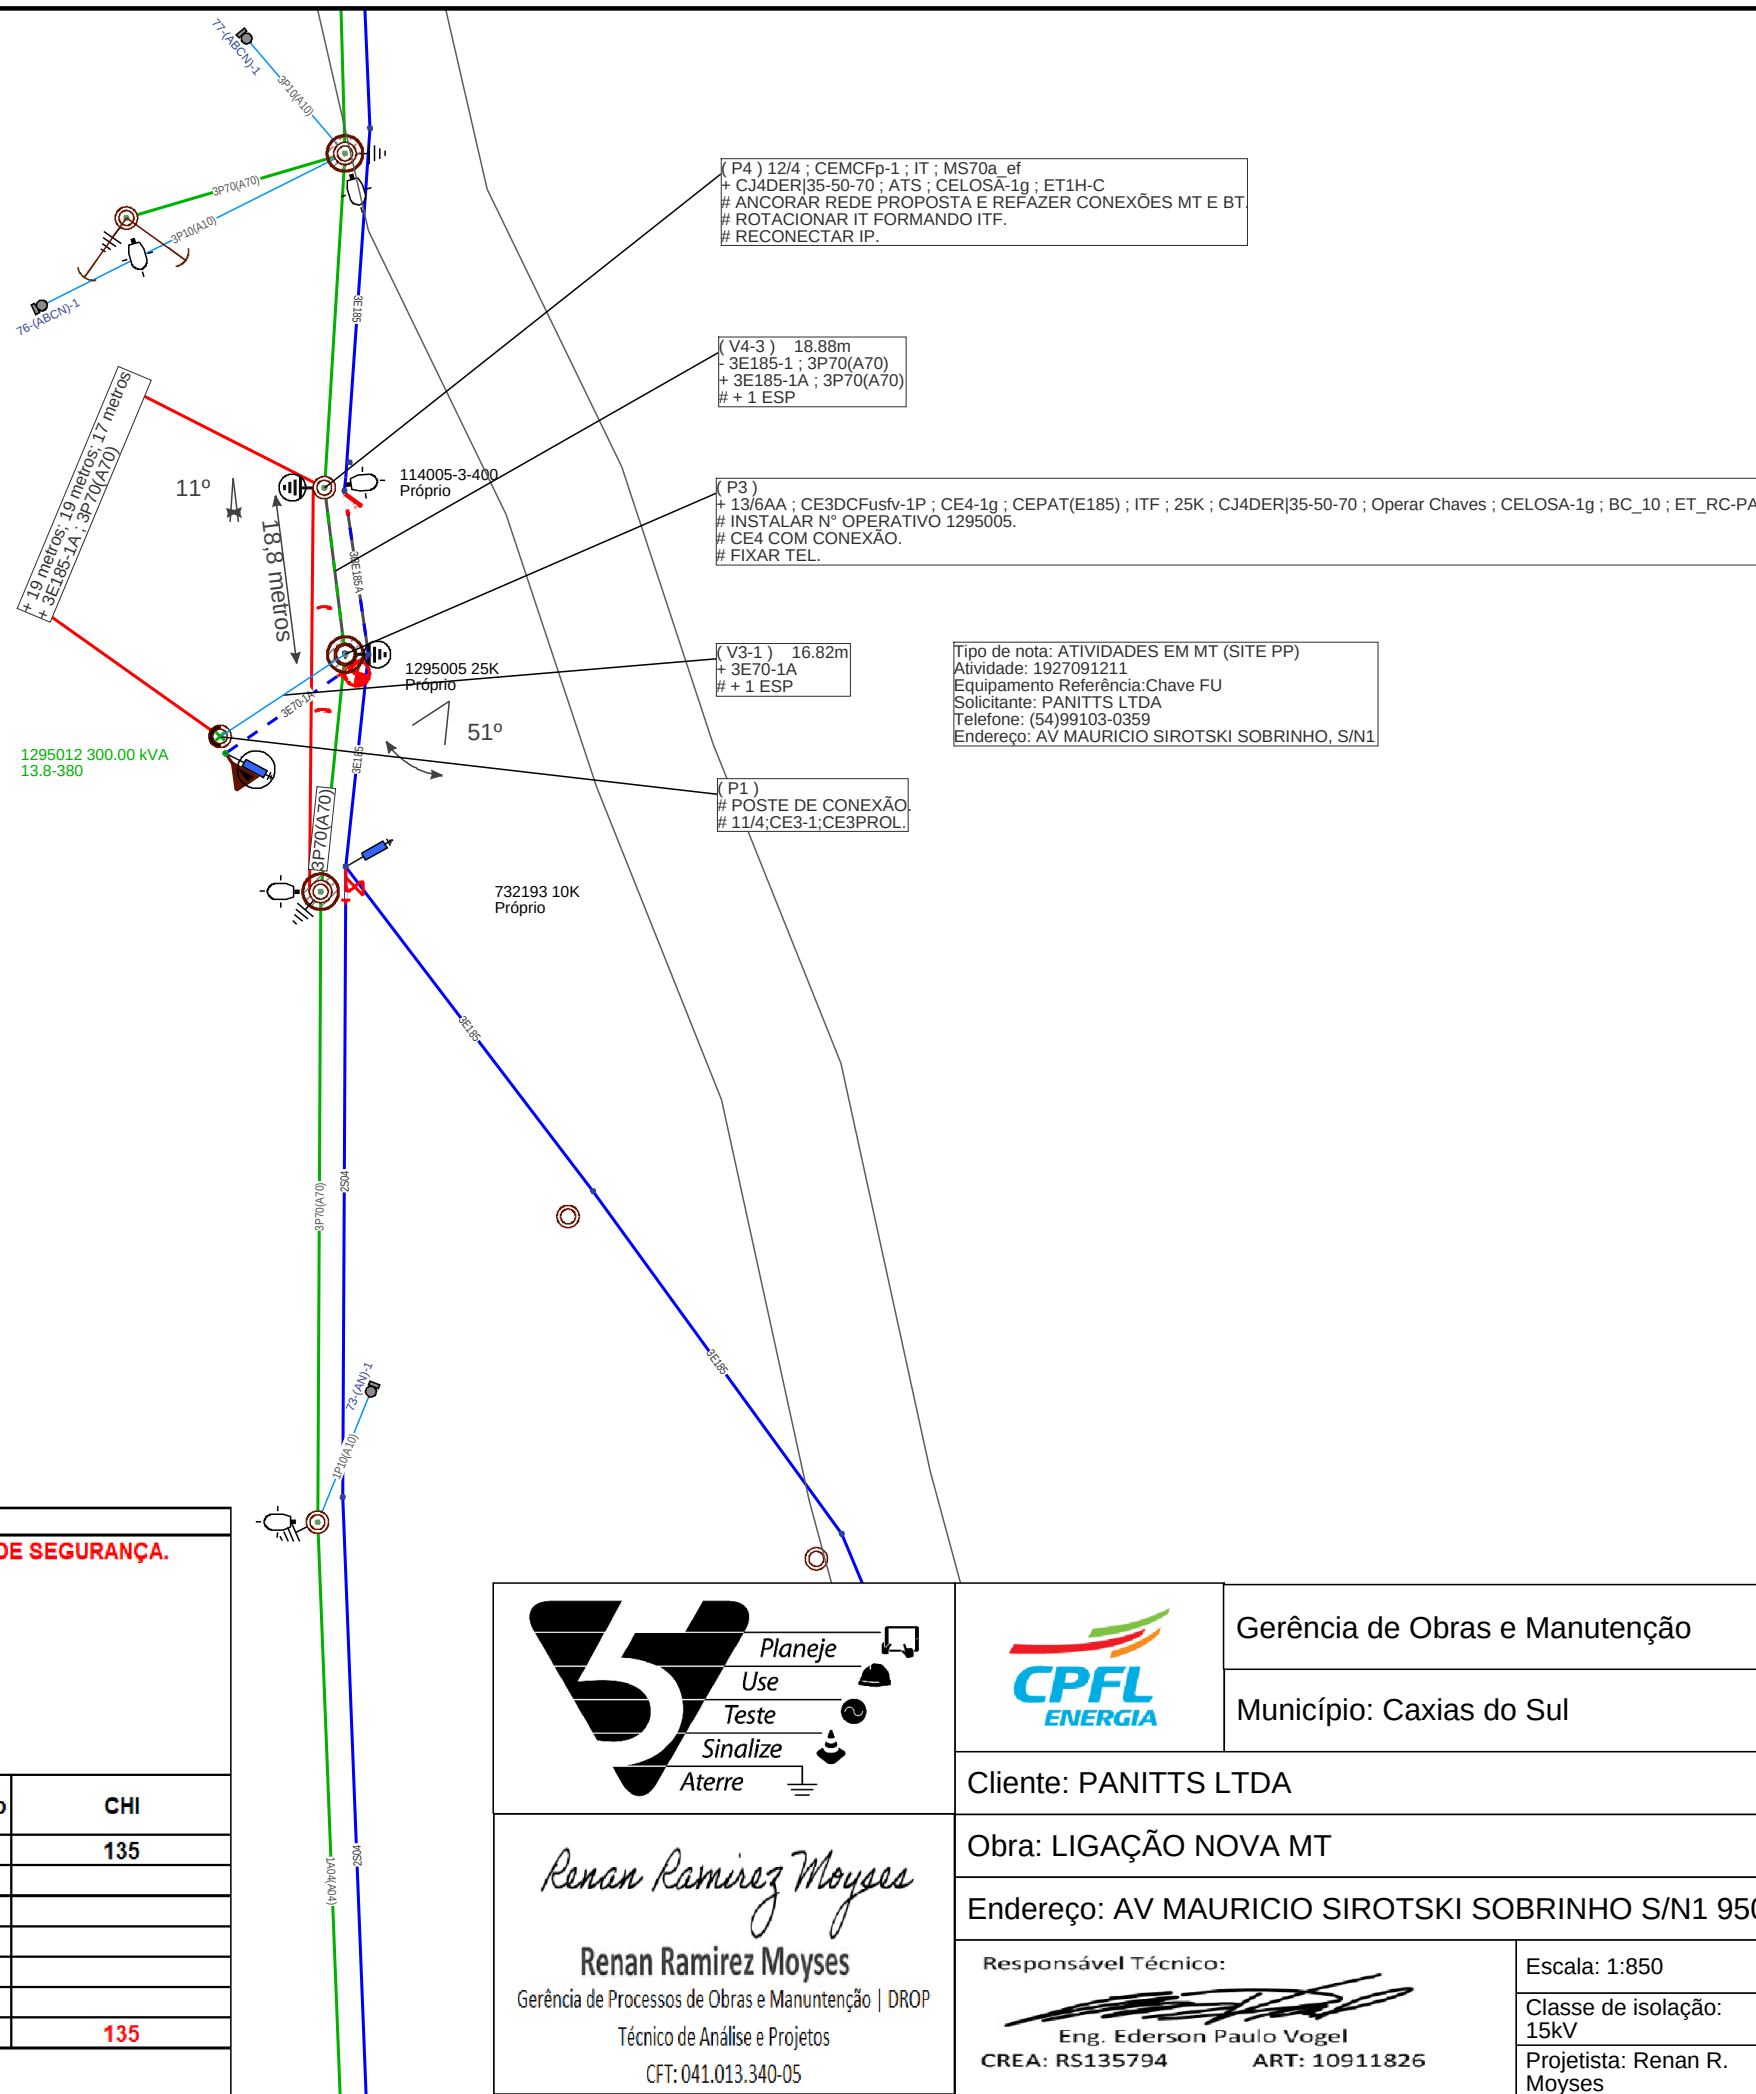


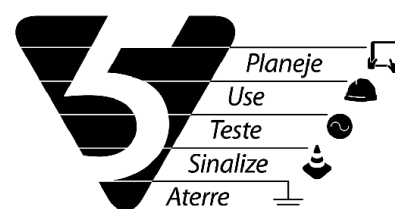

SEGURANÇA É VIDA.

Abrir Chave Faca ("NF") 298411
Abrir Chaves do Religador ("NF") 603840
Manobrar pela Chave Faca ("NA") 973151
Realizar obra conforme croqui.

Ação	Equipamento	Número	Cientes	Duração	CHI
Abrir	Chave Faca	298411	27	5	135
Abrir	Religador	603840			
Fechar	Chave Faca	973151			
Linha Viva?		Não	CHI TOTAL		135

☐ Poste novo a ser instalado (quando indicado em planta)

Renan Ramirez Moyses
Renan Ramirez Moyses
 Gerência de Processos de Obras e Manutenção | DRO
 Técnico de Análise e Projetos
 CFT: 041.013.340-05



Gerência de Obras e Manutenção

Município: Caxias do Sul

Cliente: PANITTS LTDA

Obra: LIGAÇÃO NOVA MT

Endereço: AV MAURICIO SIROTSKI SOBRINHO S/N1 95088-600 CAXIAS DO SUL BR RS

Responsável Técnico:

Eng. Ederson Paulo Vogel
CREA: RS135794 ART: 10911826

Escala: 1:850

Classe de isolamento:	15kV
Projetista:	Renan R. Moyses

	Data: 12/11/2025
--	------------------

AL: CXG25

DocId: 30000309050005

Nota:	300001093311
-------	--------------

	Folha 1
--	---------

Levantador: Marcio Bedin
