



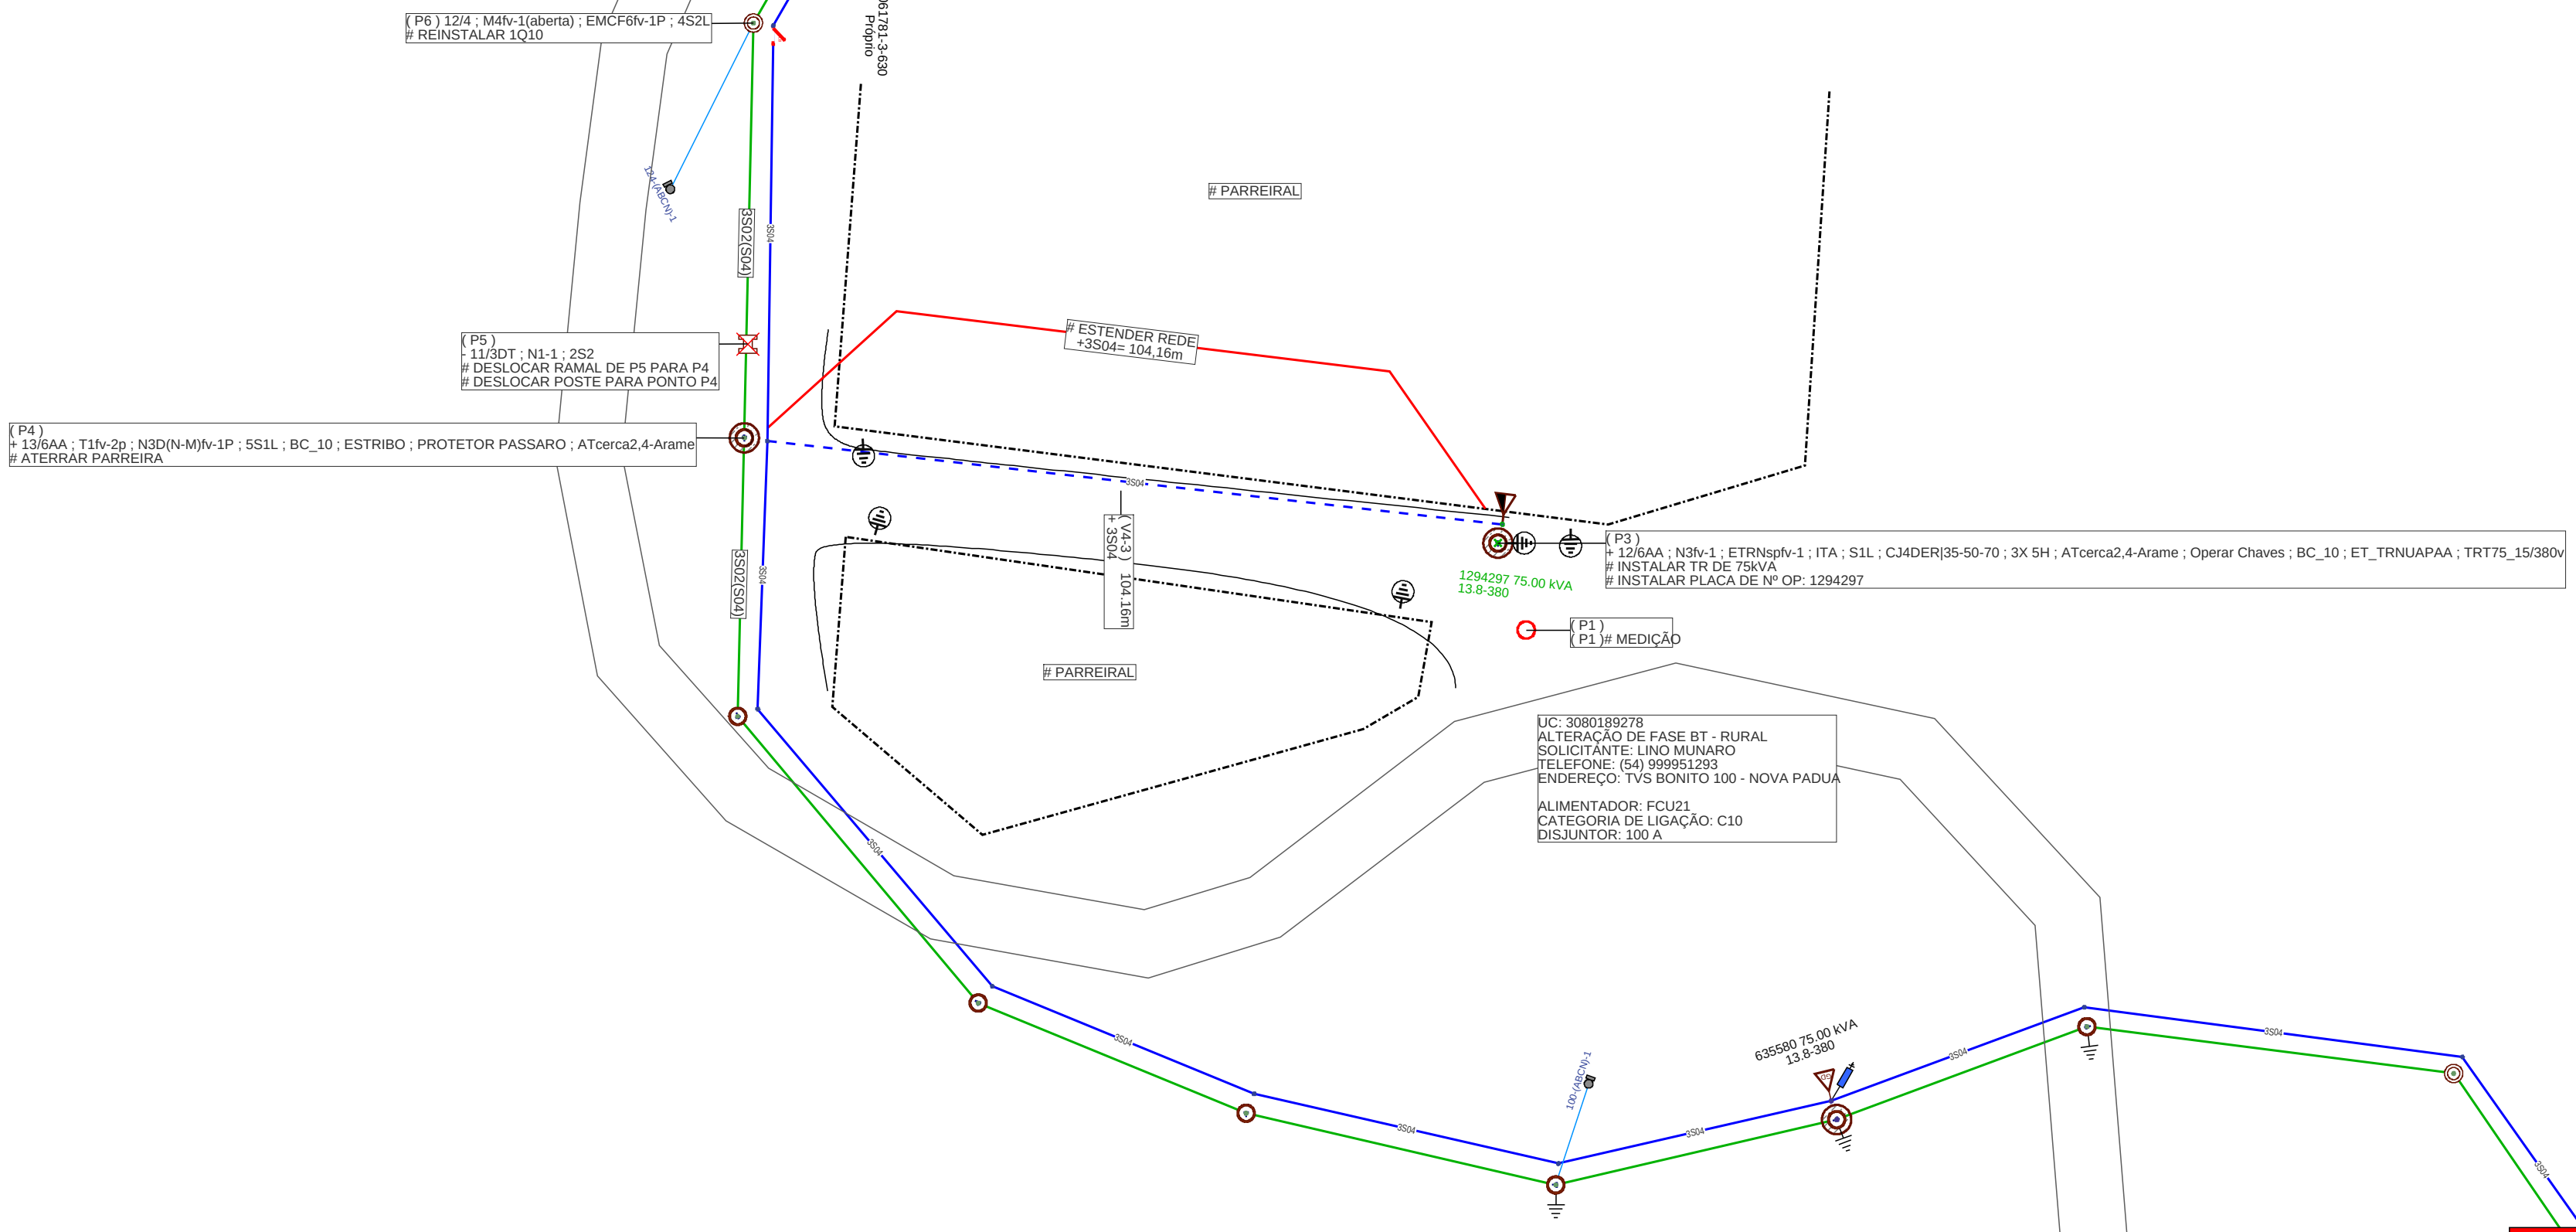

Funcionário inteligente,
previne o acidente!

PLANO DE EXECUÇÃO					
Executar a obra seguindo todos os passos de segurança!					
Manobrar equipamentos abaixo para realizar a obra. Operar com linha viva na MT					
Ação	Equipamento	Número	Cientes	Duração	CHI
Desligar	Transformador	635580	4	5	20
Linha Viva?		Sim	CHI TOTAL		20
☐ Poste novo a ser instalado (quando indicado em planta)					

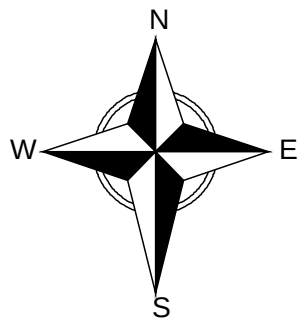

FeedBack Para Fábrica de Projetos

Planeje
Use
Teste
Sinalize
Aterre

Wellerson Avila
Wellerson Amaral Avila
Gerência de Processos de Obras e Manutenção | DROP
Técnico de Análise e Projetos
CFT: 04993185014

Gerência de Obras e Manutenção

Município: Nova Pádua

Cliente: LINO MUNARO

Obra: ALTERAÇÃO DE FASE BT - RURAL

Endereço: TVS BONITO 100 95275-000 NOVA PADUA BR RS

Responsável Técnico: Eng. Ederson Paulo Vogel CREA: RS135794 ART: 10911826	Escala: 1:800 Classe de isolamento: 15kV Projetista: Wellerson Avila	Data: 05/11/2025 AL: FCU21 Projeto: 000007915985	Nota: 300001093798 Folha 1 Levantador Marcio Bedin
---	--	--	--