



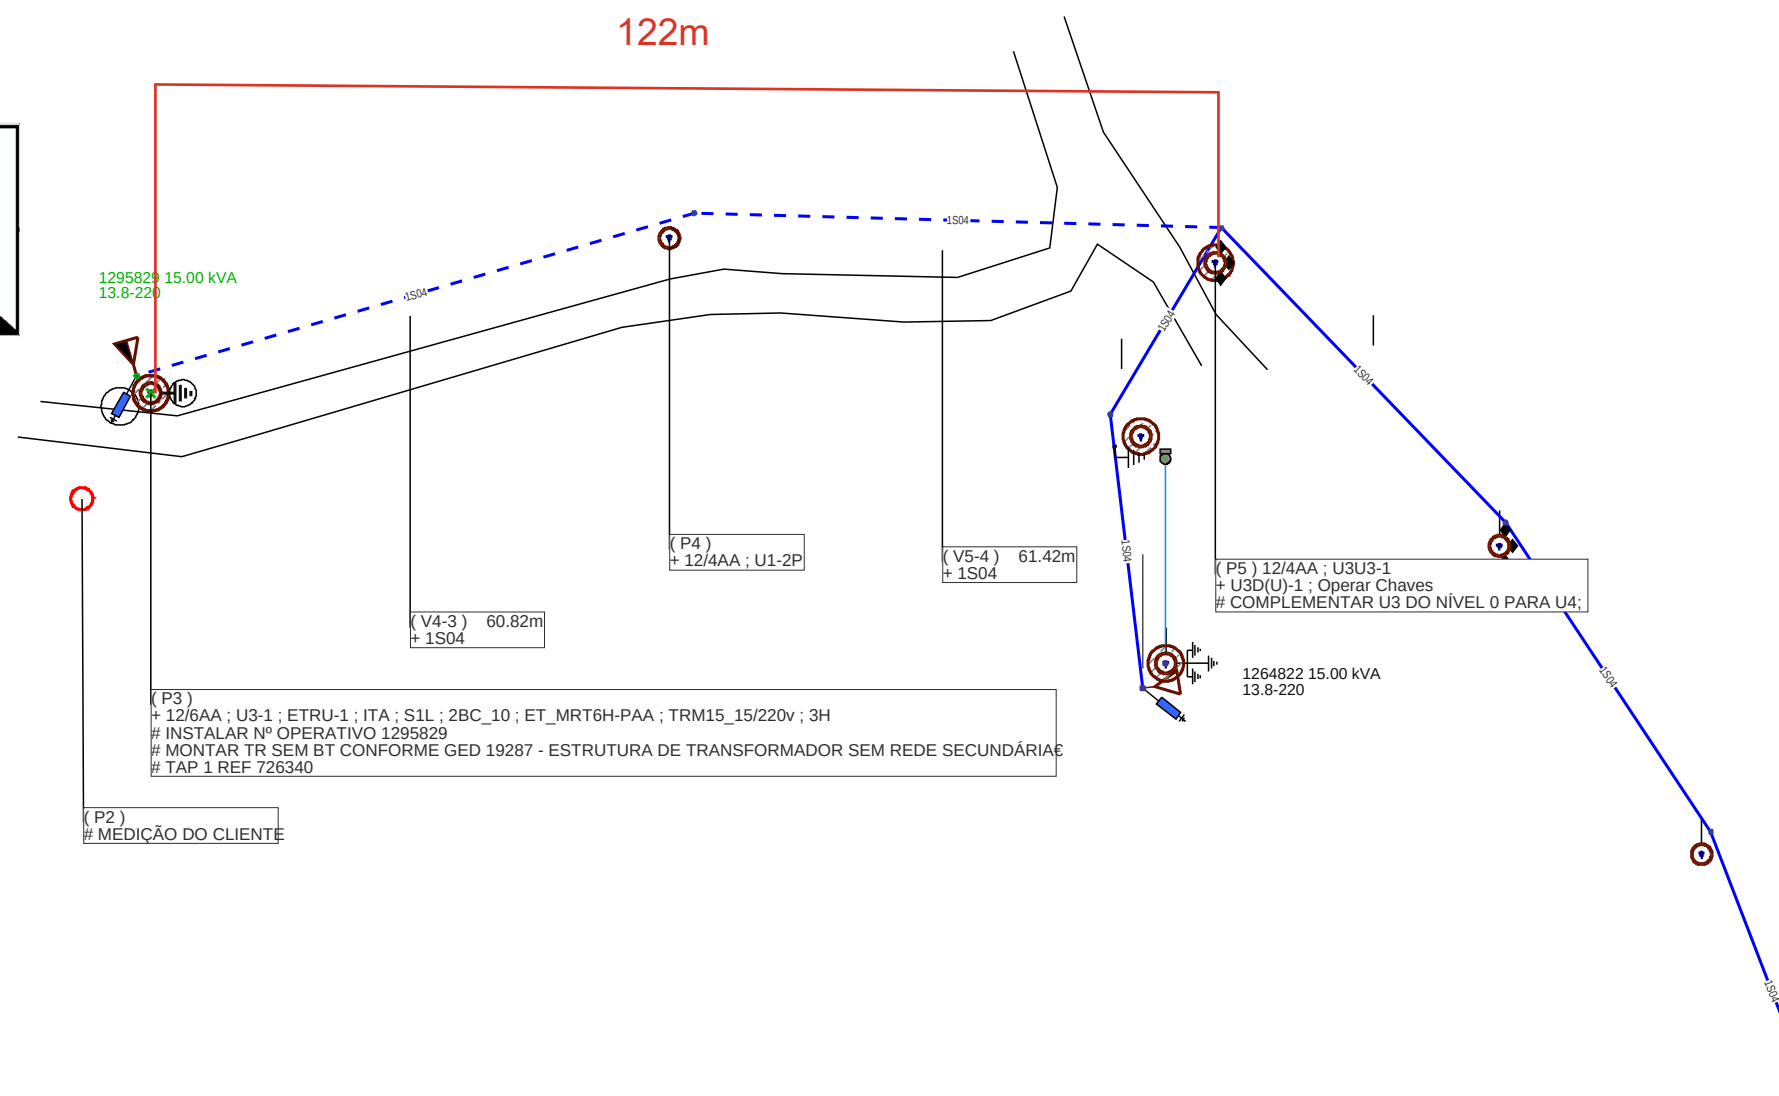

LIGACÃO NOVA BT - RURAL

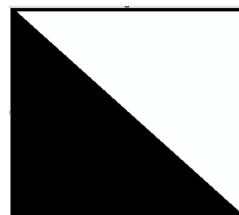


**O elo mais importante
é você!**

PLANO DE EXECUÇÃO					
# INSTALAR TR DE 75kVA NO P2					
# ESTENDER 122m DE REDE DE MT 1S04 DE					
# INSTALAR 2 POSTES					
Executar as atividades com segurança repetindo normas e orientações, Não alterar o projeto sem solicitar ao projetista.					
Ação	Equipamento	Número	Clientes	Duração	CHI
Abrir	Chave Fusível	1219873	12	5	60
Linha Viva?		Sim	CHI TOTAL		60
☐ Poste novo a ser instalado (quando indicado em planta)					



FeedBack Para Fábrica de Projetos

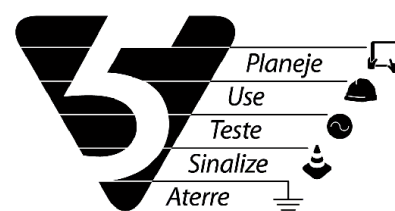

jeremias duarte

CFT: 04326448067



Eng. Ederson Paulo Vogel
CREA: RS135794 ART: 10911826

Levantador: Marcio Bedin
