


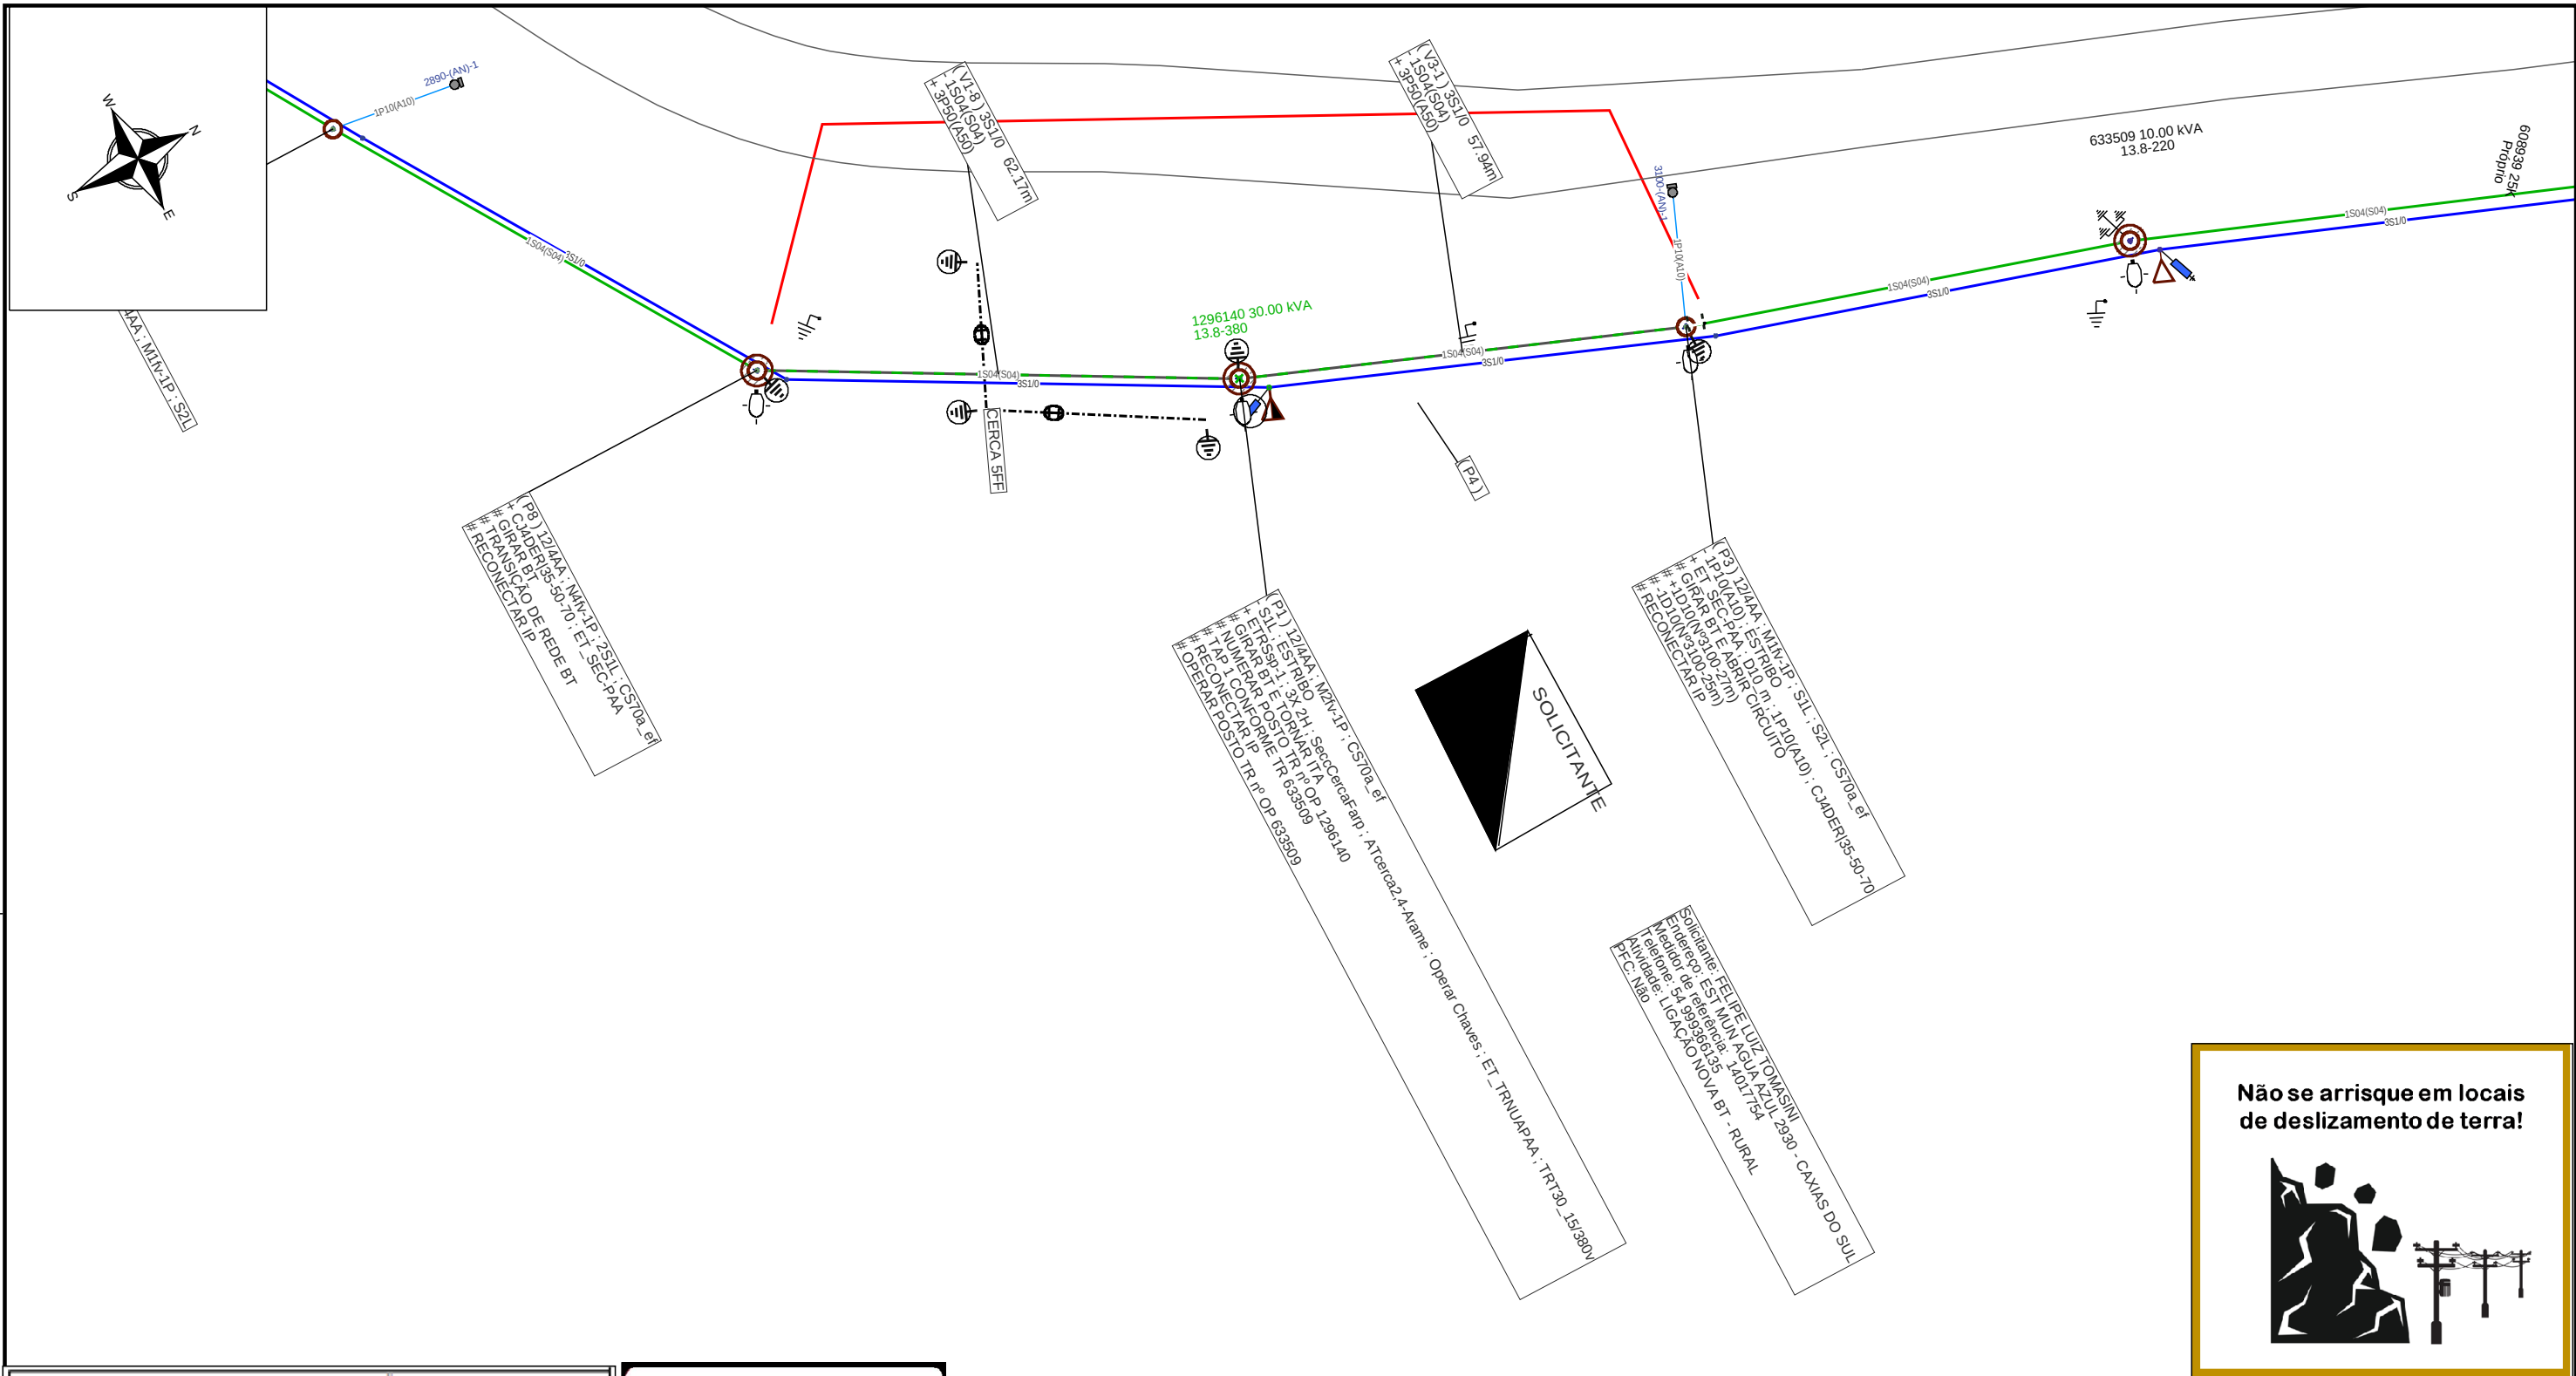

Não se arrisque em locais de deslizamento de terra!

PLANO DE EXECUÇÃO					
Executar a obra seguindo todos os passos de segurança!					
Utilizar equipe de LV e executar os pontos P1					
Abrir o equipamento indicado ABAIXO e executar a obra em LM					
Executar atividades de acordo com o projeto.					
Ação	Equipamento	Número	Clientes	Duração	CHI
Abrir	Transformador	633509	2	4	8
Linha Viva?		Não	CHI TOTAL		8
☐ Poste novo a ser instalado (quando indicado em planta)					

FeedBack Para Fábrica de Projetos

Planeje
Use
Teste
Sinalize
Aterre

Felipe Gaspari Souza
Felipe Gaspari Souza
Gerência de Processos de Obras e Manutenção | DROP
Técnico de Análise e Projetos
CFT: 028.654.060-67

Gerência de Obras e Manutenção

Município: Caxias do Sul

Cliente: FELIPE LUIZ TOMASINI

Obra: LIGAÇÃO NOVA BT - RURAL

Endereço: EST MUN AGUA AZUL 2930 95130-000 CAXIAS DO SUL BR RS

Responsável Técnico:

Eng. Ederson Paulo Vogel
CREA: RS135794 ART: 10911826

Escala: 1:850

Classe de isolamento: 15kV

Projetista: FELIPE GASPARI

Data: 26/11/2025

AL: CXD22

Projeto: 000007932970

Nota: 300001098064

Folha 1

Levantador ADELAR GRAFE