


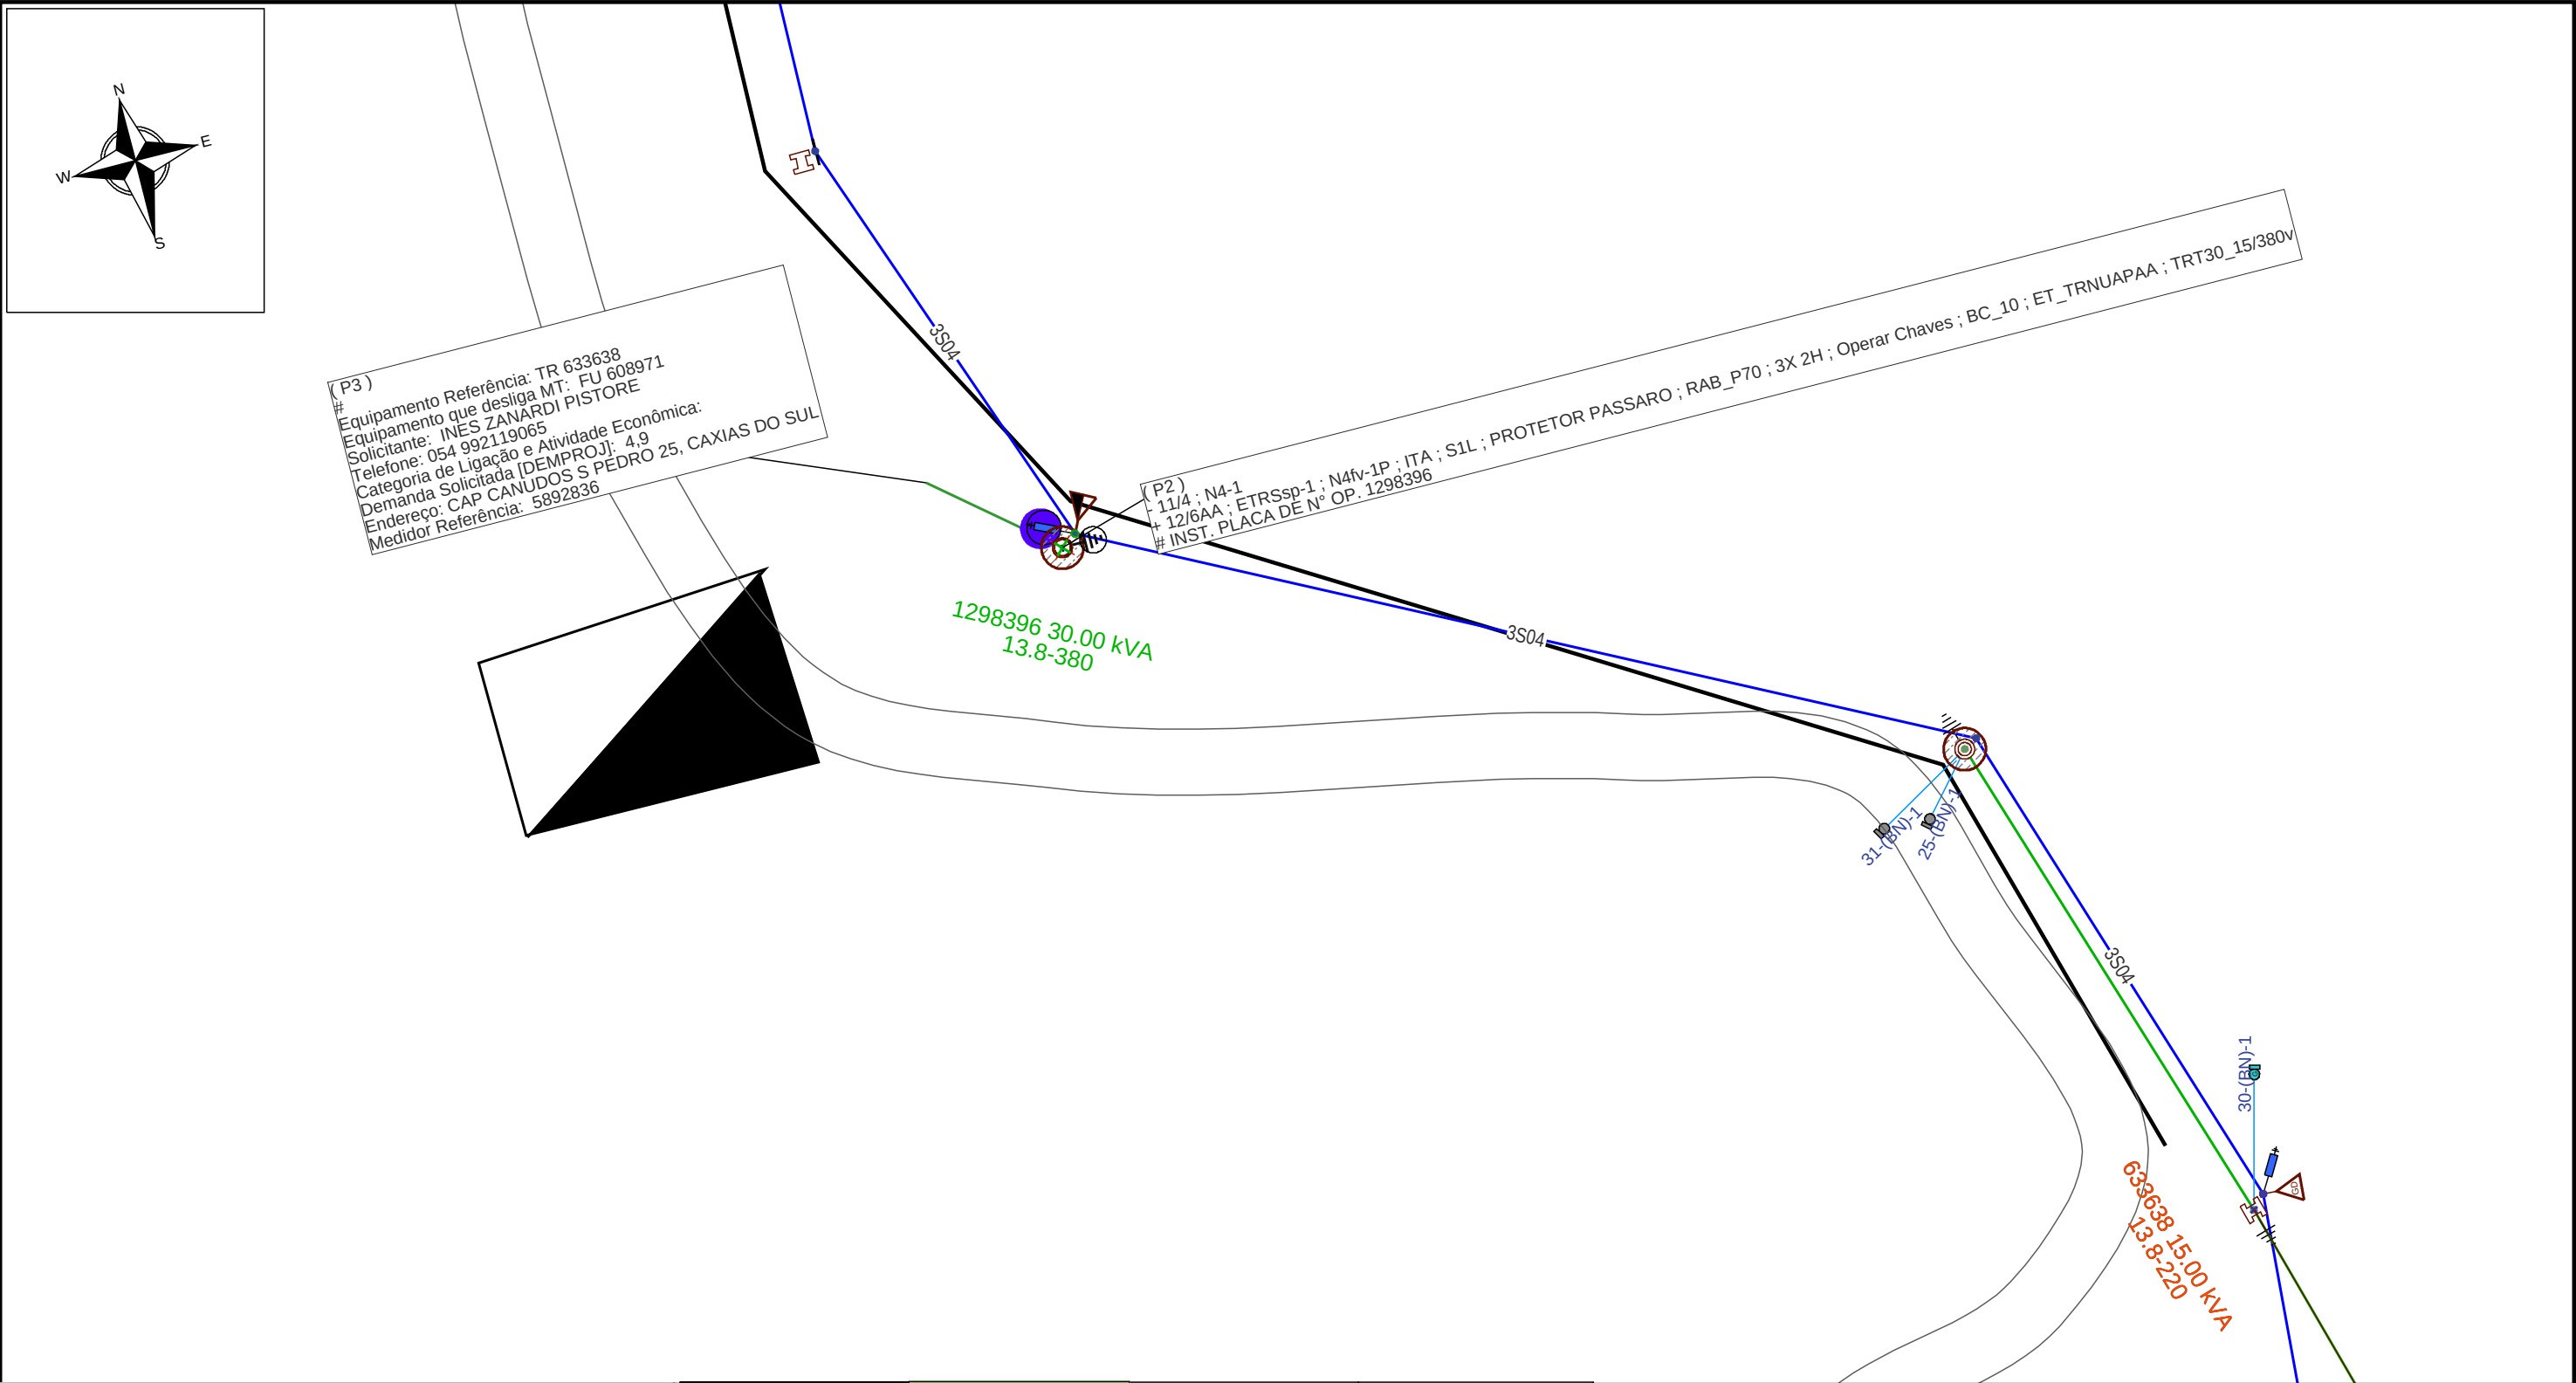

PLANO DE EXECUÇÃO Para Execução De Obra,Executar As Manobras Abaixo						RECLASSIFICAÇÃO DE POSTES OS POSTES DO TIPO TRONCO CÔNICO E FIBRA DE VIDRO CONTIDOS NOS GED'S 1347 E 14606 SEMPRE DEVERÃO SER SUBMETIDOS A AVALIAÇÃO DE RECLASSIFICAÇÃO DOS MESMOS CONFORME O GED 18968 DEVERÃO SEMPRE SER AVALIADOS 3 PARÂMETROS: # CARACTERÍSTICAS TÉCNICAS; # FISSURAS; # APARÊNCIAS. O DETALHAMENTO DE CADA PARÂMETRO DEVE SER VERIFICADO JUNTO AO GED 18968. Henrique Silva Erguy Junior Gerência de Processos de Obras e Manutenção DROP Técnico de Análise Projetos I CFT: 5287547404-9 FeedBack Para Fábrica de Projetos		Seja a mudança que você quer ver na segurança do trabalho. Planeje Use Teste Sinalize Aterre		Gerência de Obras e Manutenção Município: Caxias do Sul	
<table><tr><th>Ação</th><th>Equipamento</th><th>Número</th><th>Clientes</th><th>Duração</th><th>CHI</th></tr><tr><td>Abrir</td><td>Chave Fusível</td><td>608971</td><td>76</td><td>6</td><td>456</td></tr><tr><td></td><td></td><td></td><td></td><td></td><td>0</td></tr><tr><td></td><td></td><td></td><td></td><td></td><td>0</td></tr><tr><td></td><td></td><td></td><td></td><td></td><td>0</td></tr><tr><td></td><td></td><td></td><td></td><td></td><td>0</td></tr><tr><td></td><td></td><td></td><td></td><td></td><td>0</td></tr><tr><td colspan="2">Linha Viva?</td><td>Não</td><td colspan="2">CHI TOTAL</td><td>456</td></tr></table> Poste novo a ser instalado (quando indicado em planta)						Ação	Equipamento	Número	Clientes	Duração	CHI	Abrir	Chave Fusível	608971	76	6	456						0						0						0						0						0	Linha Viva?		Não	CHI TOTAL		456	Cliente: INES ZANARDI PISTORE					
Ação	Equipamento	Número	Clientes	Duração	CHI	
Abrir	Chave Fusível	608971	76	6	456	
					0	
					0	
					0	
					0	
					0	
Linha Viva?		Não	CHI TOTAL		456	
Obra: ALTERAÇÃO DE FASE BT - RURAL	
Endereço: CAP CANUDOS S PEDRO 25 95130-000 CAXIAS DO SUL BR RS	
Responsável Técnico: Eng. Ederson Paulo Vogel CREA: RS135794 ART: 10911826			Escala: 1:1000	Data: 01/12/2025	Nota: 300001099704	
			Classe de isolamento: 15KV	AL: CXD22	Folha 1	
			Projetista: HENRIQUE ERGUY	Projeto: 000007935811	Levantador REINHOLDO	