


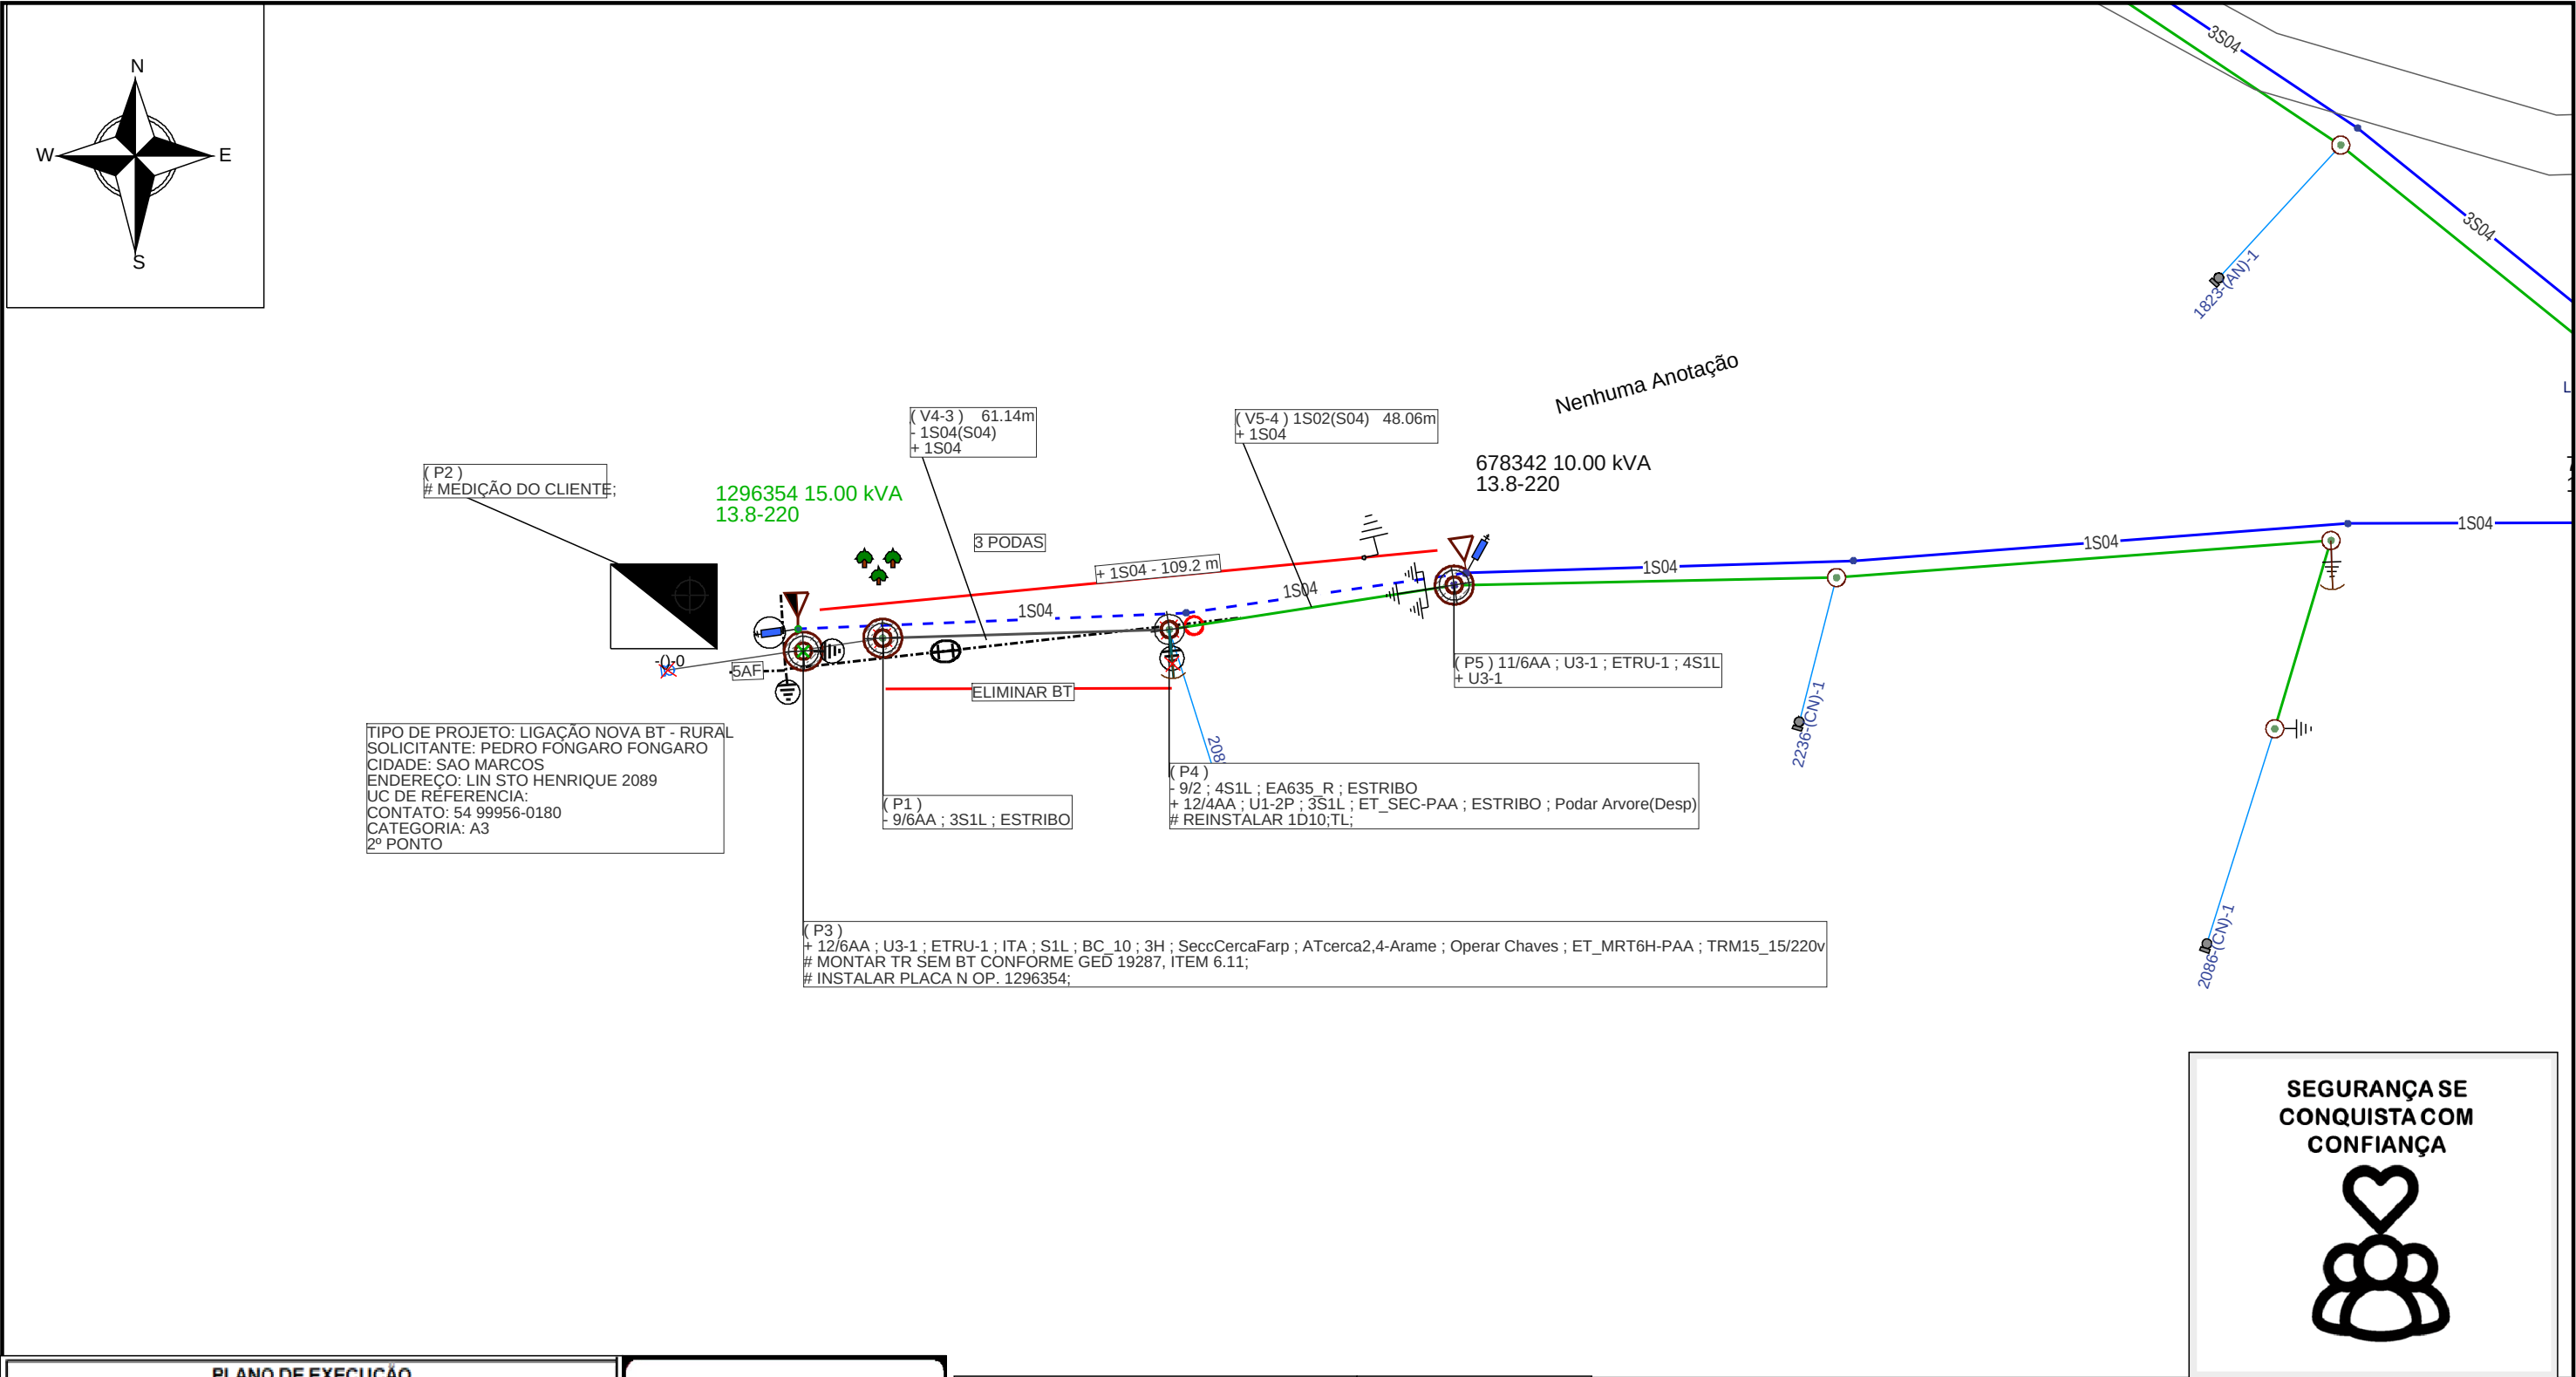

SEGURANÇA SE
CONQUISTA COM
CONFIANÇA

PLANO DE EXECUÇÃO					
Executar a obra seguindo todos os passos de segurança!					
Estender rede MT e instalar TR de 15 KV.					
Ação	Equipamento	Número	Clientes	Duração	CHI
Abrir	Chave Fusivel	622431	3	5	15
Linha Viva?		Não	CHI TOTAL		15
☐ Poste novo a ser instalado (quando indicado em planta)					

FeedBack Para Fábrica de Projetos

Planeje
Use
Teste
Sinalize
Aterre

Valesca S. Mendes

Gerência de Processos de Obras e Manutenção | DROP

Técnico de Análise e Projetos

CFT: 005.174.320-56

Gerência de Obras e Manutenção

Município: São Marcos

Cliente: PEDRO FONGARO FONGARO

Obra: LIGAÇÃO NOVA BT - RURAL

Endereço: LIN STO HENRIQUE 2089 95190-000 SAO MARCOS BR RS

Responsável Técnico:

Eng. Ederson Paulo Vogel
CREA: RS135794 ART: 10911826

Escala: 1:1100

Classe de isolamento:
15kV

Projetista: VALESCA
MENDES

Data:06/12/2025

AL: SMC14

Projeto: 000007936847

Nota:
300001100053

Folha 1

Levantador RICARDO
QUEVEDO