
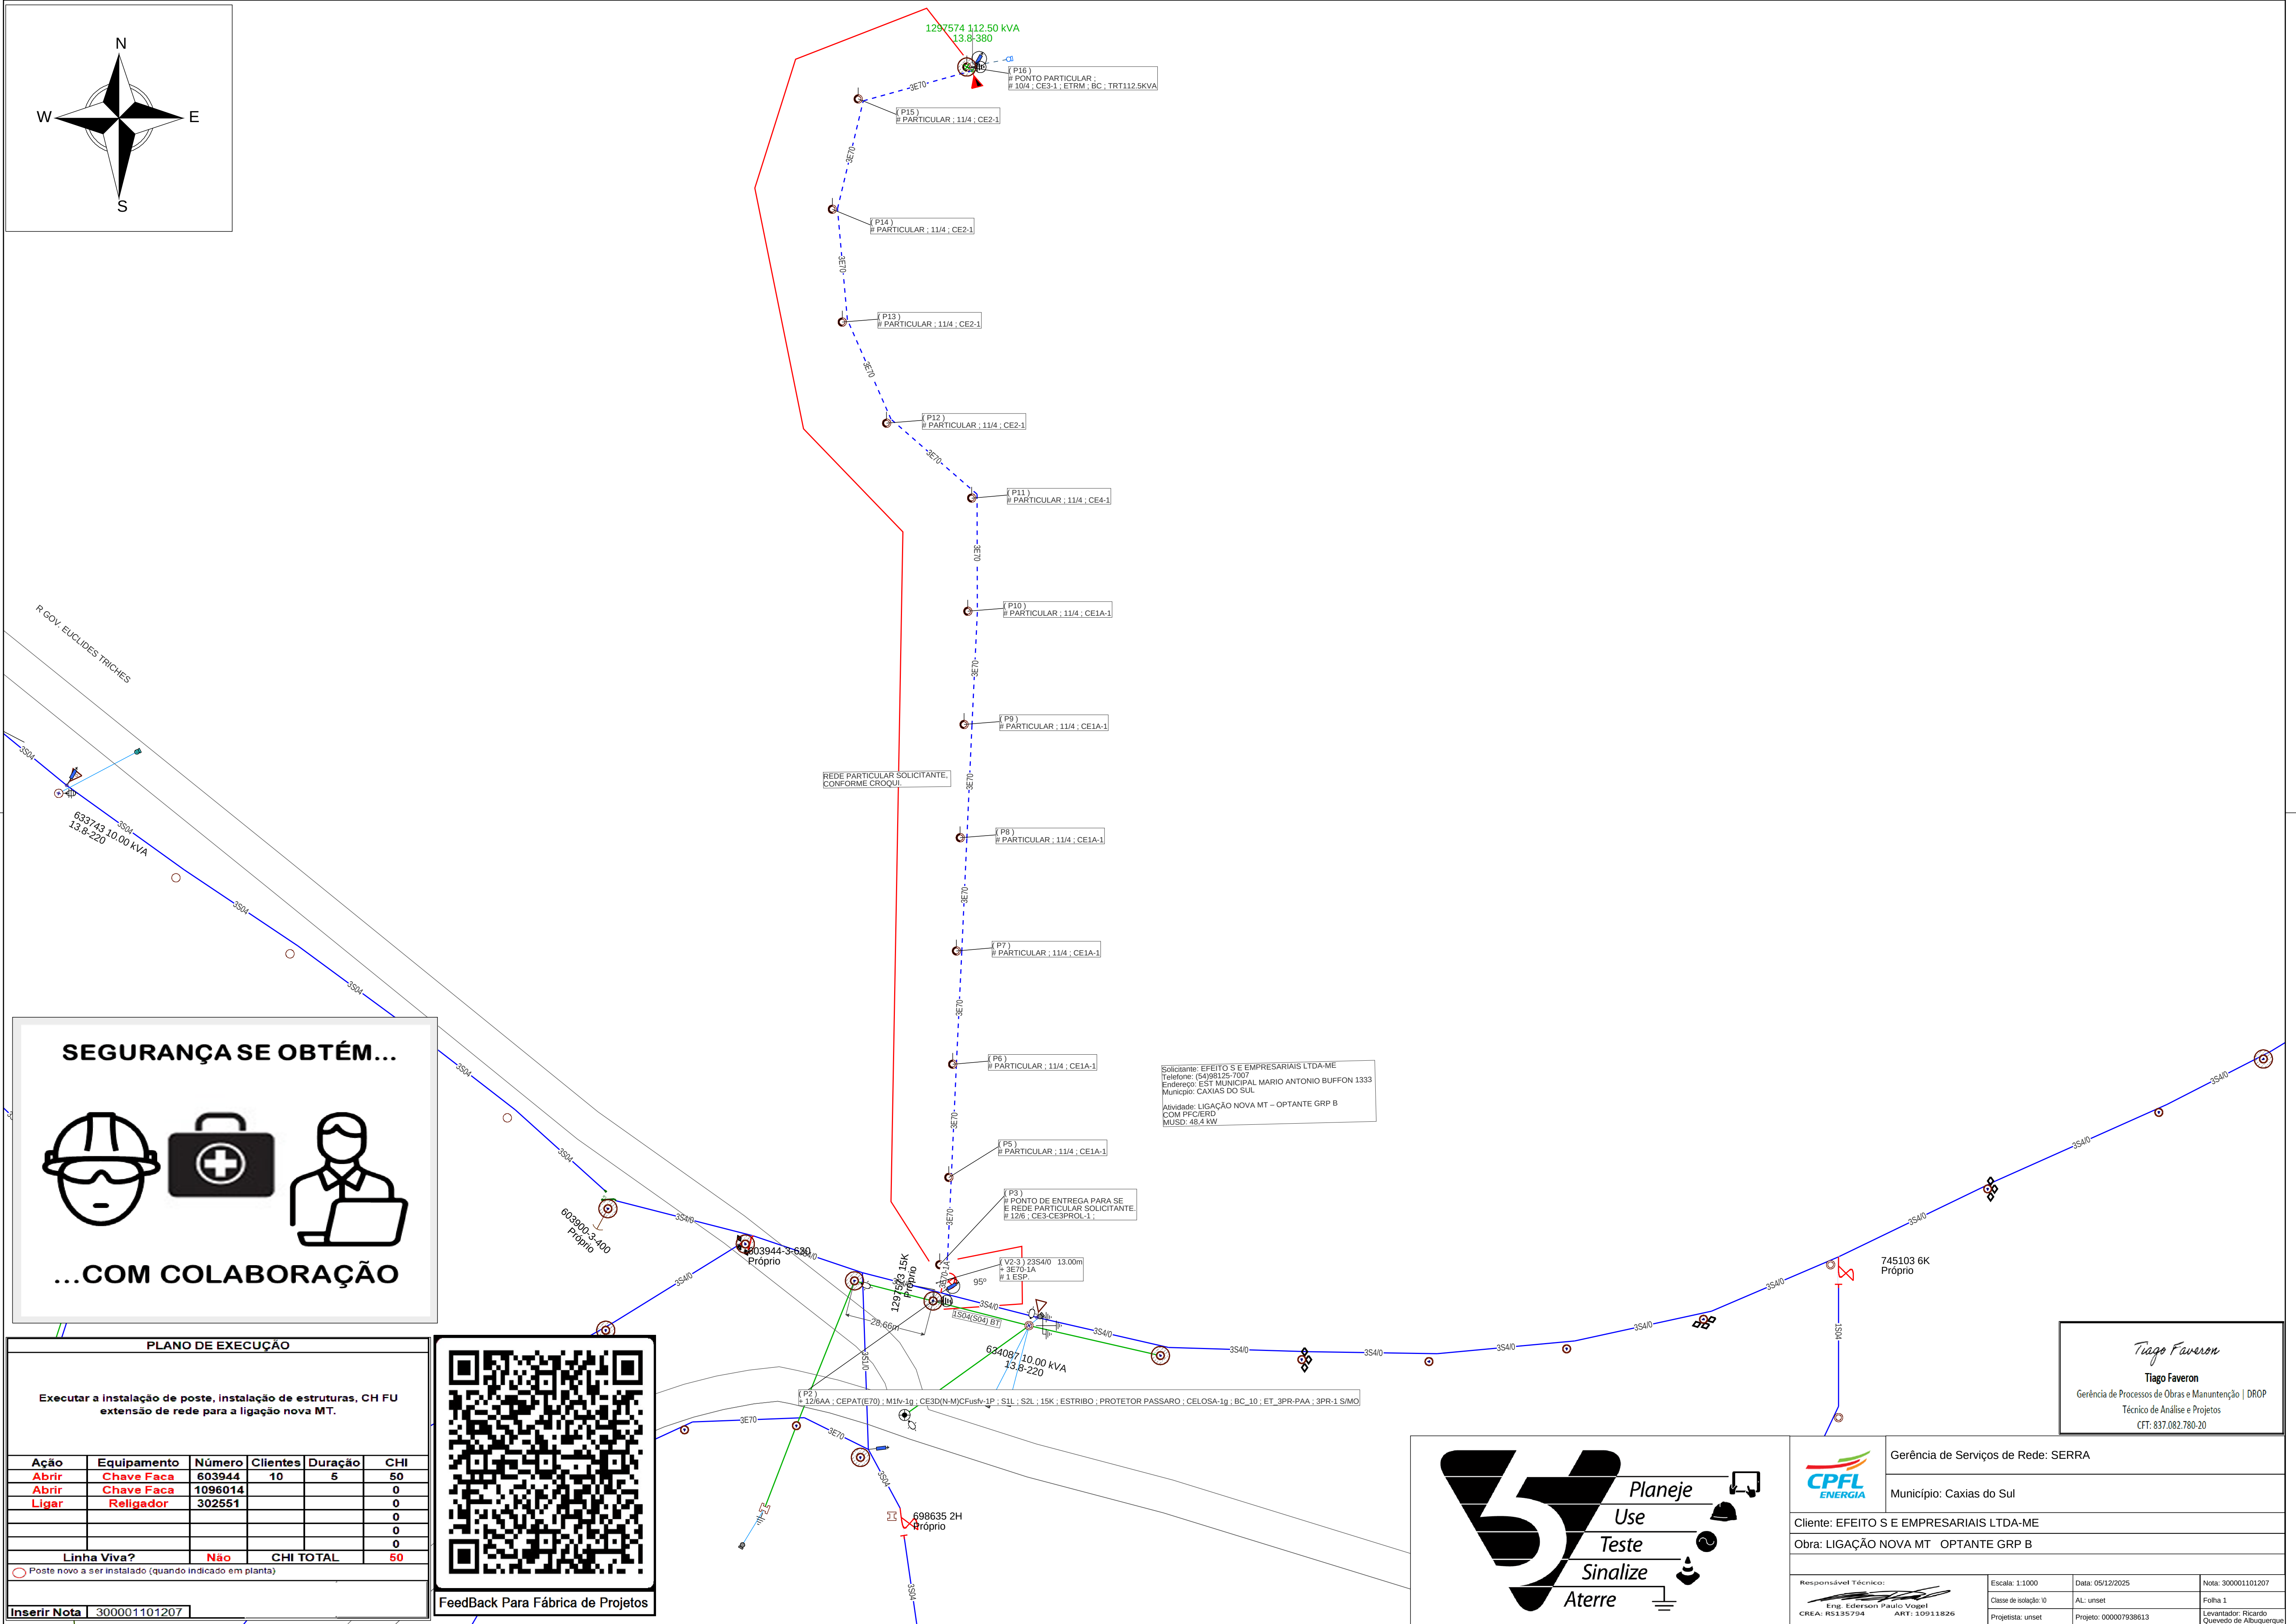


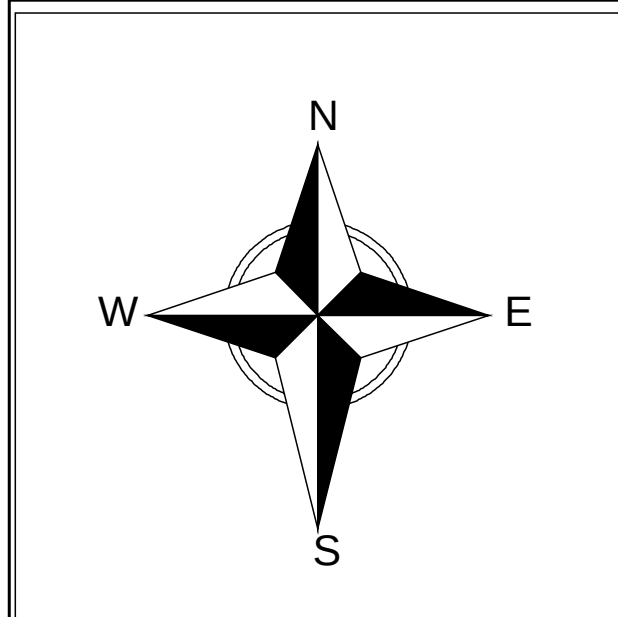

SEGURANÇA SE OBTÉM...

...COM COLABORAÇÃO

PLANO DE EXECUÇÃO					
Executar a Instalação de poste, instalação de estruturas, CH FU extensão de rede para a ligação nova MT.					
Ação	Equipamento	Número	Cientes	Duração	CHI
Abrir	Chave Faca	603944	10	5	50
Abrir	Chave Faca	1096014			0
Ligar	Religador	302551			0
					0
					0
					0
Linha Viva?		Não	CHI TOTAL		50
☐ Poste novo a ser instalado (quando indicado em planta)					
Inserir Nota		300001101207			

FeedBack Para Fábrica de Projetos

Planeje

Use

Teste

Sinalize

Aterre

Gerência de Serviços de Rede: SERRA

Município: Caxias do Sul

Cliente: EFEITO S E EMPRESARIAIS LTDA-ME

Obra: LIGAÇÃO NOVA MT - OPTANTE GRP B

Responsável Técnico:
Eng. Ederson Paulo Vogel
CREA: RS135794

Escala: 1:1000
Classe de Isolção: 10
Projeto: unset

Data: 05/12/2025
AL: unset
Projeto: 000007938613

Nota: 300001101207
Folha 1
Levantador: Ricardo Quevedo de Albuquerque