


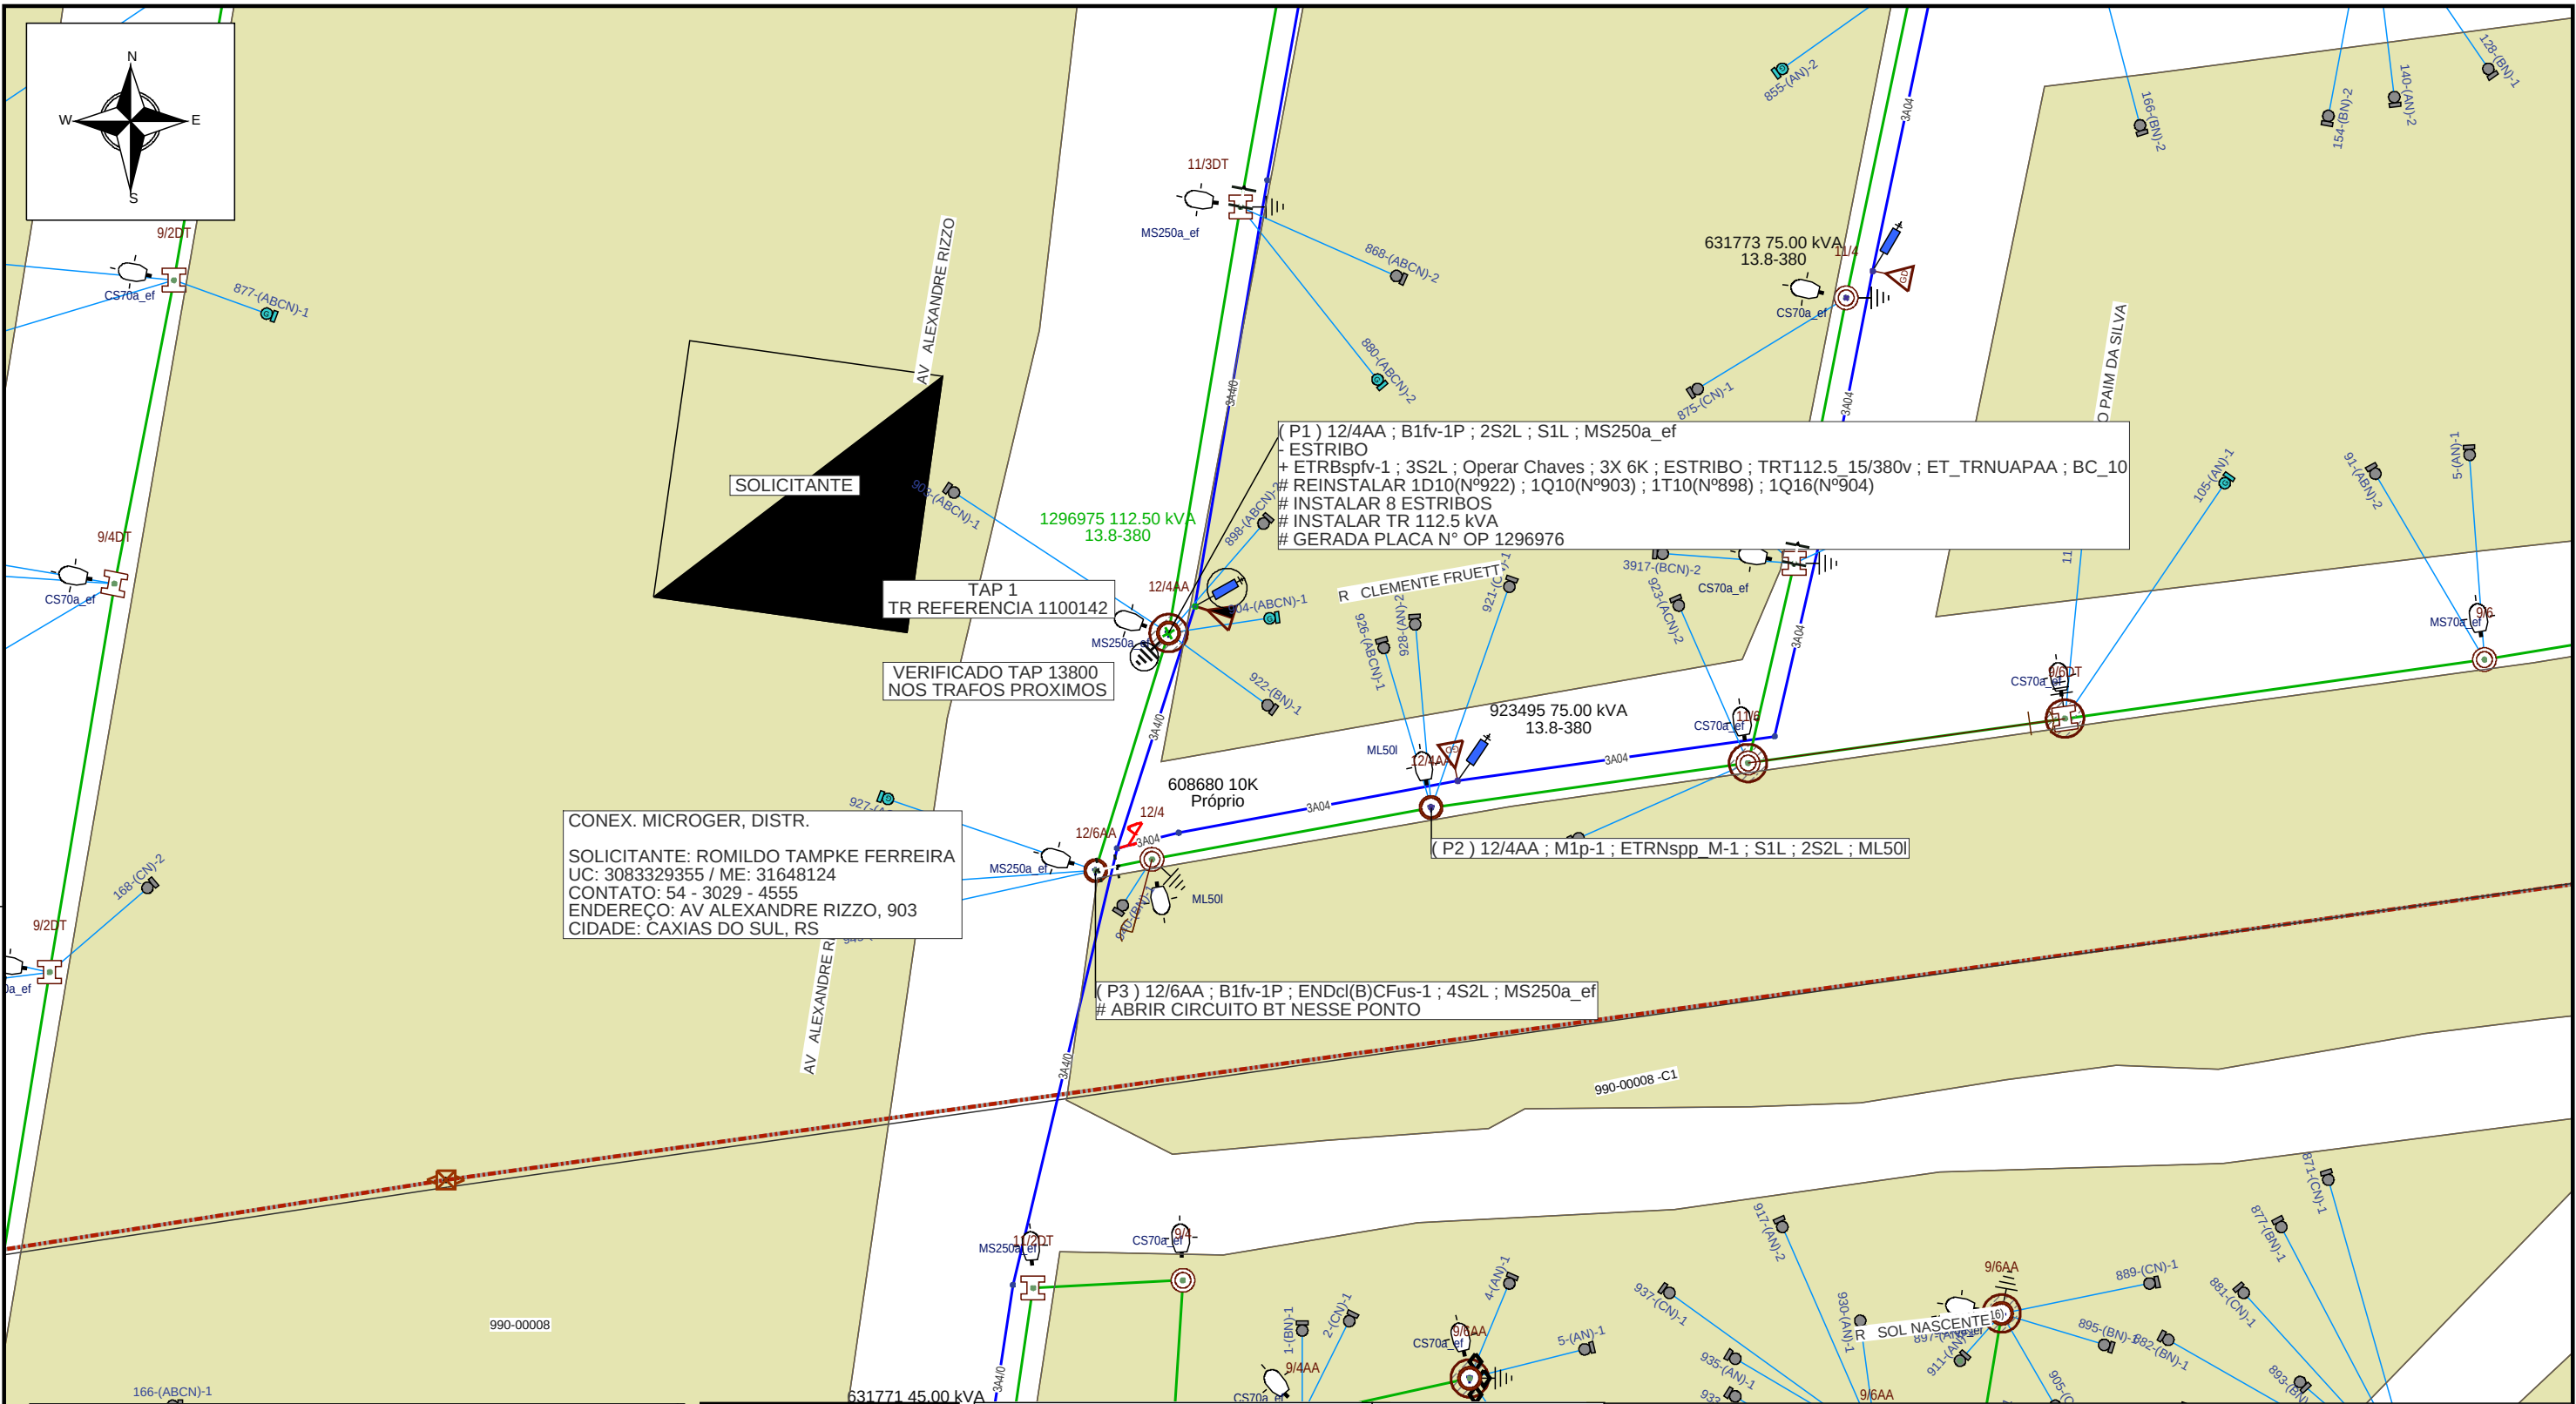

CONEX. MICROGER, DISTR.
SOLICITANTE: ROMILDO TAMPKE FERREIRA
UC: 3083329355 / ME: 31648124
CONTATO: 54 - 3029 - 4555
ENDEREÇO: AV ALEXANDRE RIZZO, 903
CIDADE: CAXIAS DO SUL, RS

(P1) 12/4AA ; B1fv-1P ; 2S2L ; S1L ; MS250a_ef
- ESTRIBO
+ ETRBspfv-1 ; 3S2L ; Operar Chaves ; 3X 6K ; ESTRIBO ; TRT112.5_15/380v ; ET_TRNUAPAA ; BC_10
REINSTALAR 1D10(Nº922) ; 1Q10(Nº903) ; 1T10(Nº898) ; 1Q16(Nº904)
INSTALAR 8 ESTRIBOS
INSTALAR TR 112.5 kVA
GERADA PLACA Nº OP 1296976

(P2) 12/4AA ; M1p-1 ; ETRNspp_M-1 ; S1L ; 2S2L ; ML50I

(P3) 12/6AA ; B1fv-1P ; ENDcl(B)CFus-1 ; 4S2L ; MS250a_ef
ABRIR CIRCUITO BT NESSE PONTO

PLANO DE EXECUÇÃO

Executar atividades com segurança, respeitando normas e orientações
Abrir cavas e preparar as obras; MO da manobra paga no P1
Instalar com LV no P1, TR 1296975 de 112.5 kVA; Abrir circuito BT em P3
Instalar e atualizar placas de número operativo, conforme projeto
Recolher resíduos após o término das obras

Qualquer alteração, solicitar via Desing I

Ação	Equipamento	Número	Clientes	Duração	CHI
Abrir	Transformador	923495	38	5	190
					0
					0
					0
					0
					0
Linha Viva?		Sim	CHI TOTAL		190

Poste novo a ser instalado (quando indicado em planta)




FeedBack Para Fábrica de Projetos

SEGURANÇA SE OBTÉM...



...COM COLABORAÇÃO

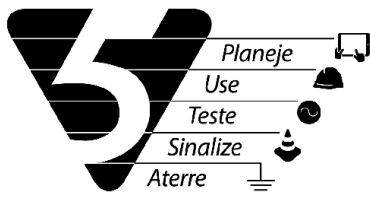

Diego Souza Ribeiro

DIEGO SOUZA RIBEIRO

Gerência de Processos de Obras e Manutenção | DROP

Técnico de Análise e Projetos

CFT: 021.824.880-65



Gerência de Obras e Manutenção

Município: CAXIAS DO SUL

Cliente: ROMILDO TAMPKE FERREIRA

Obra: CONEXÃO MICROGERADOR DISTRIBUIDA

Endereço: AV ALEXANDRE RIZZO 903 95110-000 CAXIAS DO SUL BR RS

Responsável Técnico:

Eng. Ederson Paulo Vogel
CREA: RS135794 ART: 10911826

Escala: 1:700

Classe de isolamento:
15kV

Projetista: DIEGO
RIBEIRO

Data: 04/12/2025

AL: CXH44

Projeto: 000007937437

Nota:
300001101423

Folha 1

Levantador: RICARDO
Q. DE ALBUQUERQUE