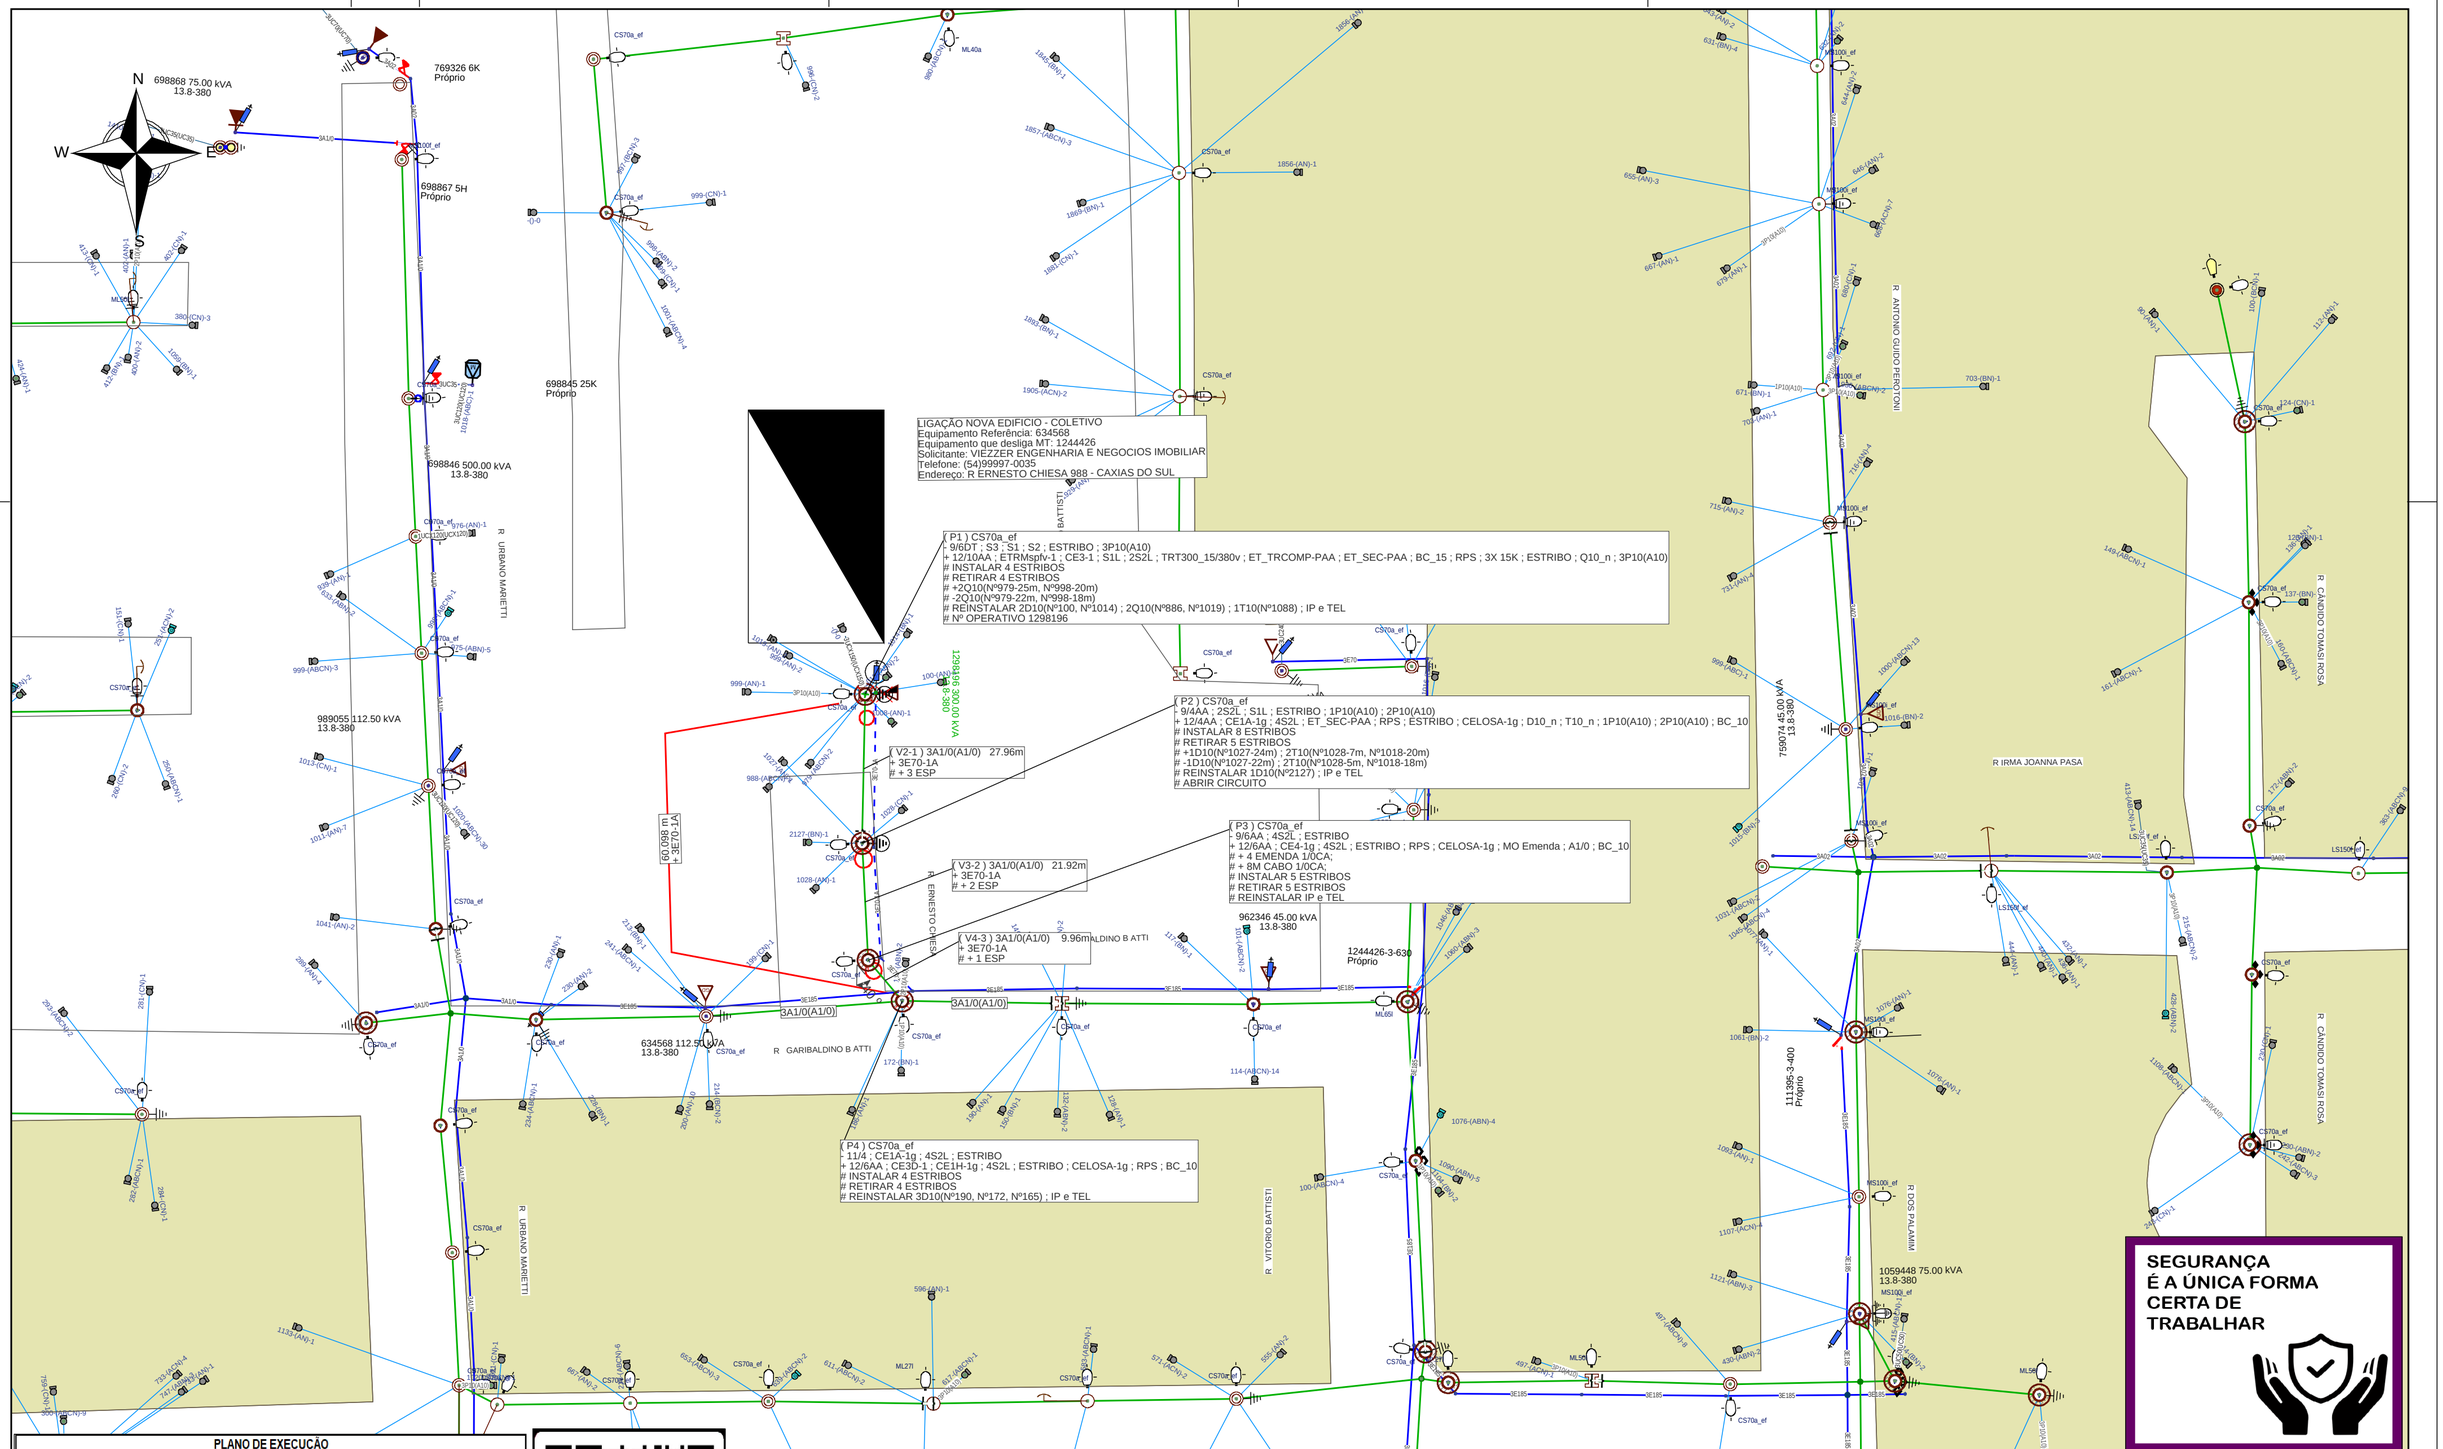

SEGURANÇA É A ÚNICA FORMA CERTA DE TRABALHAR

PLANO DE EXECUÇÃO

ABRIR CAVAS E PREPARAR OBRA PARA INSTALAÇÃO DE POSTES
REALIZAR TRABALHOS COM SEGURANÇA

P4 AO P1: ESTENDER REDE DE MT 3E70
P1: INSTALAR TR 300KVA;
P1: PONTO DE CONEXÃO DO SOLICITANTE.

Ação	Equipamento	Número	Clientes	Duração	CHI
Abrir	Transformador	634568	65	4	260
Linha Viva?		Sim	CHI TOTAL		260

Poste novo a ser instalado (quando indicado em planta)

FeedBack Para Fábrica de Projetos

Planeje
Use
Teste
Sinalize
Aterre

Ana Paula Bloedorn
Gerência de Processos de Obras e Manuntenção | DROP
Técnico de Projetos II
CFT: 002.795.320-32

CPFL ENERGIA

Gerência de Obras e Manutenção

Município: Caxias do Sul

Cliente: VIEZZER ENGENHARIA E NEGOCIOS IMOBILIARI

Obra: LIGAÇÃO NOVA EDIFICIO - COLETIVO

Endereço: R ERNESTO CHIESA 988 95059-130 CAXIAS DO SUL BR RS

Responsável Técnico:
Eng. Ederson Paulo Vogel
CREA: RS135794 ART: 10911826

Escala: 1:800	Data: 11/12/2025	Nota: 300001101611
Classe de isolação: 15kV	AL: CXD12	Folha 1
Projetista: unset	Projeto: 000007941704	Levantador ADELAR GRAFE