



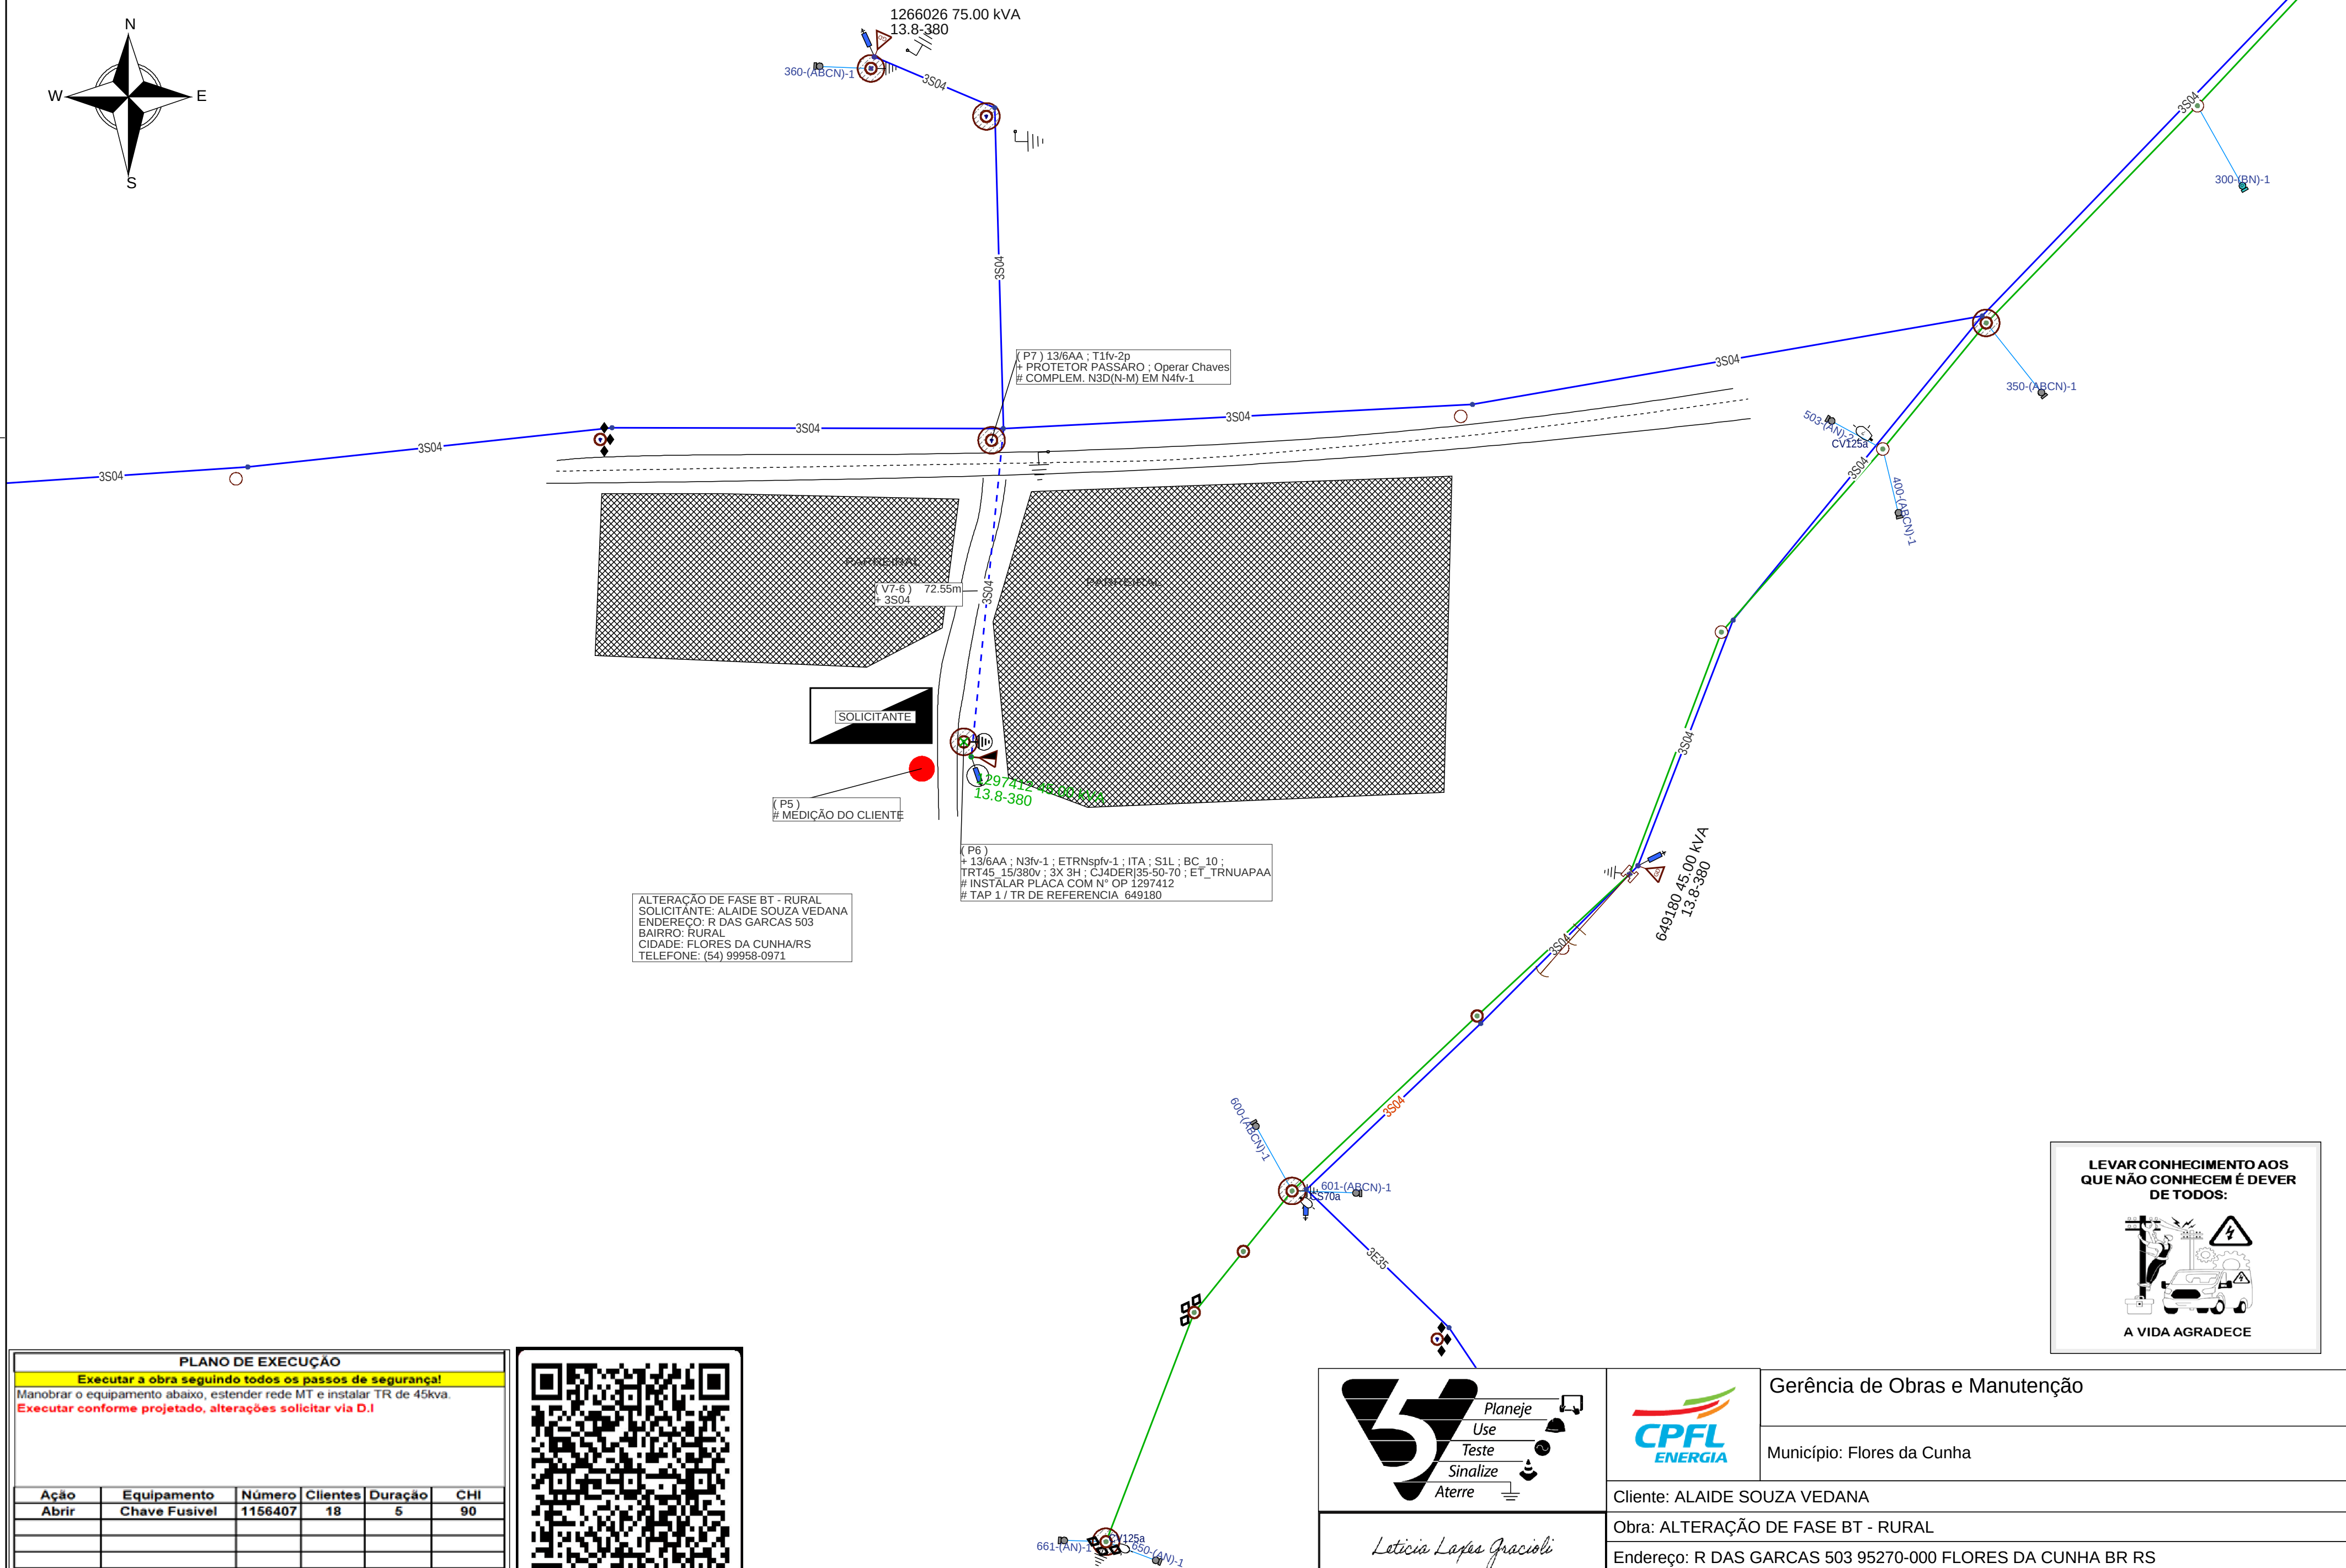

LEVAR CONHECIMENTO AOS QUE NÃO CONHECEM É DEVER DE TODOS:

A VIDA AGRADECE

PLANO DE EXECUÇÃO					
Executar a obra seguindo todos os passos de segurança!					
Manobrar o equipamento abaixo, estender rede MT e instalar TR de 45kva.					
Executar conforme projetado, alterações solicitar via D.I					
Ação	Equipamento	Número	Cientes	Duração	CHI
Abrir	Chave Fusível	1156407	18	5	90
Linha Viva?		Não	CHI TOTAL		90
☐ Poste novo a ser instalado (quando indicado em planta)					

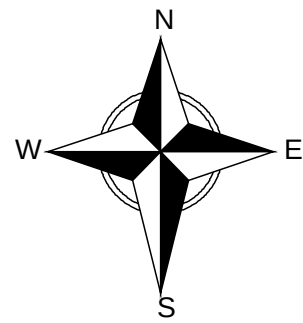

FeedBack Para Fábrica de Projetos

Planeje
Use
Teste
Sinalize
Aterre

Leticia Laxes Gracioli

Leticia Laxes Gracioli

Gerência de Processos de Obras e Manutenção | DROP

Técnico de Análise e Projetos

CFT: 03573031056

Gerência de Obras e Manutenção

Município: Flores da Cunha

Cliente: ALAIDE SOUZA VEDANA

Obra: ALTERAÇÃO DE FASE BT - RURAL

Endereço: R DAS GARCAS 503 95270-000 FLORES DA CUNHA BR RS

Responsável Técnico:	Eng. Ederson Paulo Vogel	Escala: 1:1000	Data: 09/12/2025	Nota: 300001101773
CREA: RS135794	ART: 10911826	Classe de isolamento: 15KV	AL: FCU14	Folha 1
		Projetista: Leticia Laxes	Projeto: 000007940486	Levantador: Marcio Bedin