


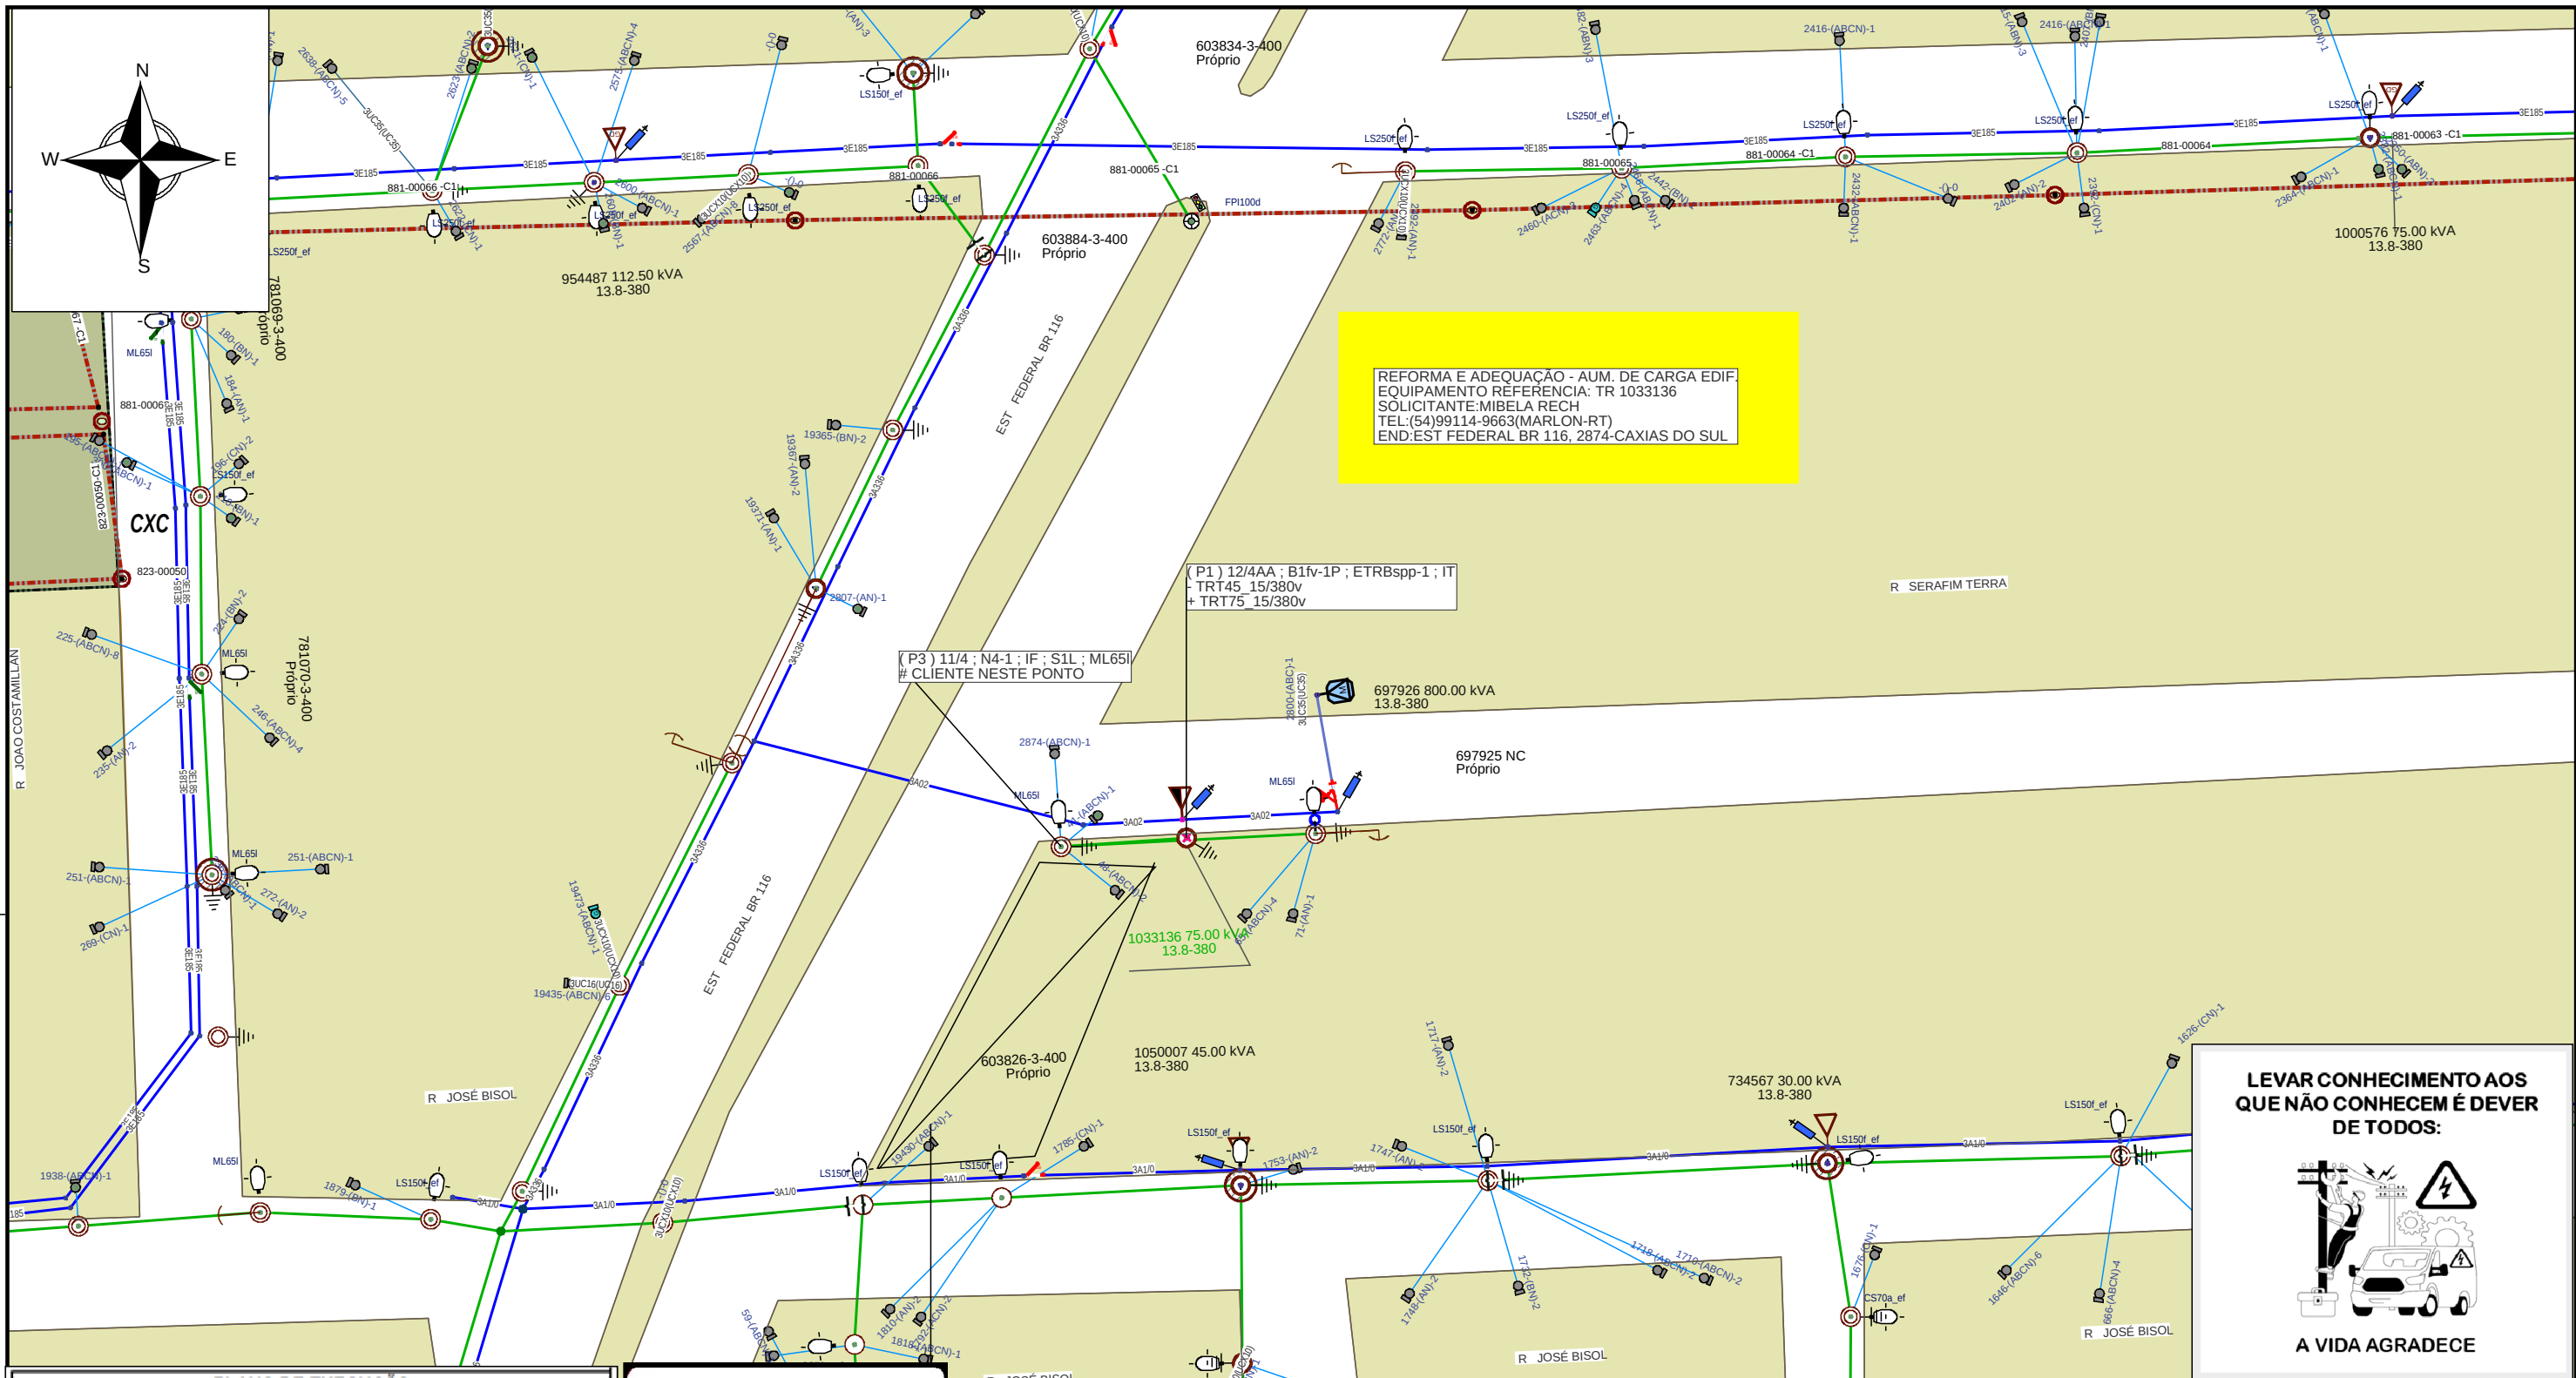

PLANO DE EXECUÇÃO					
Executar a obra seguindo todos os passos de segurança					
Ação	Equipamento	Número	Clientes	Duração	CHI
Abrir	Transformador	1033136	9	4	36
					0
					0
					0
					0
					0
Linha Viva?			CHI TOTAL		36
☐ Poste novo a ser instalado (quando indicado em planta)					

FeedBack Para Fábrica de Projetos

Planeje
Use
Teste
Sinalize
Aterre

Rodrigo De Vargas Santos
Gerência de Processos de Obras e Manutenção | DROP
Técnico de Análise e Projetos
CFT: 00235489085

Gerência de Obras e Manutenção
Município: Caxias do Sul

Cliente: MIBELA RECH
Obra: REFORMA E ADEQUAÇÃO - AUM. DE CARGA EDIF
Endereço: EST FEDERAL BR 116 2874 95070-070 CAXIAS DO SUL BR RS

Responsável Técnico:

Eng. Ederson Paulo Vogel
CREA: RS135794 ART: 10911826

Escala: 1:850
Classe de isolamento: 15kV
Projetista: Rodrigo Santos

Data: 12/12/2025
AL: CXC12
Projeto: 000007943061

Nota: 300001102835
Folha 1
Levantador: Reinhold Brulinger