


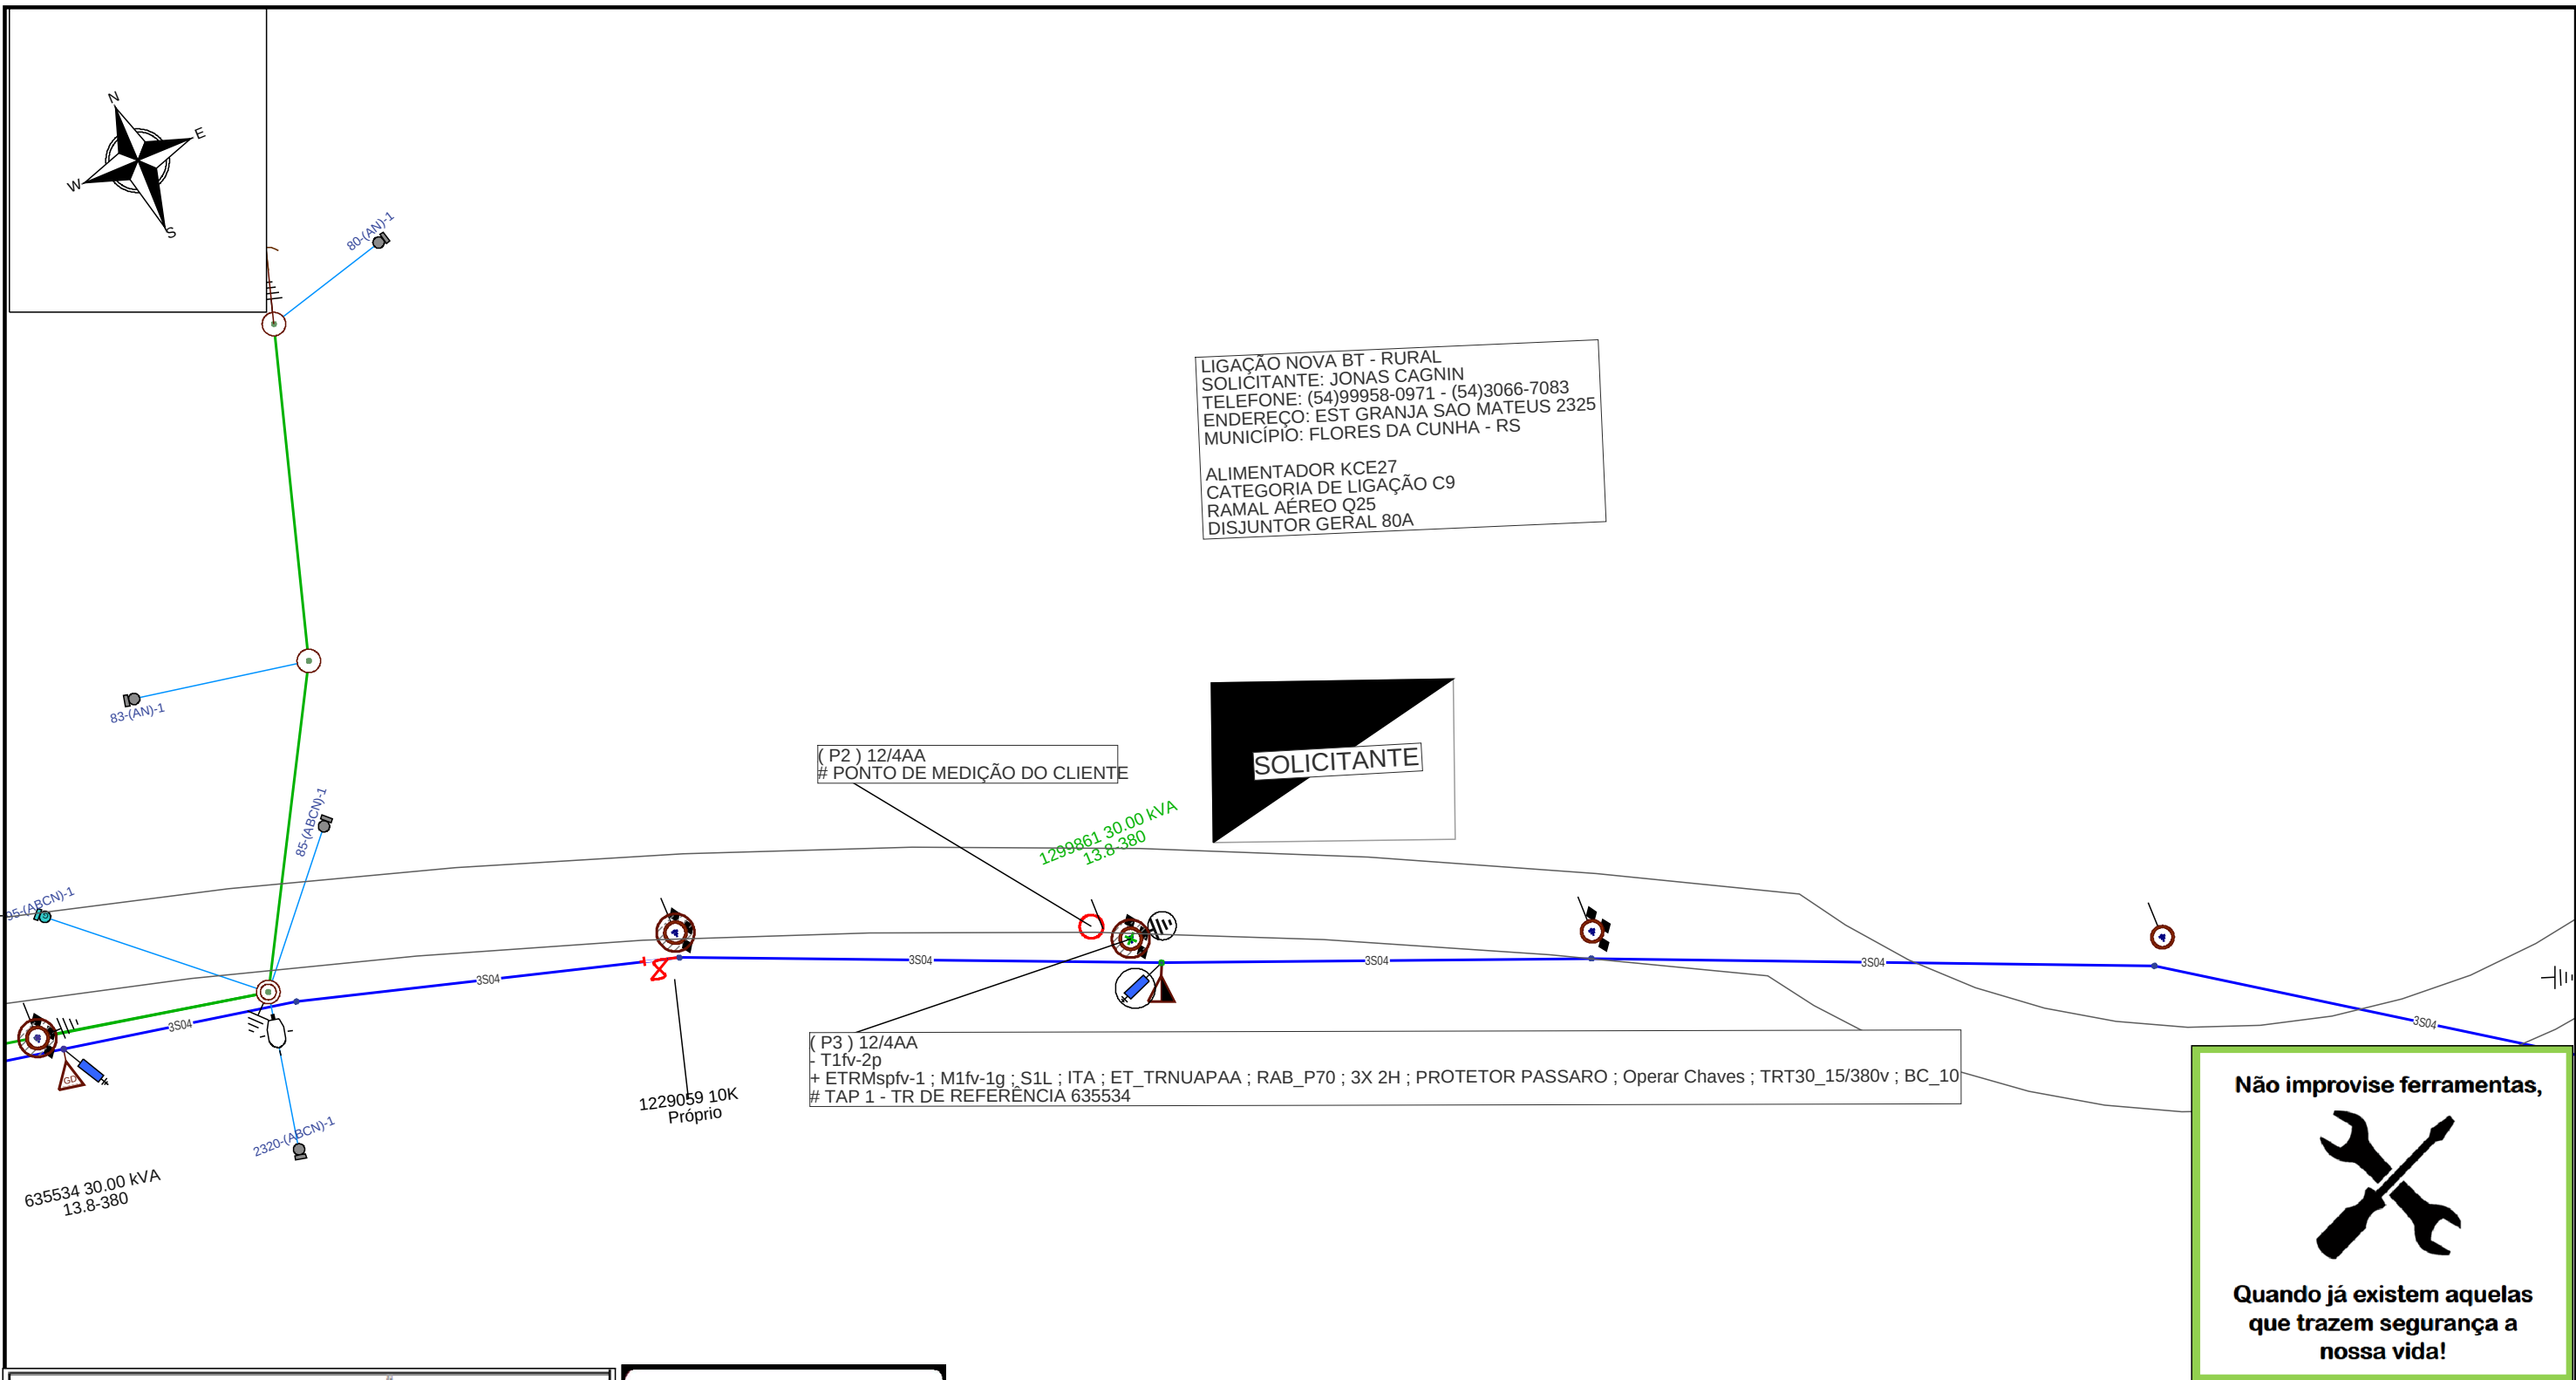

PLANO DE EXECUÇÃO					
Executar a obra seguindo todos os passos de segurança!					
Abrir chave faca e, em LM, instalar Tr de 30 kVA.					
Ação	Equipamento	Número	Cientes	Duração	CHI
Abrir	Chave Faca	1008383	73	5	365
Abrir	Chave Faca	1005704			
Ligar	Religador	1002666			
Linha Viva?		Não	CHI TOTAL		365
☐ Poste novo a ser instalado (quando indicado em planta)					

QR Code

FeedBack Para Fábrica de Projetos

Logo CPFL ENERGIA

Planeje
Use
Teste
Sinalize
Aterre

Willian C. Mendonça

Willian Coelho Mendonça

Gerência de Processos de Obras e Manutenção | DROP

Técnico de Análise e Projetos

CFT: 04127459093

Gerência de Obras e Manutenção	
Município: Flores da Cunha	
Cliente: JONAS CAGNIN	
Obra: LIGAÇÃO NOVA BT	
Endereço: EST GRANJA SAO MATEUS 2325 95270-000 FLORES DA CUNHA BR RS	
Responsável Técnico:	Eng. Ederson Paulo Vogel CREA: RS135794 ART: 10911826
Escala: 1:700	Data: 24/12/2025
Classe de isolamento: 15kV	AL: KCE27
Projetista: Willian Coelho	Projeto: 000007950363
Nota: 300001105568	Folha 1
Levantador: Ricardo Albuquerque	