


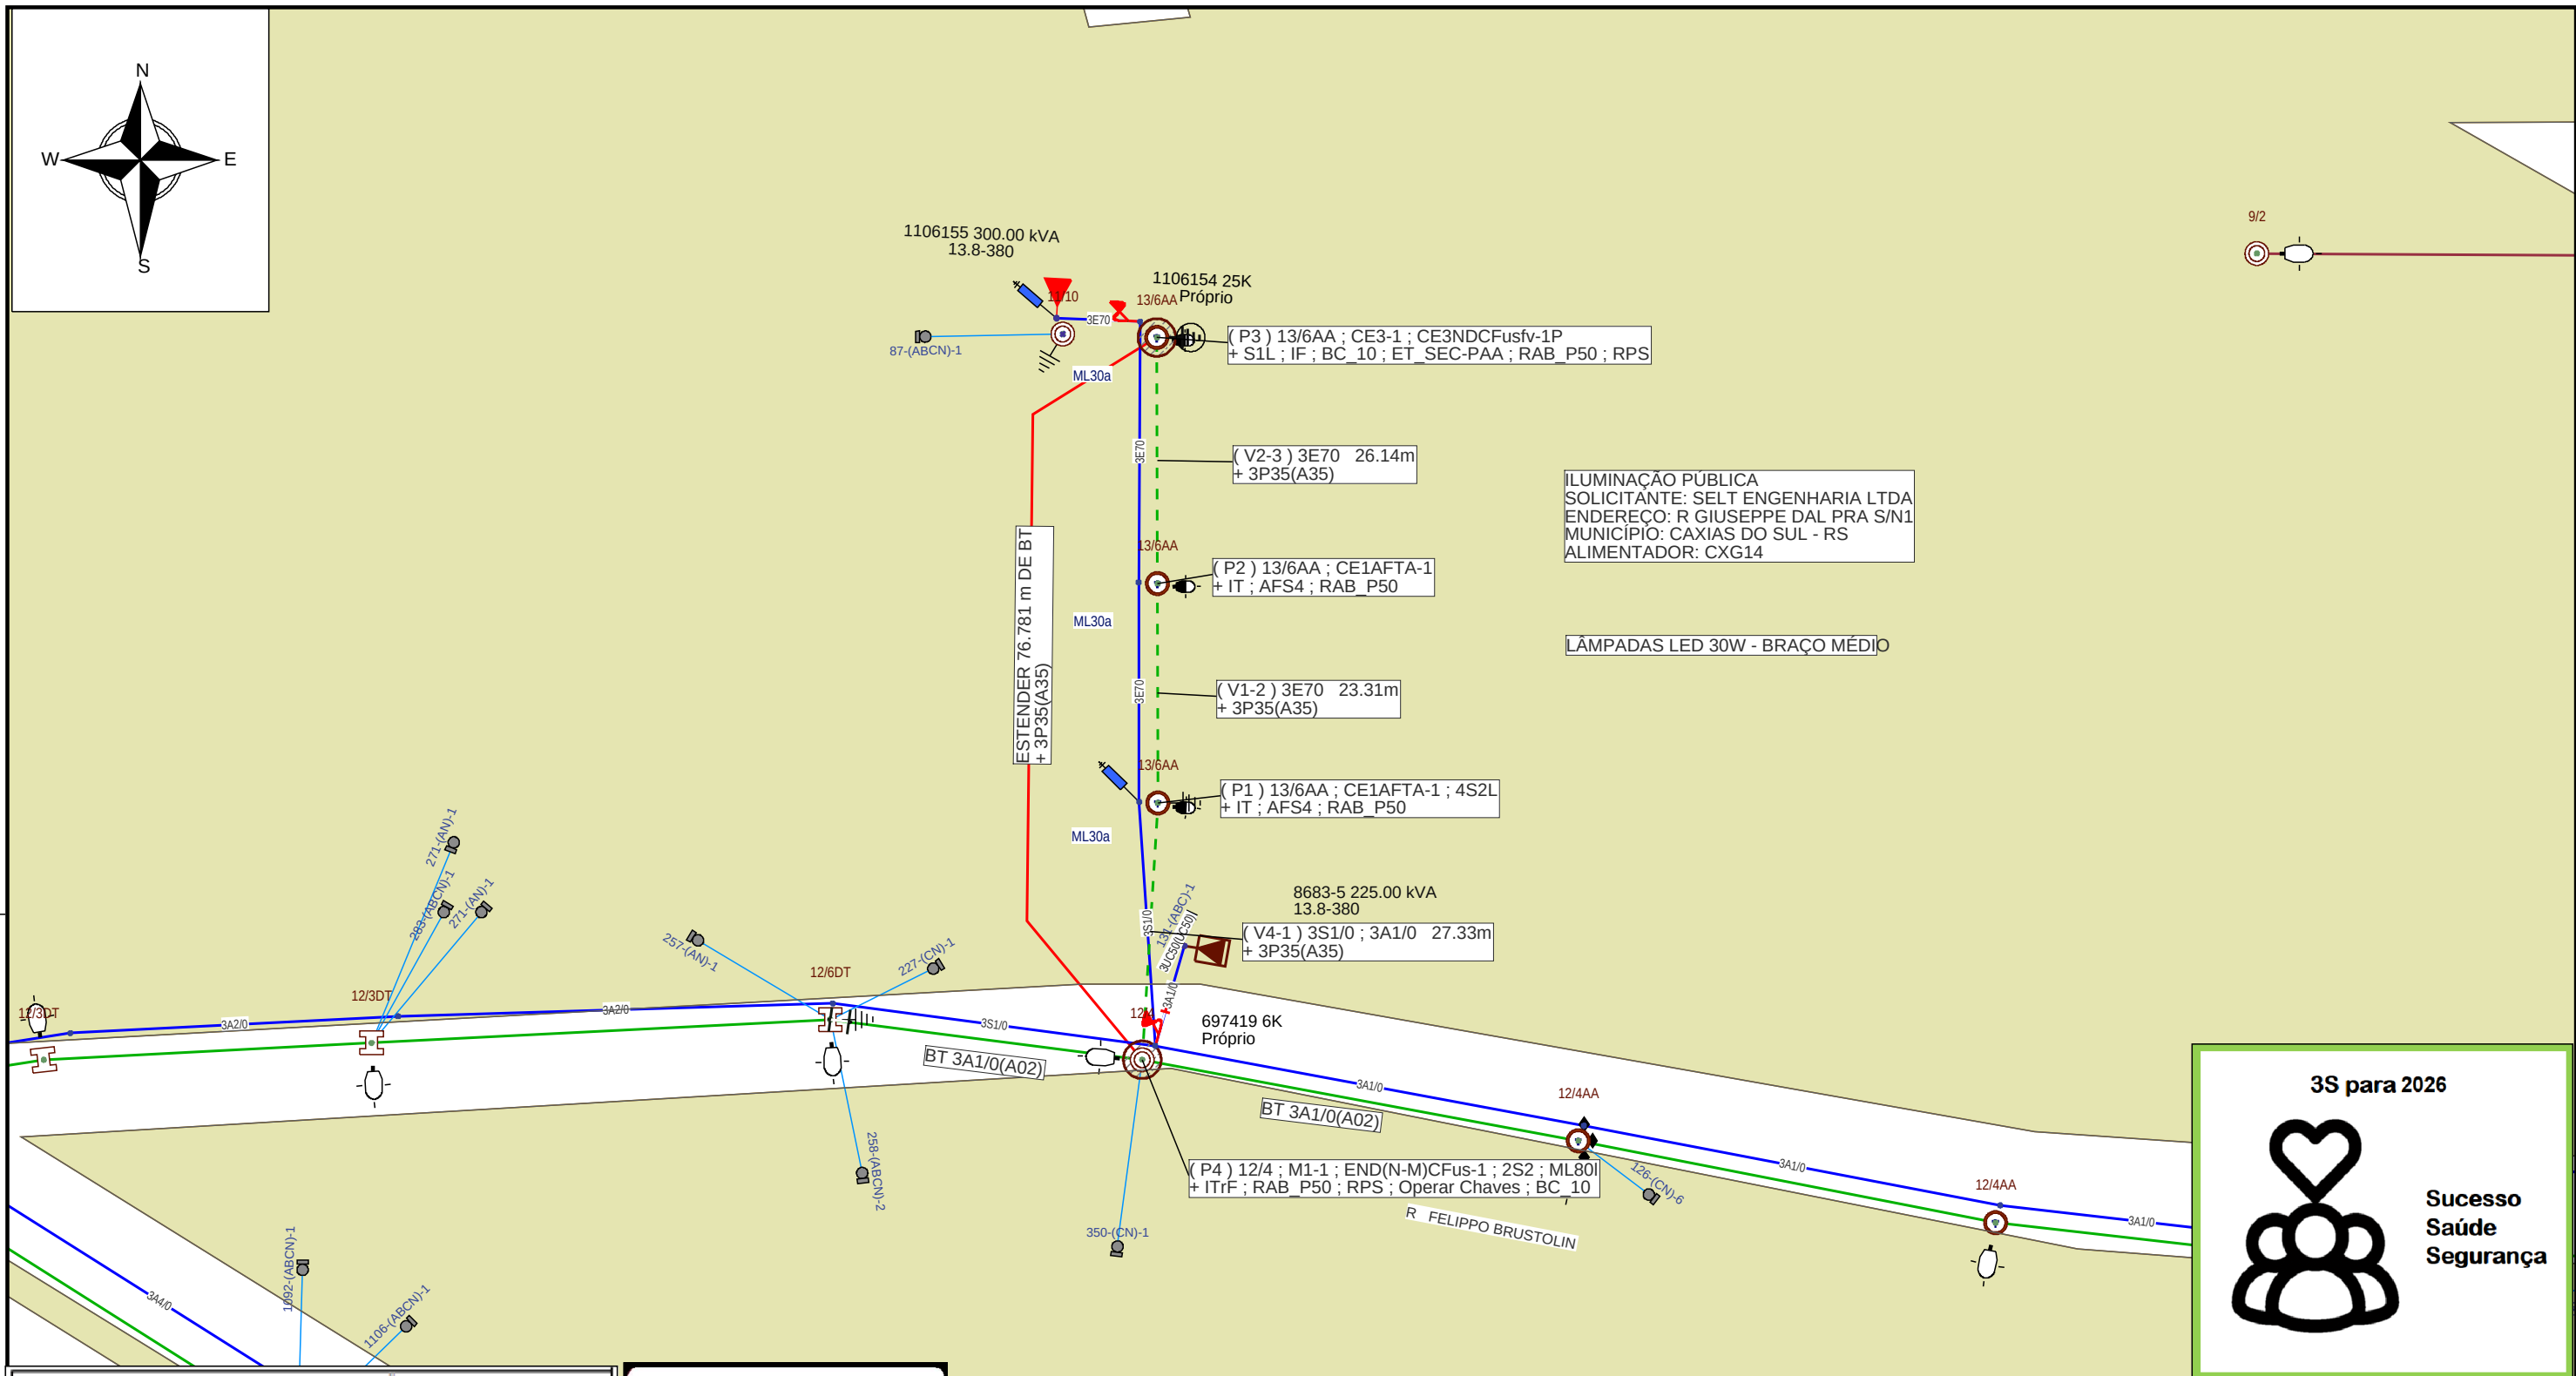

PLANO DE EXECUÇÃO					
Executar a obra seguindo todos os passos de segurança!					
Abrir Tr e, em LM, estender BT 3P35(A35) para atender as IPs.					

FeedBack Para Fábrica de Projetos

Planeje
Use
Teste
Sinalize
Aterre


Willian C. Mendonça

Willian Coelho Mendonça

Gerência de Processos de Obras e Manutenção | DROP

Técnico de Análise e Projetos

CFT: 04127459093

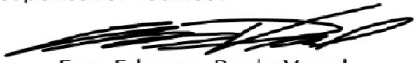	Gerência de Obras e Manutenção		
	Município: Caxias do Sul		
Cliente: SELT ENGENHARIA LTDA			
Obra: ILUMINAÇÃO PUBLICA AMPLIAÇÃO SUBSTITUIÇÃO			
Endereço: R GIUSEPPE DAL PRA S/N1 95098-180 CAXIAS DO SUL BR RS			
Responsável Técnico:  Eng. Ederson Paulo Vogel CREA: RS135794 ART: 10911826	Escala: 1:700	Data: 30/12/2025	Nota: 300001106880
	Classe de isolamento: 15kV	AL: CXG14	Folha 1
	Projetista: Willian Coelho	Projeto: 000007952484	Levantador: Adelar Grafe