
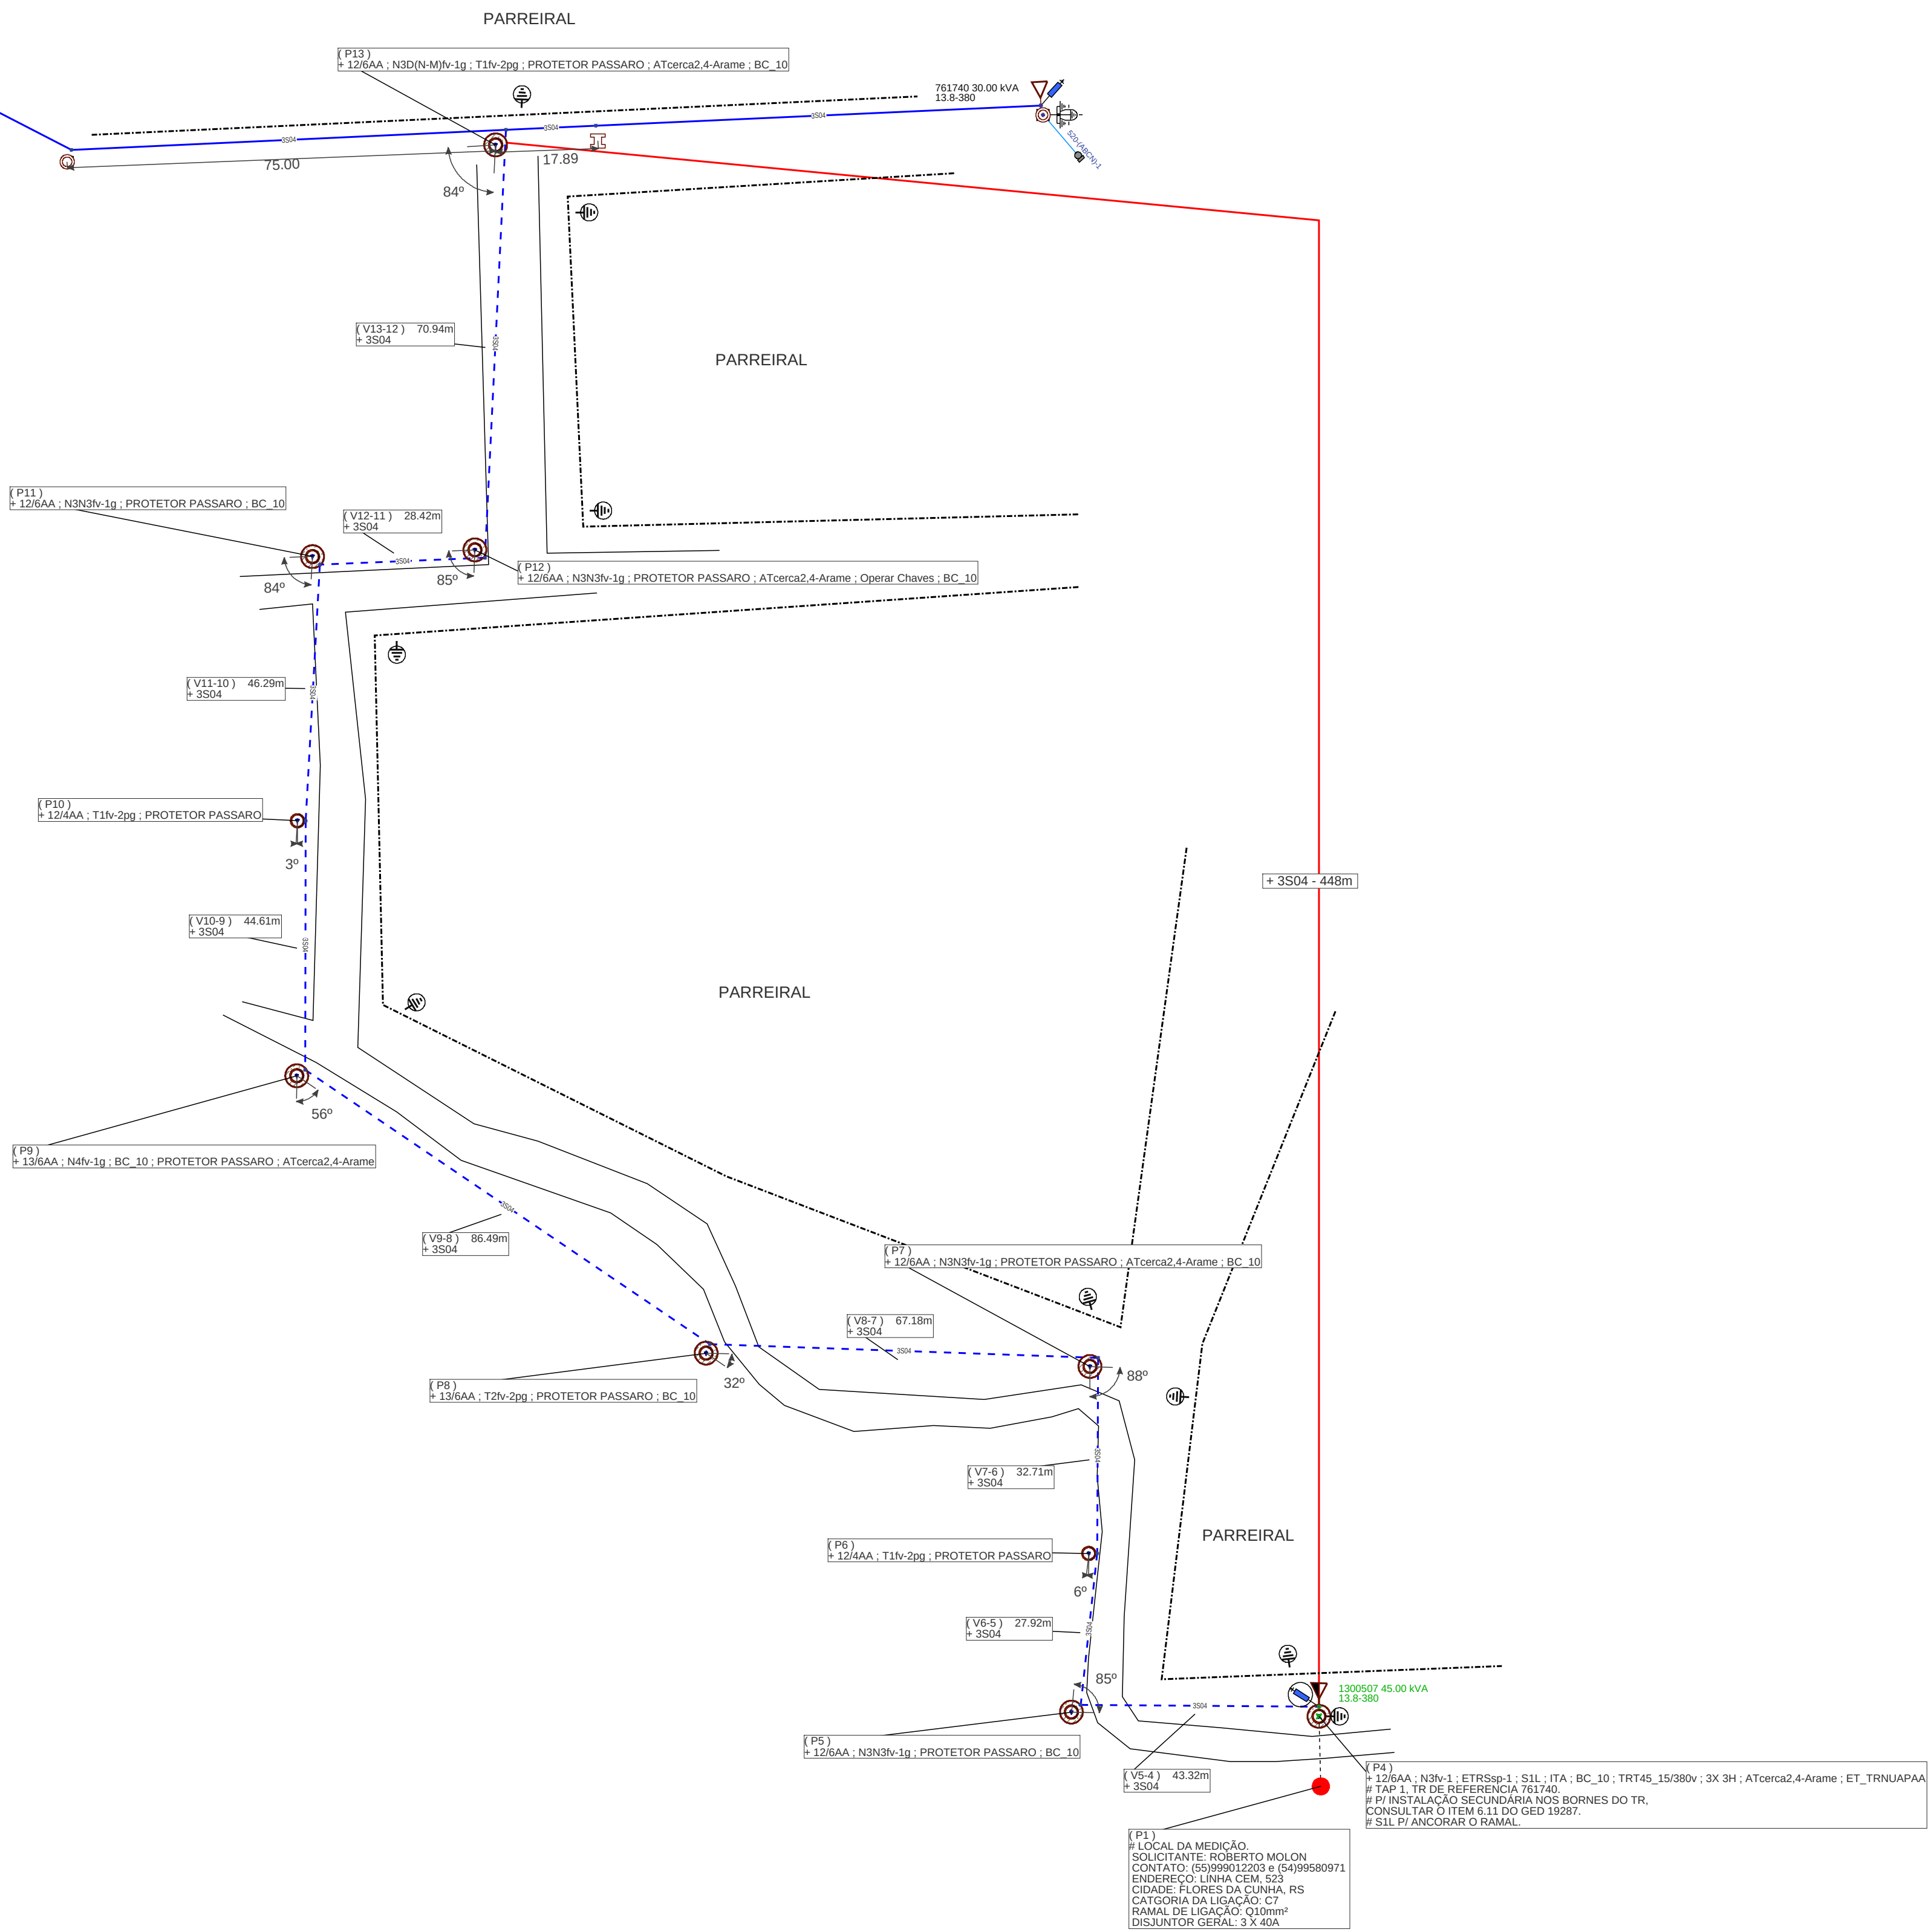


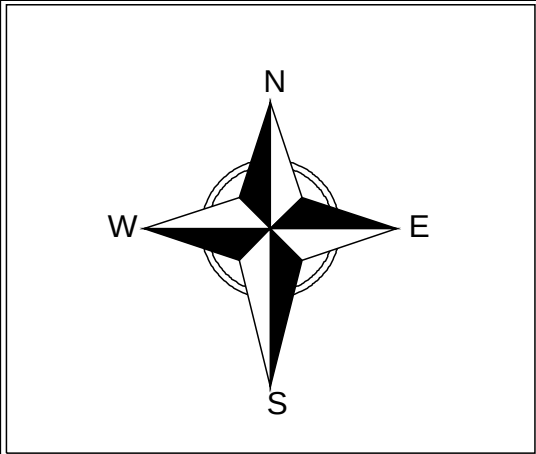

PLANO DE EXECUÇÃO

EXECUTAR ATIVIDADES COM SEGURANÇA!

CONSTRUIR REDE DE MT NOVA E INSTALAR TR DE 45 KVA.
COMEÇAR A OBRA NA ÁREA LIVRE, DO P4 AO P12 APÓS A OBRA CONCLUÍDA
NESSE TRECHO, DESLIGAR A FACA 911027 P/ ATIVIDADES NO P13, ANCORANDO
E CONECTANDO A REDE NOVA.

EXECUTAR ATIVIDADES DE ACORDO COM O PROJETO. ALTERAÇÕES, SOLICITAR D. I.

Ação	Equipamento	Número	Clientes	Duração	CHI
Abrir	Chave Faca	911027	14	5	70
Linha Viva?		Não	CHI TOTAL		70

Feedback Para Fábrica de Projetos

Quem semeia a segurança,

Colhe qualidade de vida.

Planeje
Use
Teste
Sinalize
Aterre

Gerência de Obras e Manutenção

Município: Flores da Cunha

Cliente: ROBERTO MOLON

Obra: LIGAÇÃO NOVA BT - RURAL

Endereço: LINHA CEM, 523 95270-000 FLORES DA CUNHA BR RS

Responsável Técnico:

Eng. Ederson Paulo Vogel
CREA: RS 33575/4 ART: 3093.1826

Escala: 1:800

Data: 31/12/2025

Nota: 300001106934

Classe de Isolção: 15kV

AL: FCU14

Folha 1

Projeto: EDSON PAPALIA

Projeto: 000007952876

Levantador: MARCIO BECIN

Edson Dilmar Papalia Flores
Edson Dilmar Papalia Flores
Gerência de Processos de Obras e Manutenção | DROP
Técnico de Análise e Projetos
CFT: 220.942.817-3