


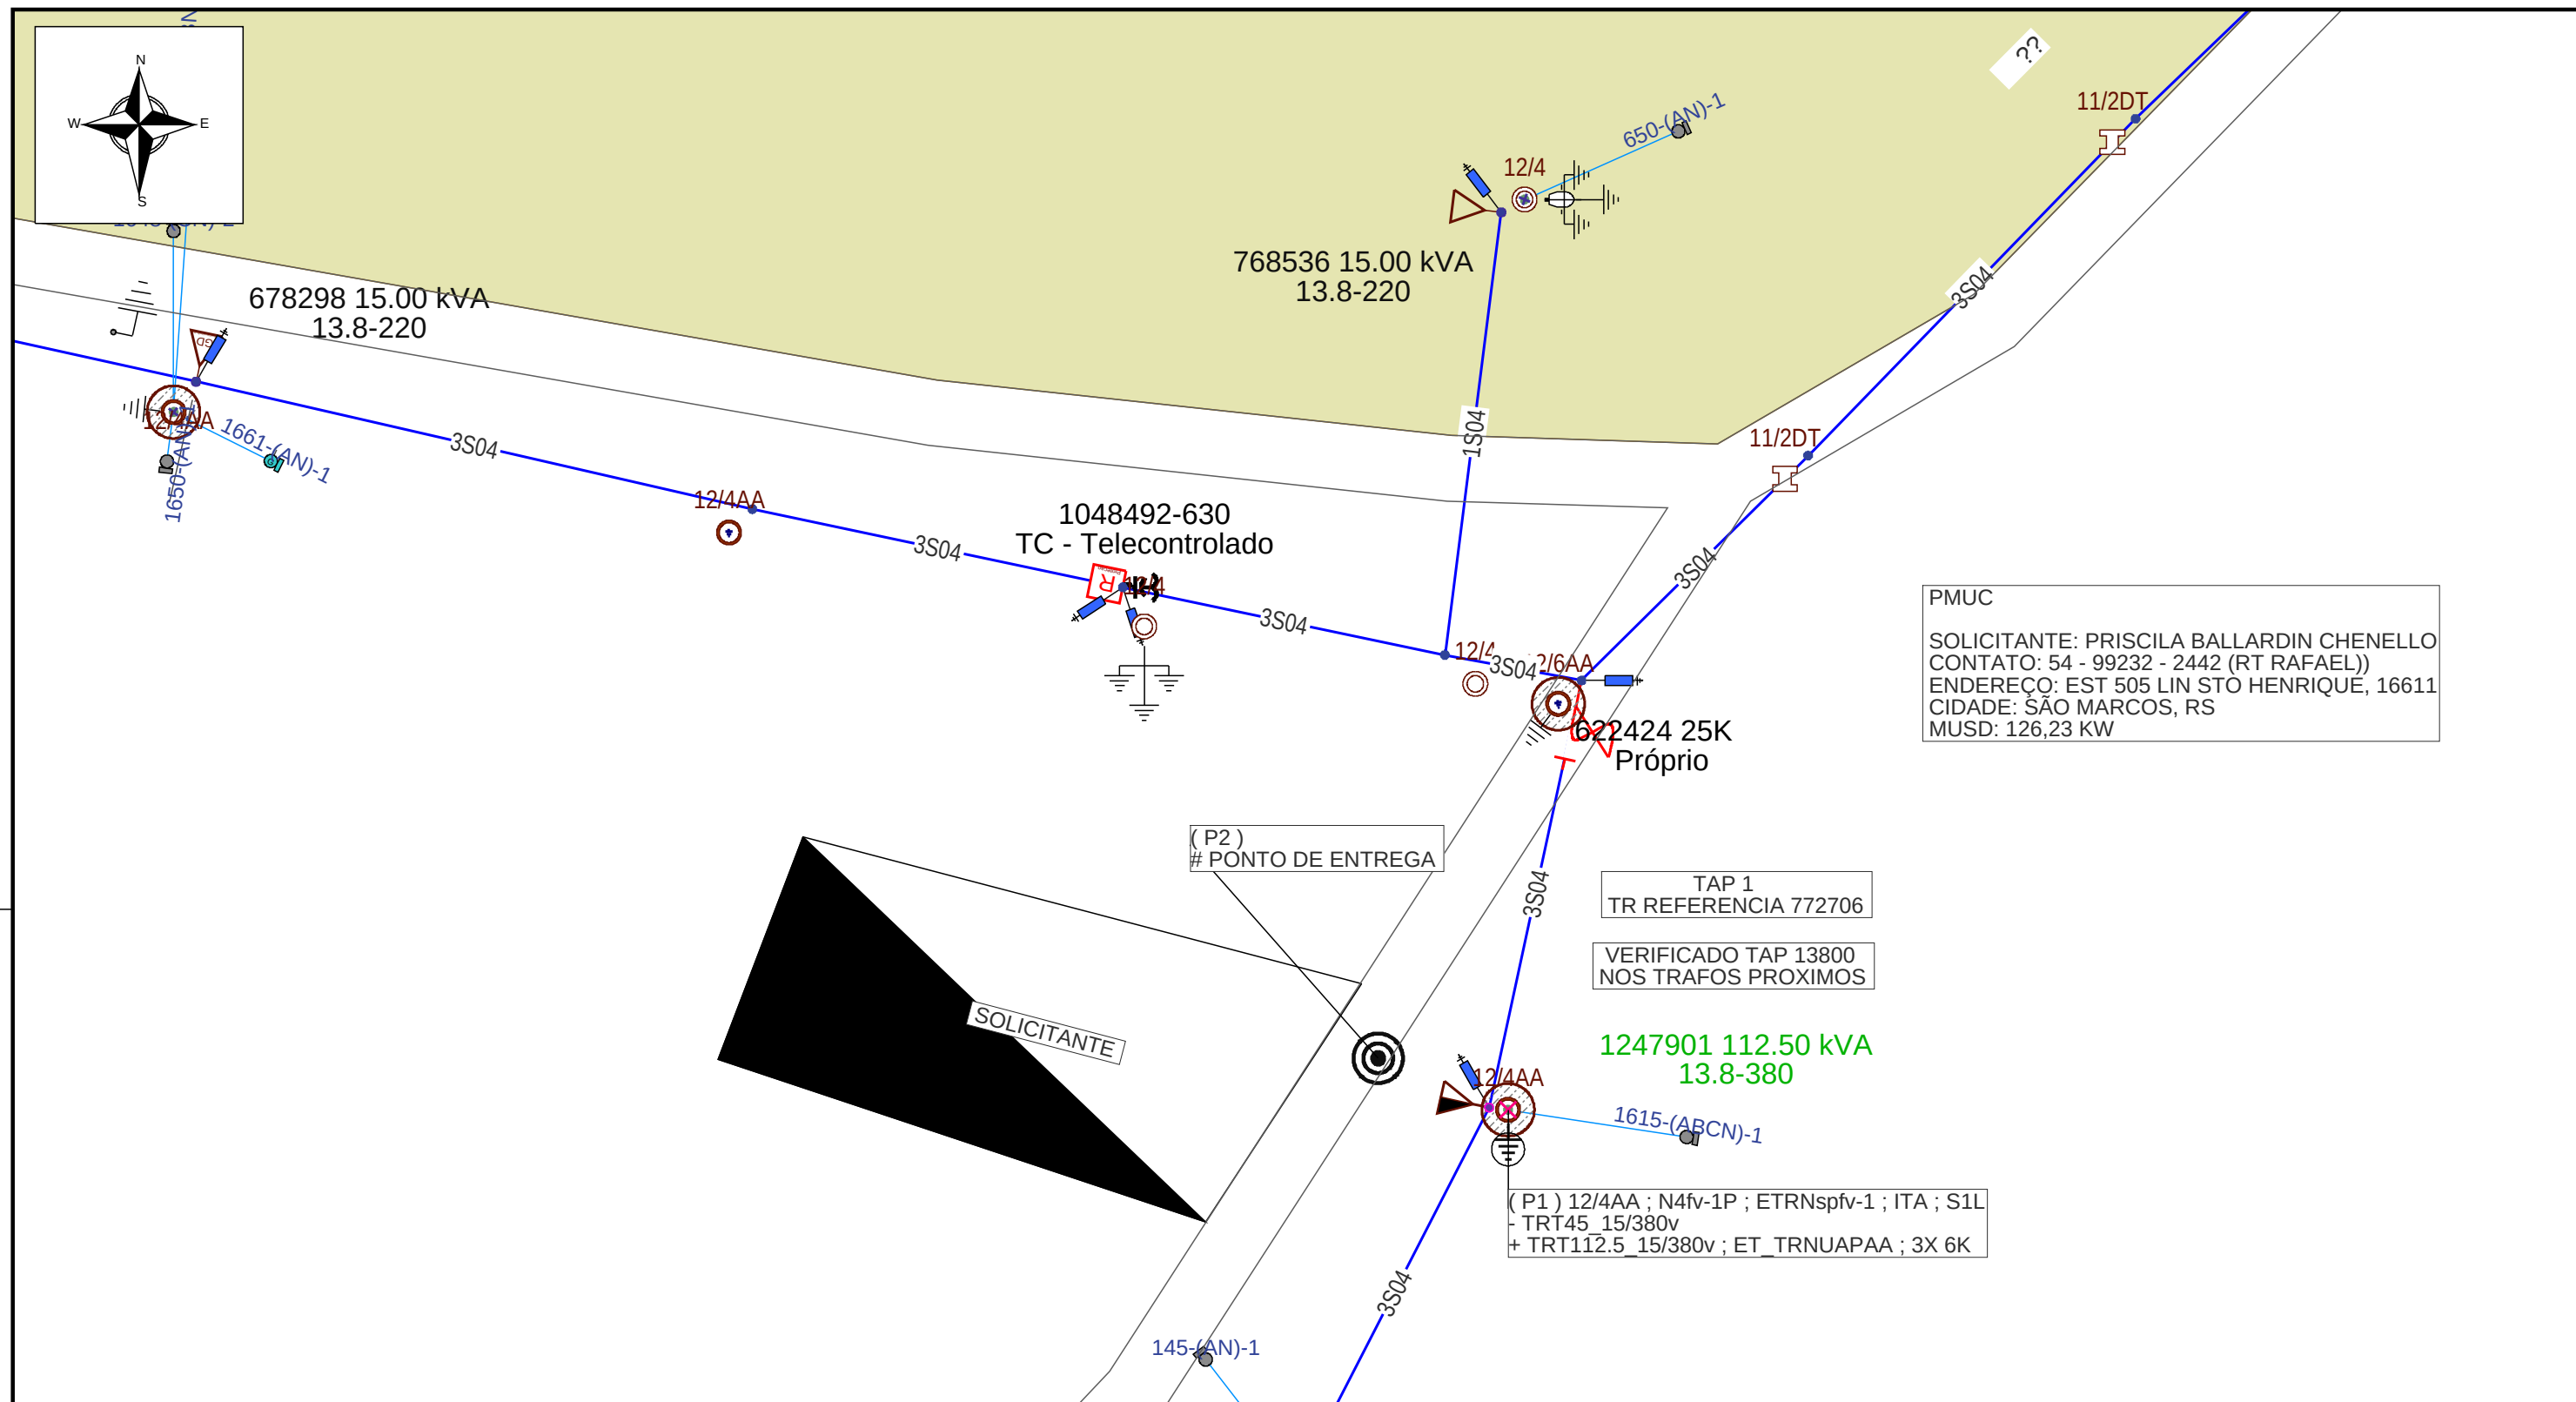

PMUC
SOLICITANTE: PRISCILA BALLARDIN CHENELLO
CONTATO: 54 - 99232 - 2442 (RT RAFAEL)
ENDEREÇO: EST 505 LIN STO HENRIQUE, 16611
CIDADE: SÃO MARCOS, RS
MUSD: 126,23 KW

TAP 1
TR REFERENCIA 772706

VERIFICADO TAP 13800
NOS TRAFOS PROXIMOS

1247901 112.50 kVA
13.8-380

(P1) 12/4AA ; N4fv-1P ; ETRNspfv-1 ; ITA ; S1L
- TRT45_15/380v
+ TRT112.5_15/380v ; ET_TRNUAPAA ; 3X 6K

PLANO DE EXECUÇÃO					
Executar atividades com segurança, respeitando normas e orientações					
Substituir em P1, trafo de 45 kVA do TR 1247901 por outro de 112.5 kVA					
Recolher resíduos após o término das obras					
Qualquer alteração, solicitar via Desing I					
Ação	Equipamento	Número	Clientes	Duração	CHI
Abrir	Transformador	1247901	1	4	4
					0
					0
					0
					0
					0
Linha Viva?			CHI TOTAL		4
☐ Poste novo a ser instalado (quando indicado em planta)					

FeedBack Para Fábrica de Projetos

Não fique em cima do muro

Trabalhe sempre seguro!

Planeje
Use
Teste
Sinalize
Aterre

Diego Souza Ribeiro

Gerência de Processos de Obras e Manutenção | DROP

Técnico de Análise e Projetos

CFT: 021.824.880-65

Gerência de Obras e Manutenção

Município: São Marcos

Cliente: PRISCILA BALLARDIN CHENELLO

Obra: LIGAÇÃO NOVA EDIFICIO - COLETIVO

Endereço: R ENDEREÇO PROVISORIO S/N1 99999-999 SAO MARCOS BR RS

Responsável Técnico:

Eng. Ederson Paulo Vogel
CREA: RS135794 ART: 10911826

Escala: 1:800

Classe de isolamento:
15kV

Projetista: DIEGO RIBEIRO

Data: 22/01/2026

AL: SMC14

Projeto: 000007966146

Nota: 300001108145

Folha 1

Levantador