


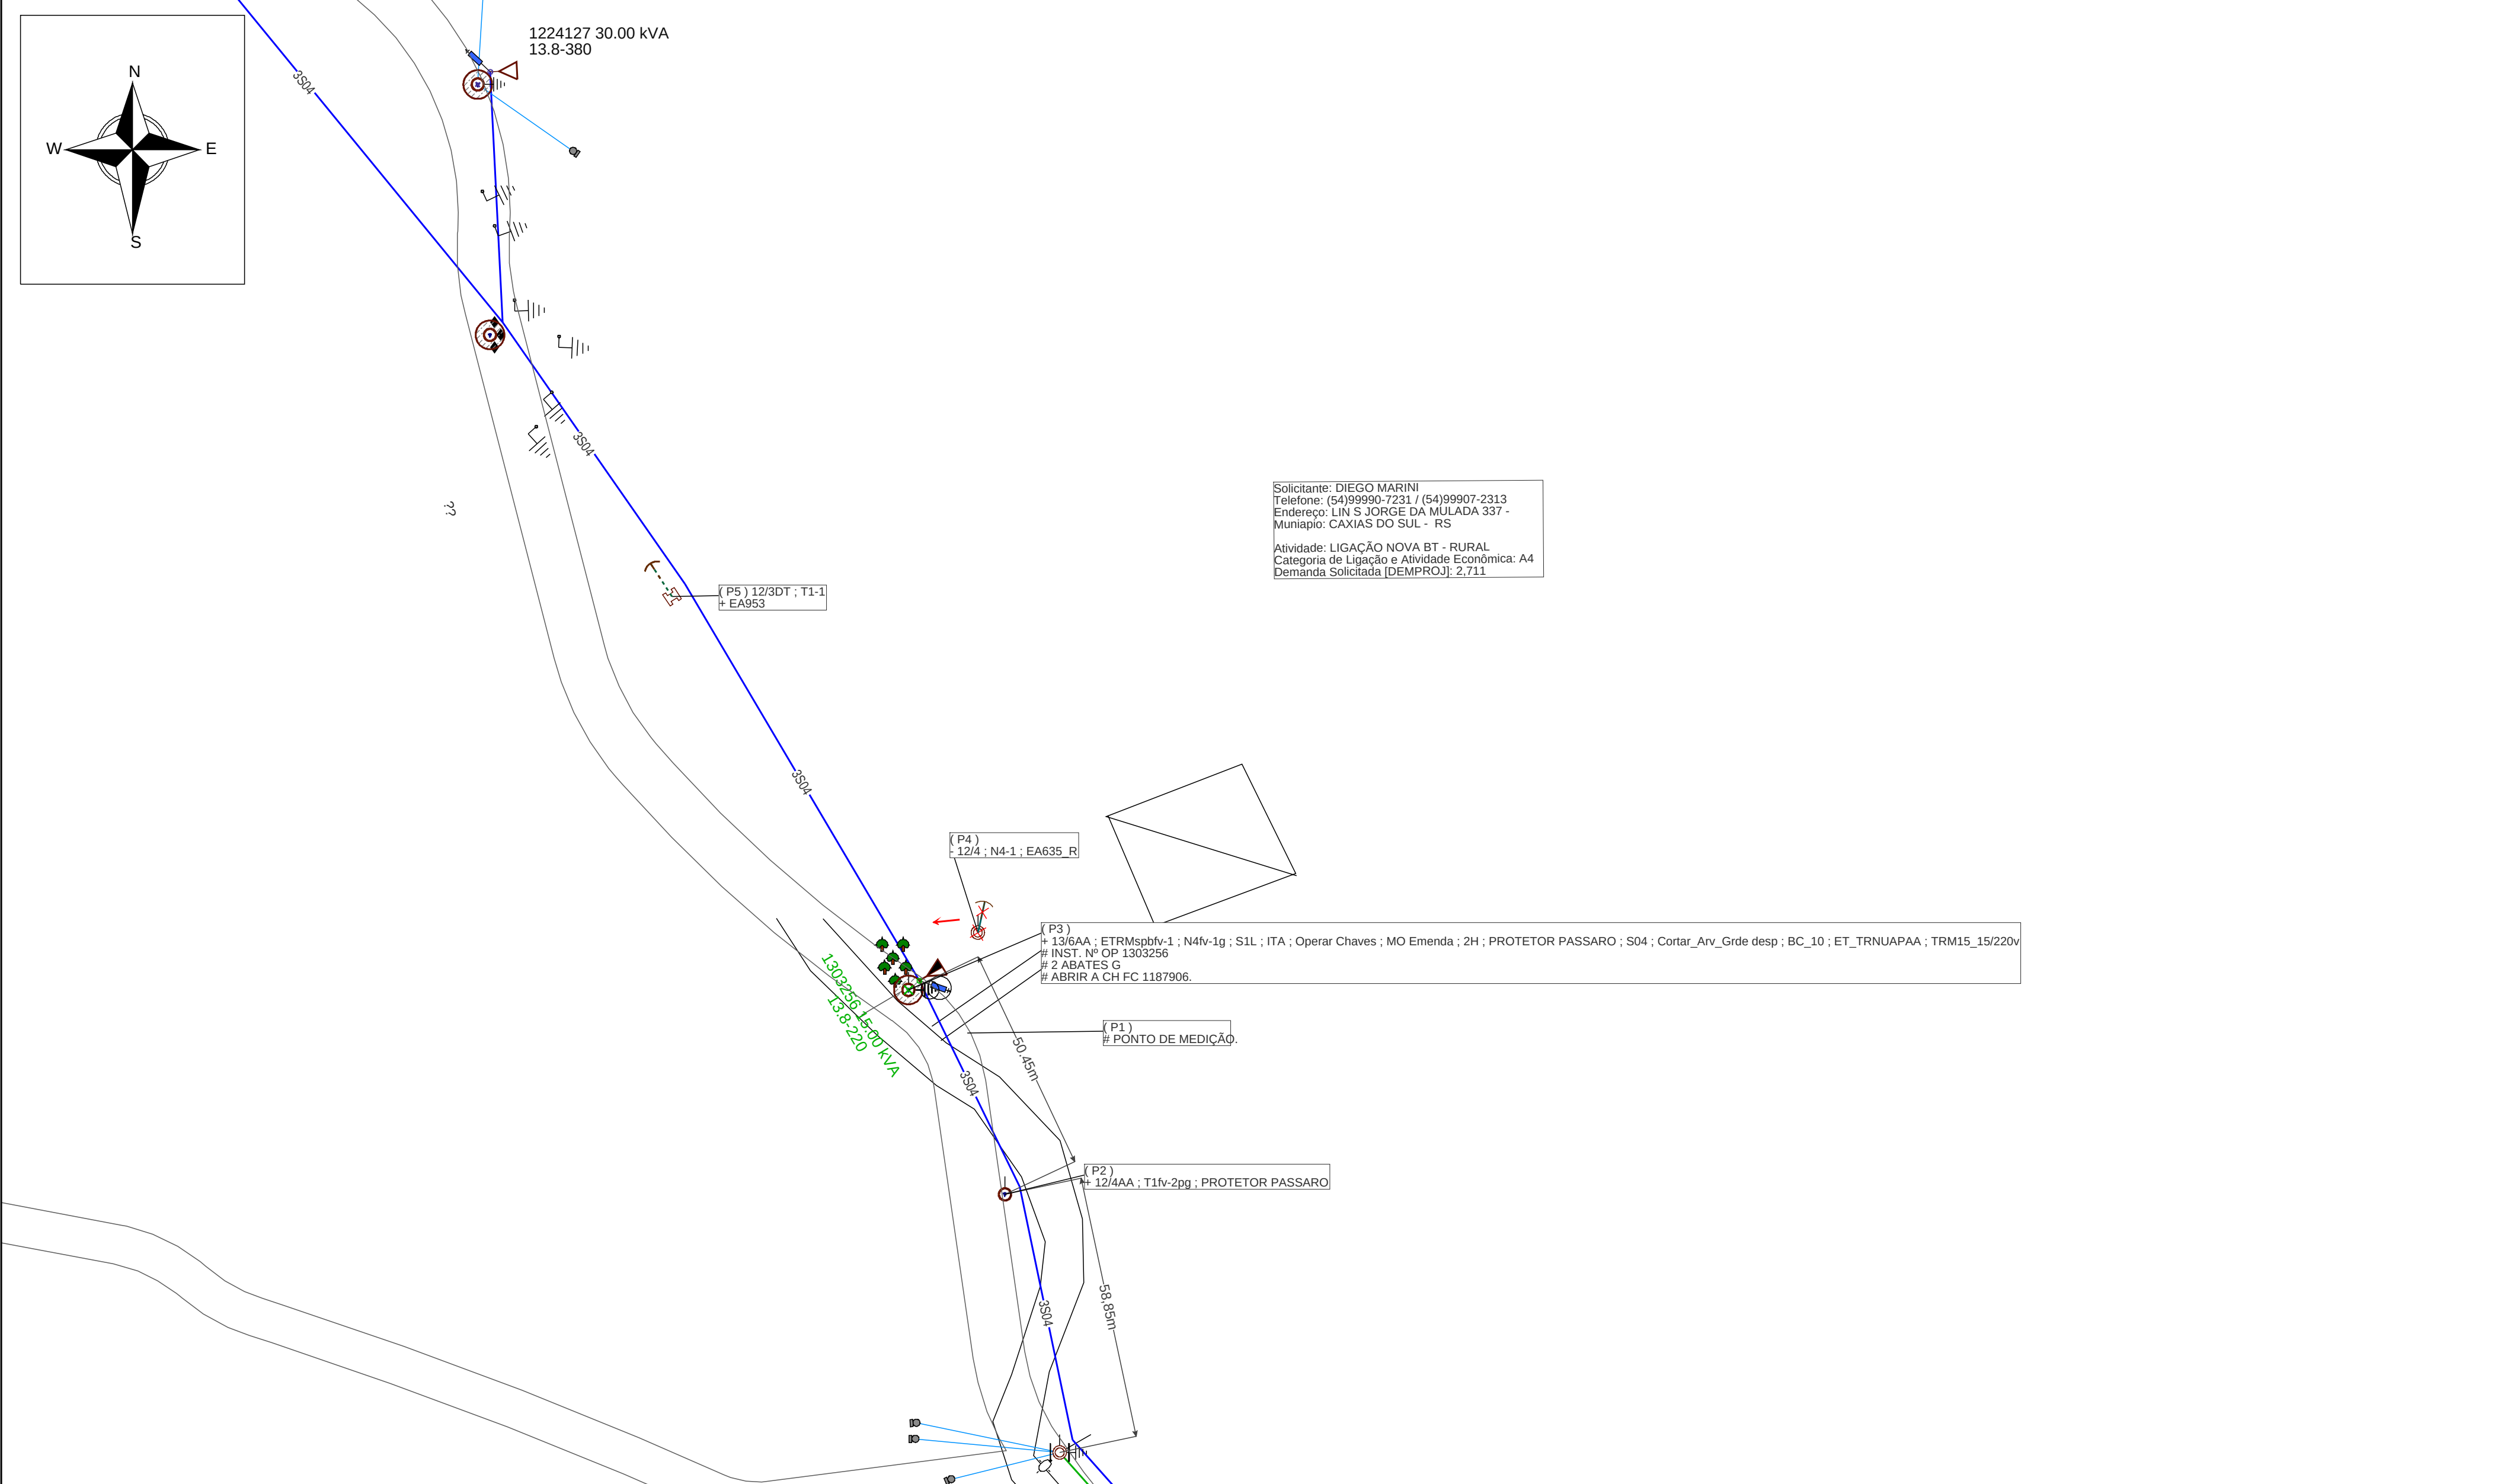

Solicitante: DIEGO MARINI
Telefone: (54)99990-7231 / (54)99907-2313
Endereço: LIN S JORGE DA MULADA 337 -
Muniapio: CAXIAS DO SUL - RS
Atividade: LIGAÇÃO NOVA BT - RURAL
Categoria de Ligação e Atividade Econômica: A4
Demanda Solicitada [DEMPROJ]: 2,711

(P3)
+ 13/6AA ; ETRMspbvf-1 ; N4fv-1g ; S1L ; ITA ; Operar Chaves ; MO Emenda ; 2H ; PROTETOR PASSARO ; S04 ; Cortar_Arv_Grde desp ; BC_10 ; ET_TRNUAPAA ; TRM15_15/220v
INST. Nº OP 1303256
2 ABATES G
ABRIR A CH FC 1187906.

(P1)
PONTO DE MEDIÇÃO.

(P2)
+ 12/4AA ; T1fv-2pg ; PROTETOR PASSARO

PLANO DE EXECUÇÃO					
Executar a instalação de postes, instalação de TR para a ligação nova BT.					
Ação	Equipamento	Número	Cientes	Duração	CHI
Abrir	Chave Faca	1187906	232	4	928
					0
					0
					0
					0
Linha Viva?		Não	CHI TOTAL		928
☐ Poste novo a ser instalado (quando indicado em planta)					
Inserir Nota 300001111012					

FeedBack Para Fábrica de Projetos

Acidentes não acontecem
por acaso

mas sim por descaso!

Planeje
Use
Teste
Sinalize
Aterre

Tiago Faveron

Tiago Faveron

Gerência de Processos de Obras e Manutenção | DROP

Técnico de Análise e Projetos

CFT: 837.082.780-20

Gerência de Obras e Manutenção			
Município: Caxias do Sul			
Cliente: DIEGO MARINI			
Obra: LIGAÇÃO NOVA BT - RURAL			
Endereço: LIN S JORGE DA MULADA 337 95143-000 CAXIAS DO SUL BR RS			
Responsável Técnico:		Escala: 1:1000	Data: 02/02/2026
Eng. Ederson Paulo Vogel		Classe de isolamento: 15kV	AL: SMC13
CREA: RS135794		Projeto: 000007966878	Folha 1
ART: 10911826		Projeto: 000007966878	Levantador: Marcio Bedin