



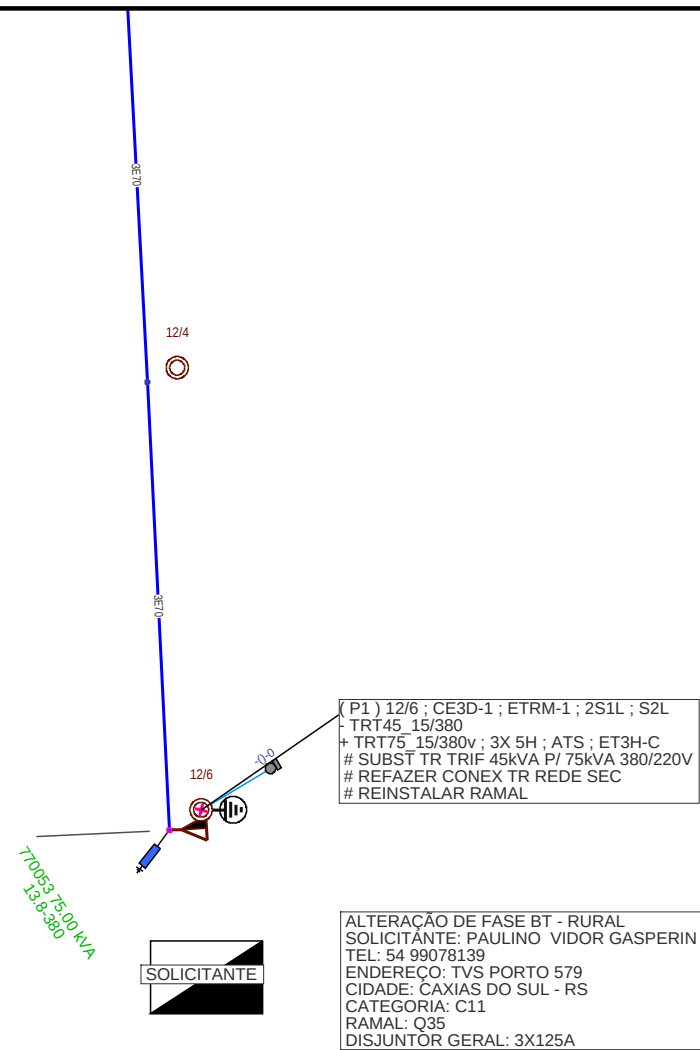

Descuido é risco

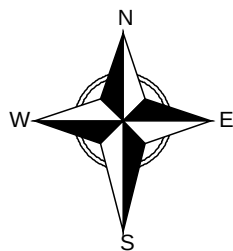

Segurança é vida

PLANO DE EXECUÇÃO

P1: SUBSTITUIR TR TRIF 45kVA P/ 75kVA 380/220V.

Executar as atividades conforme planejado, alterações solicitar via D.I.


Realizar as operações com segurança !

Ação	Equipamento	Número	Cientes	Duração	CHI
Abrir	Transformador	770053	1	6	6
					0
					0
					0
					0
					0
Linha Viva?		Não	CHI TOTAL		6

Poste novo a ser instalado (quando indicado em planta)



FeedBack Para Fábrica de Projetos

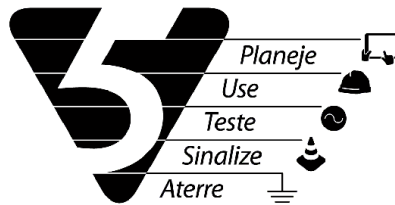

Iury de Souza Deckmann

Iury de Souza Deckmann

Gerência de Processos de Obras e Manutenção | DROP

Técnico de Análise e Projetos

CFT: 046.153340-52



Gerência de Obras e Manutenção

Município: Caxias do Sul

Cliente: PAULINO VIDOR GASPERIN

Obra: ALTERAÇÃO DE FASE BT - RURAL

Endereço: TVS PORTO 579 95000-001 CAXIAS DO SUL BR RS

Responsável Técnico:

Eng. Ederson Paulo Vogel
CREA: RS135794 ART: 10911826

Escala: 1:850

Classe de isolamento:
15kV

Projetista: Iury
Deckmann

Data: 23/01/2026

AL: FCU12

Projeto: 000007967047

Nota:
300001111101

Folha 1

Levantador: Adelar Miguel