

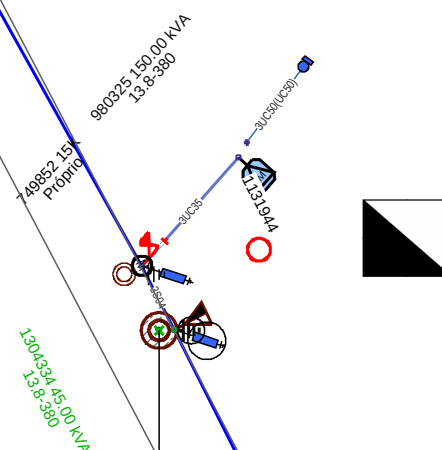


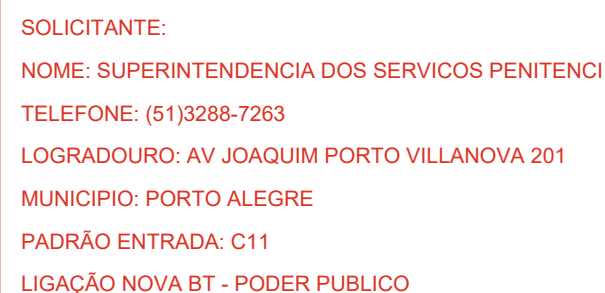


(P3)
+ 12/6AA; M1fv-1P; ETRSp-1; S1L; ITA; BC_10; PROTETOR PASSARO: 3X 3H; ATS; ET_Trt; TRT45_15/380V
MONTAR TR SEM BT CONFORME GED 19287 - ESTRUTURA DE TRANSFORMADOR SEM REDE SECUNDÁRIA
TAP 1 REF 634379
INSTALAR N° OPERATIVO 1304334
EXECUTAR COM LV

Na corrente da segurança

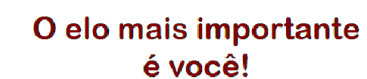

PLANO DE EXECUÇÃO					
# INSTALAR 1 POSTE					
# INSTALAR TR DE 45kVA					
Executar as atividades com segurança repetindo normas e orientações, Não alterar o projeto sem solicitar ao projetista					
Ação	Equipamento	Número	Clientes	Duração	CHI
Linha Viva?			Sim	CHI TOTAL	
				0	

○ Poste novo a ser instalado (quando indicado em planta)

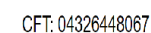

Gerência de Obras e Manutenção

Município: São Francisco de Paula

Cliente: SUPERINTENDENCIA DOS SERVICOS PENITENCIA

Obra: LIGAÇÃO NOVA BT - PODER PUBLICO

Endereço: EST MUN ROSA FERRI MARTINI 9876 95143-000 CAXIAS DO SUL BR RS

Responsável Técnico:

Eng. Ederson Paulo Vogel
CREA: RS135794 ART: 10911826

Escala: 1:850

	Data: 26/01/2026
--	------------------

Nota:	300001111506
-------	--------------

Classe de isolamento:	15kV
-----------------------	------

AL: CXD13

	3000011
	Folha 1

Projeto: JEREMIAS DUARTE

Projeto: 000007967833

	Levantador: Valdir Neri
--	-------------------------