


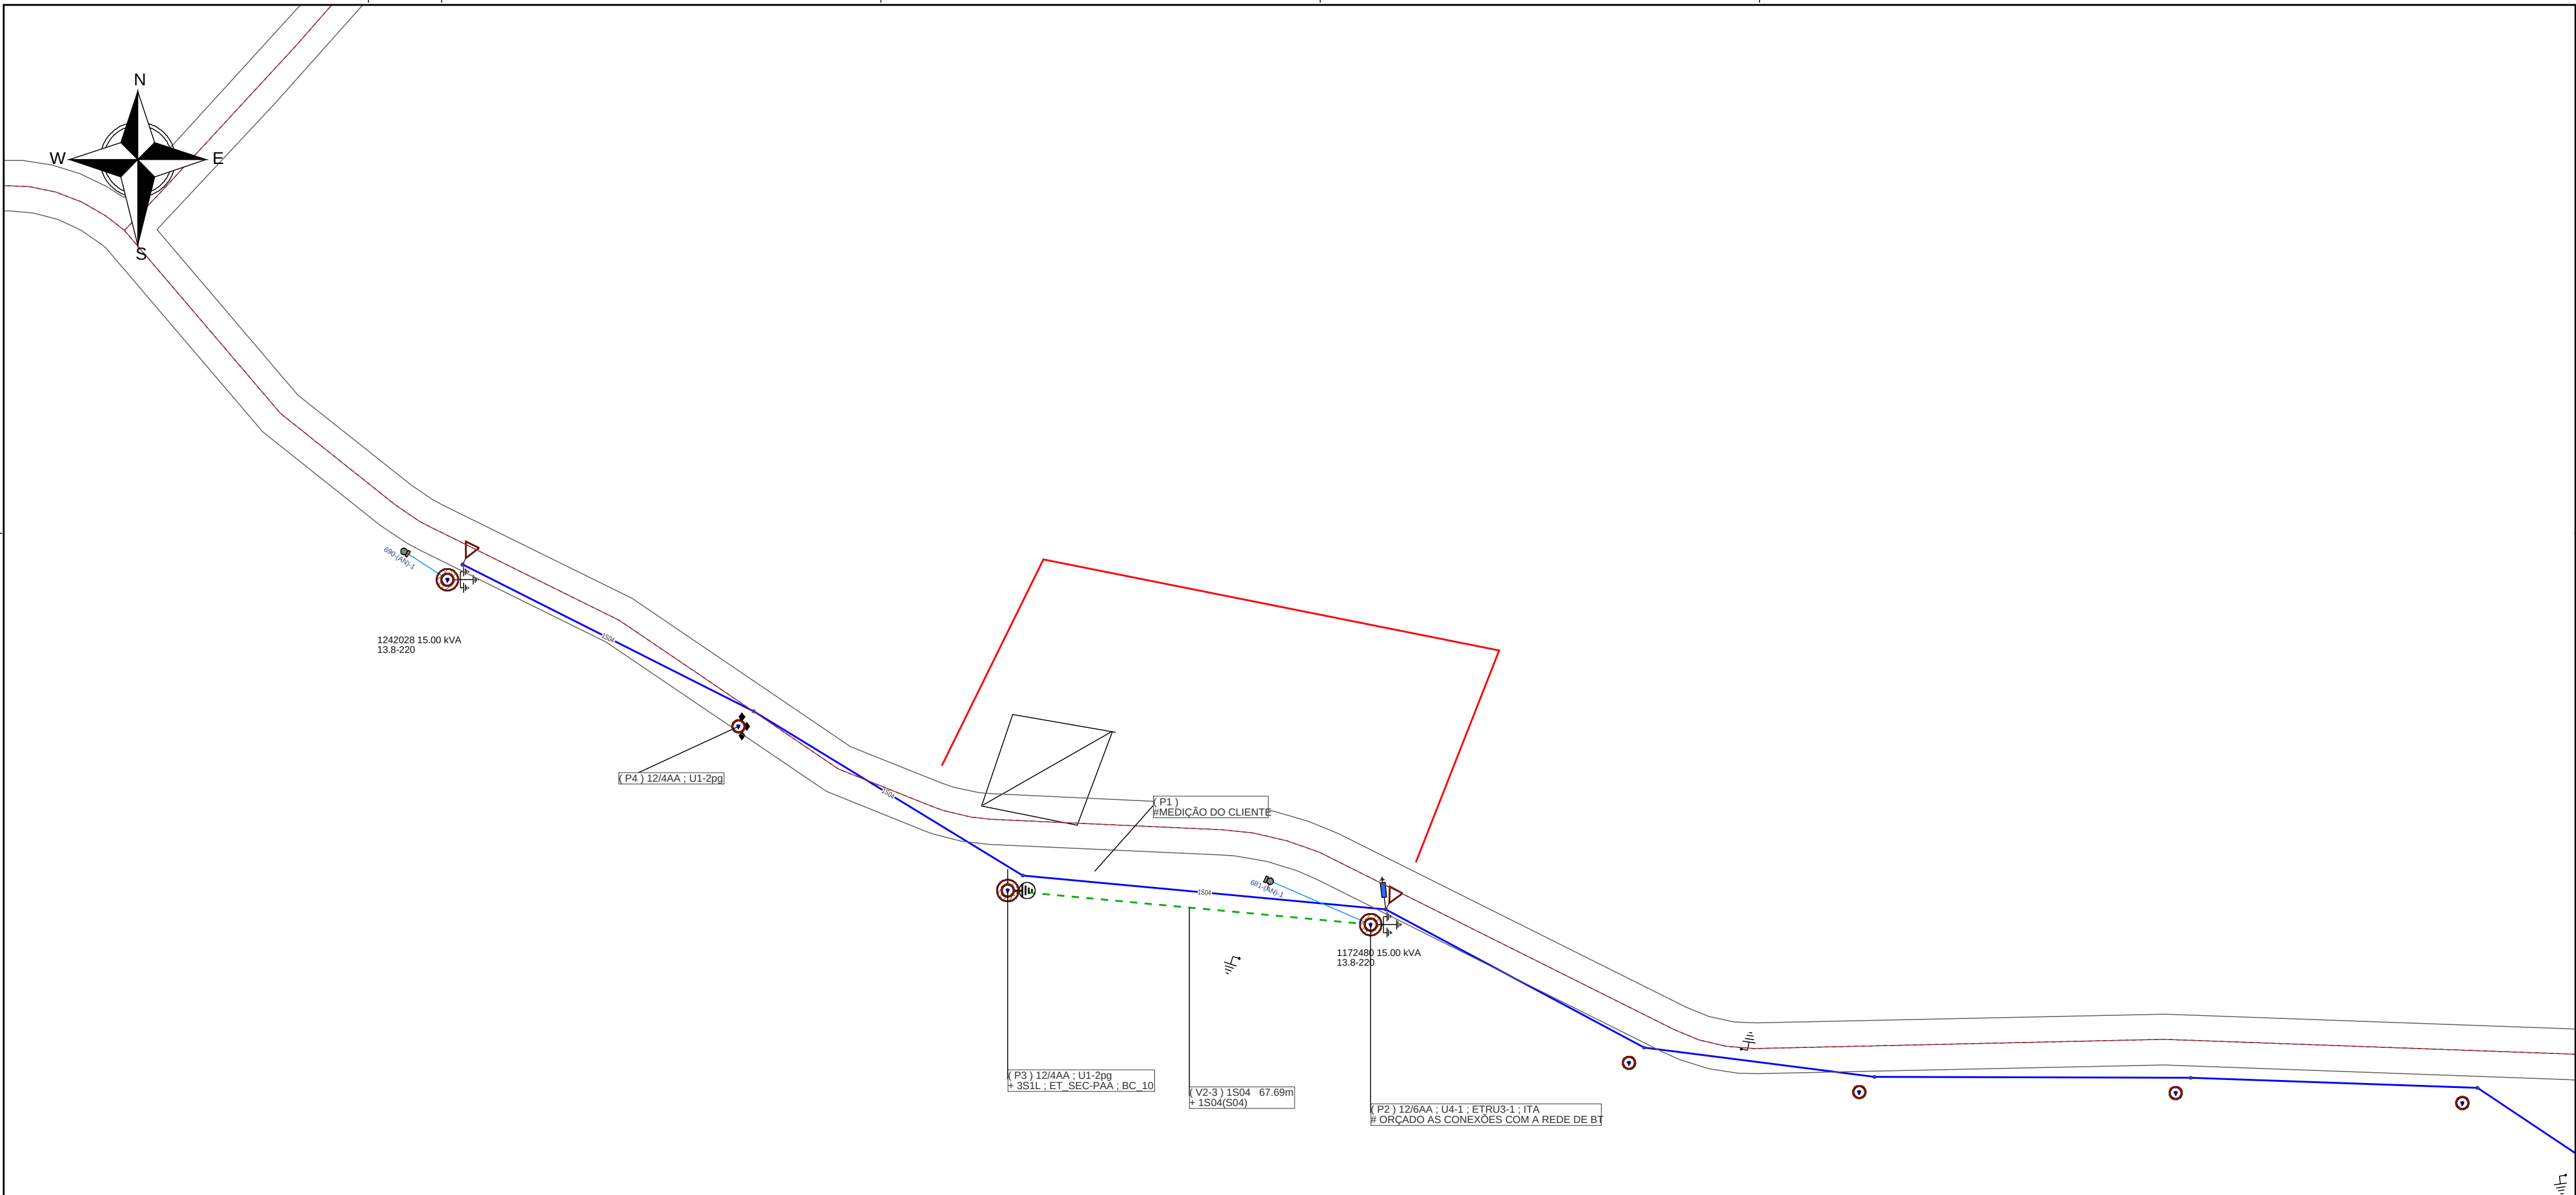

PLANO DE EXECUÇÃO					
Executar a obra seguindo todos os passos de segurança!					
Preparar a obra , Montar estrutura Para a Extensão da rede de BT					
Realizar a obra Conforme Manobra mencionado abaixo					
Alterações necessarias solicitar via D.I					
Ação	Equipamento	Número	Clientes	Duração	CHI
Desligar	Transformador	1172480	1	4	4
Linha Viva?		Não	CHI TOTAL		4
○ Poste novo a ser instalado (quando indicado em planta)					

FeedBack Para Fábrica de Projetos

Planeje
Use
Teste
Sinalize
Aterre

Diego Silva
DIEGO RODRIGUES SILVA
Gerência de Processos de Obras e Manuntenção | DROP
Técnico de Análise e Projetos
CFT: 03866285051

Gerência de Obras e Manutenção

Município: Caxias do Sul

Cliente: VALTER VILLA

Obra: LIGAÇÃO NOVA BT - RURAL

Endereço: EST RIO BRANCO 682 95143-000 CAXIAS DO SUL BR RS

Responsável Técnico: Eng. Ederson Paulo Vogel CREA: RS135794 ART: 10911826	Escala: 1:850 Classe de isolamento: 15kV Projetista: Diego Rodrigues	Data: 12/02/2026 AL: SMC13 Projeto: 000007980404	Nota: 300001113603 Folha 1 Levantador ADELAR FERREIRA
---	--	--	---