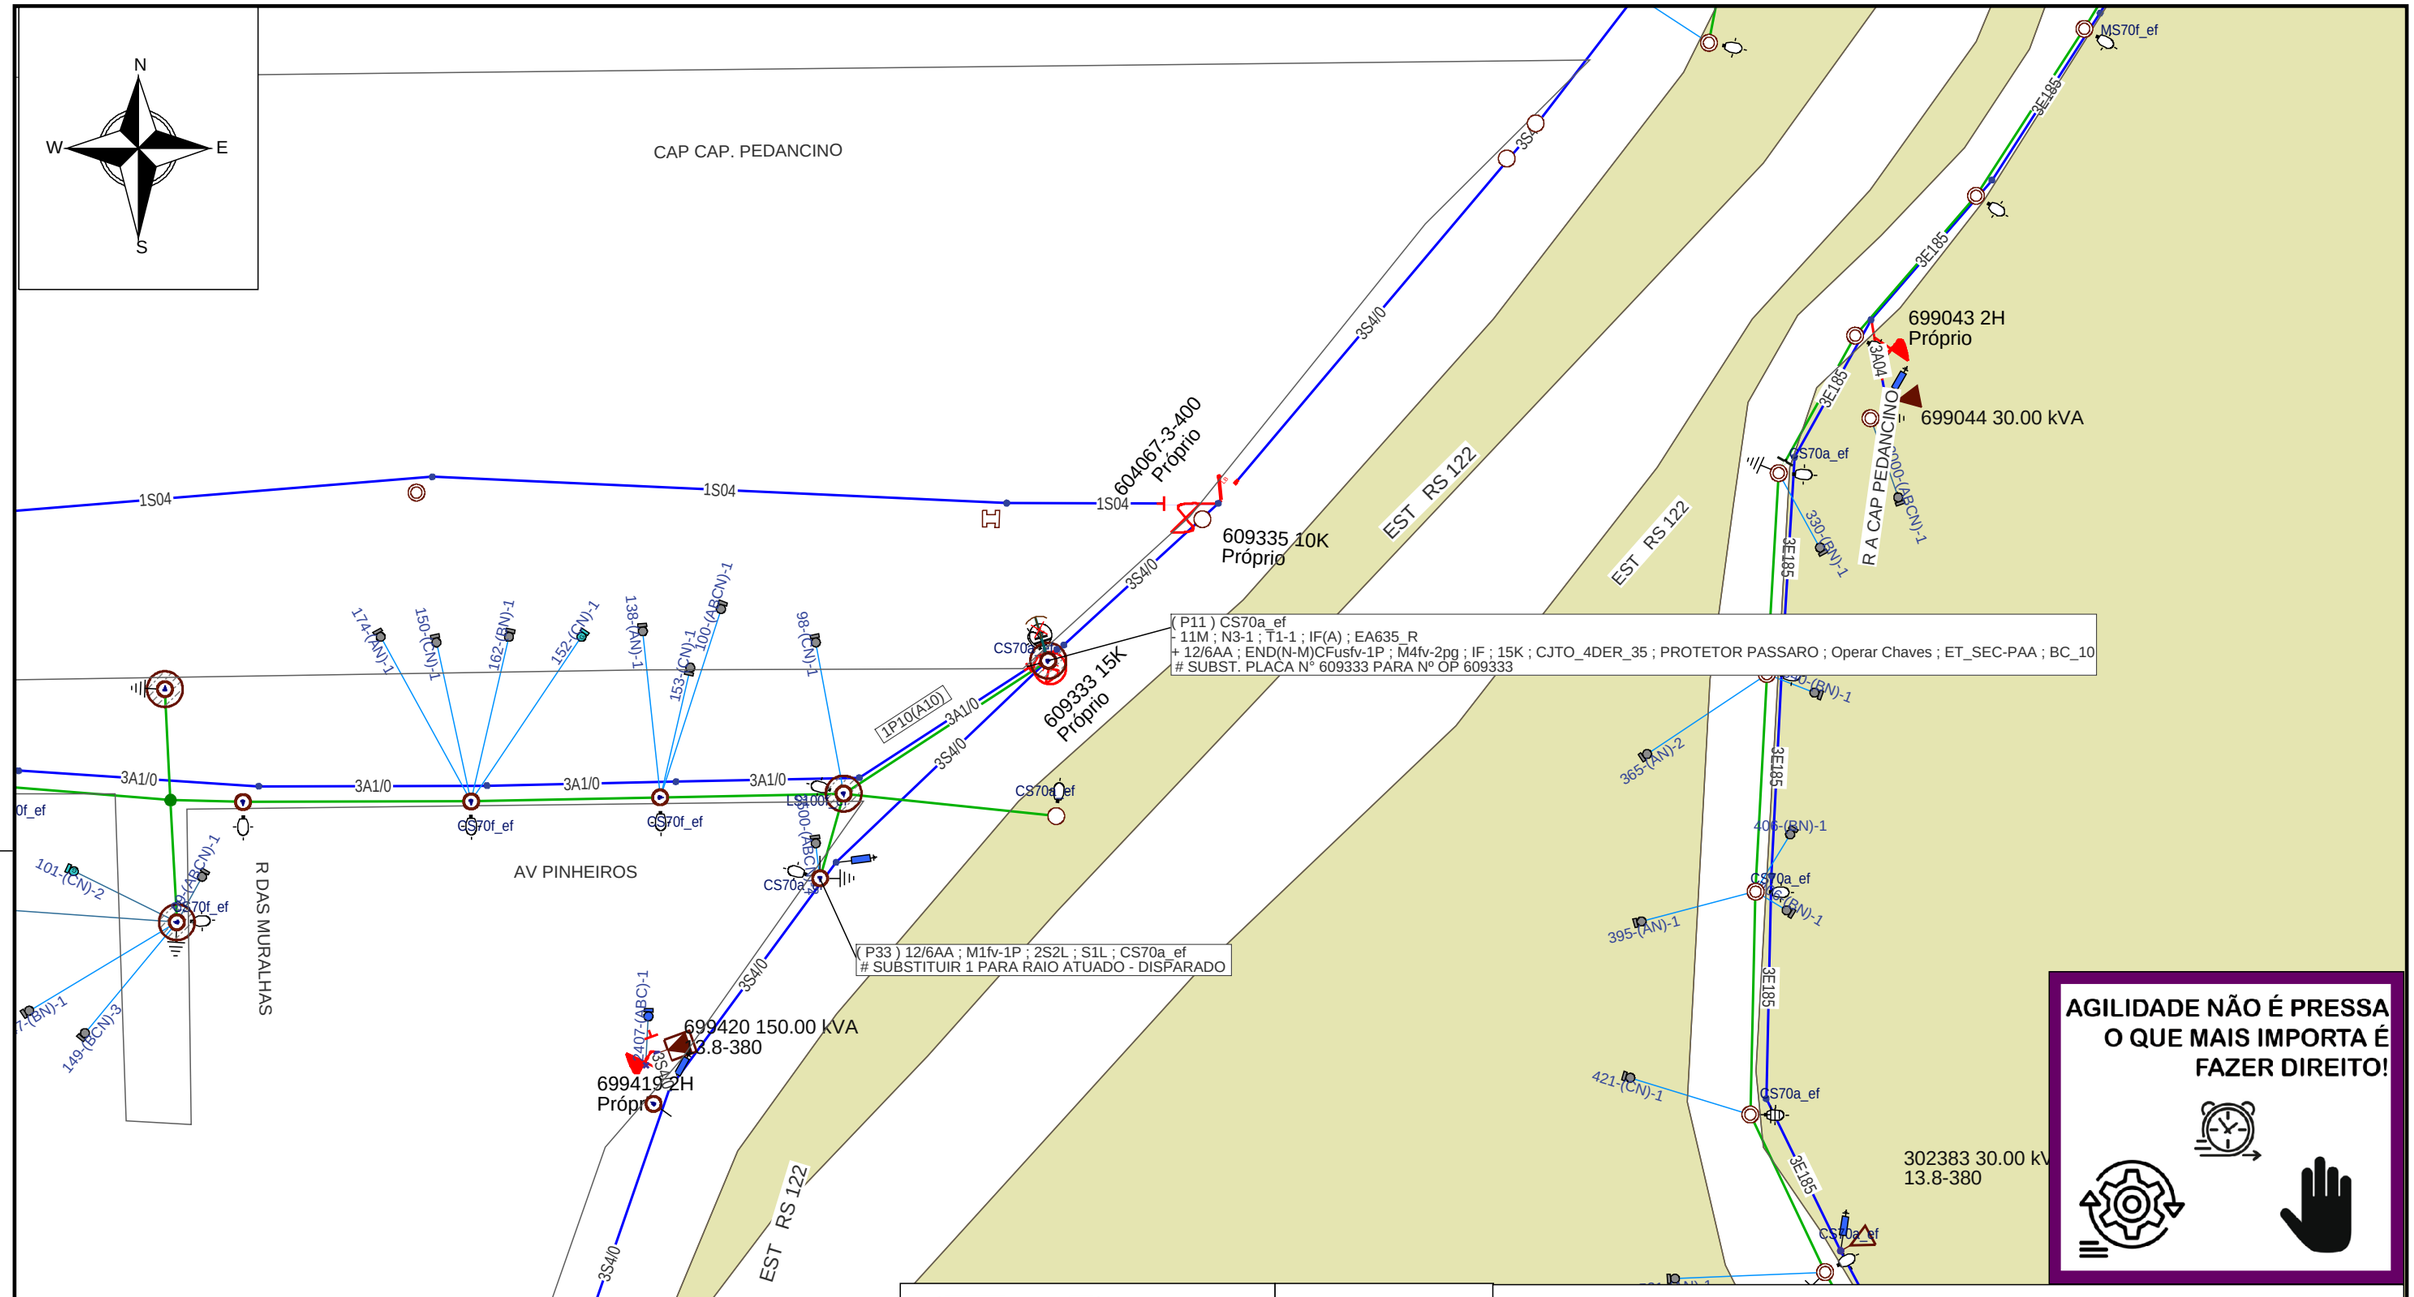

PLANO DE EXECUÇÃO

Deslocar equipe LV para trocar postes de madeira, e numerar posto, conforme previsto no projeto.

Se possível, na mesma programação executar a nota 4934785.

Ação	Equipamento	Número	Clientes	Duração	CHI
Linha Viva?		Sim	CHI TOTAL		0

◯ Poste novo a ser instalado (quando indicado em planta)

FeedBack Para Fábrica de Projetos

Planeje
Use
Teste
Sinalize
Aterre

Jorlene Viviane G. Rechene
Gerência de Processos de Obras e Manutenção | DROP
Técnica de Análise e Projetos
CFT: 00422447226

CPFL ENERGIA

Gerência de Obras e Manutenção

Município: Caxias do Sul

Cliente: RGE SUL DISTRIBUIDORA DE ENERGIA S/A

Obra: Caxias do Sul 2024 - Insp Visual de Rede

Endereço: EST RS 122 PARA F CUNHA, 3500. CAP PEDANCINO - CAXIAS DO SUL

Responsável Técnico:
Eng. Ederson Paulo Vogel
CREA: RS135794 ART: 10911826

	Escala: 1:1100	Data: 25/02/2024	Nota: 000006052567
	Classe de isolação: 15kV	AL: KCE16	Folha 1
	Projetista: Jorlene Viviane	Projeto: 000007331987	Levantador: Reinholdo