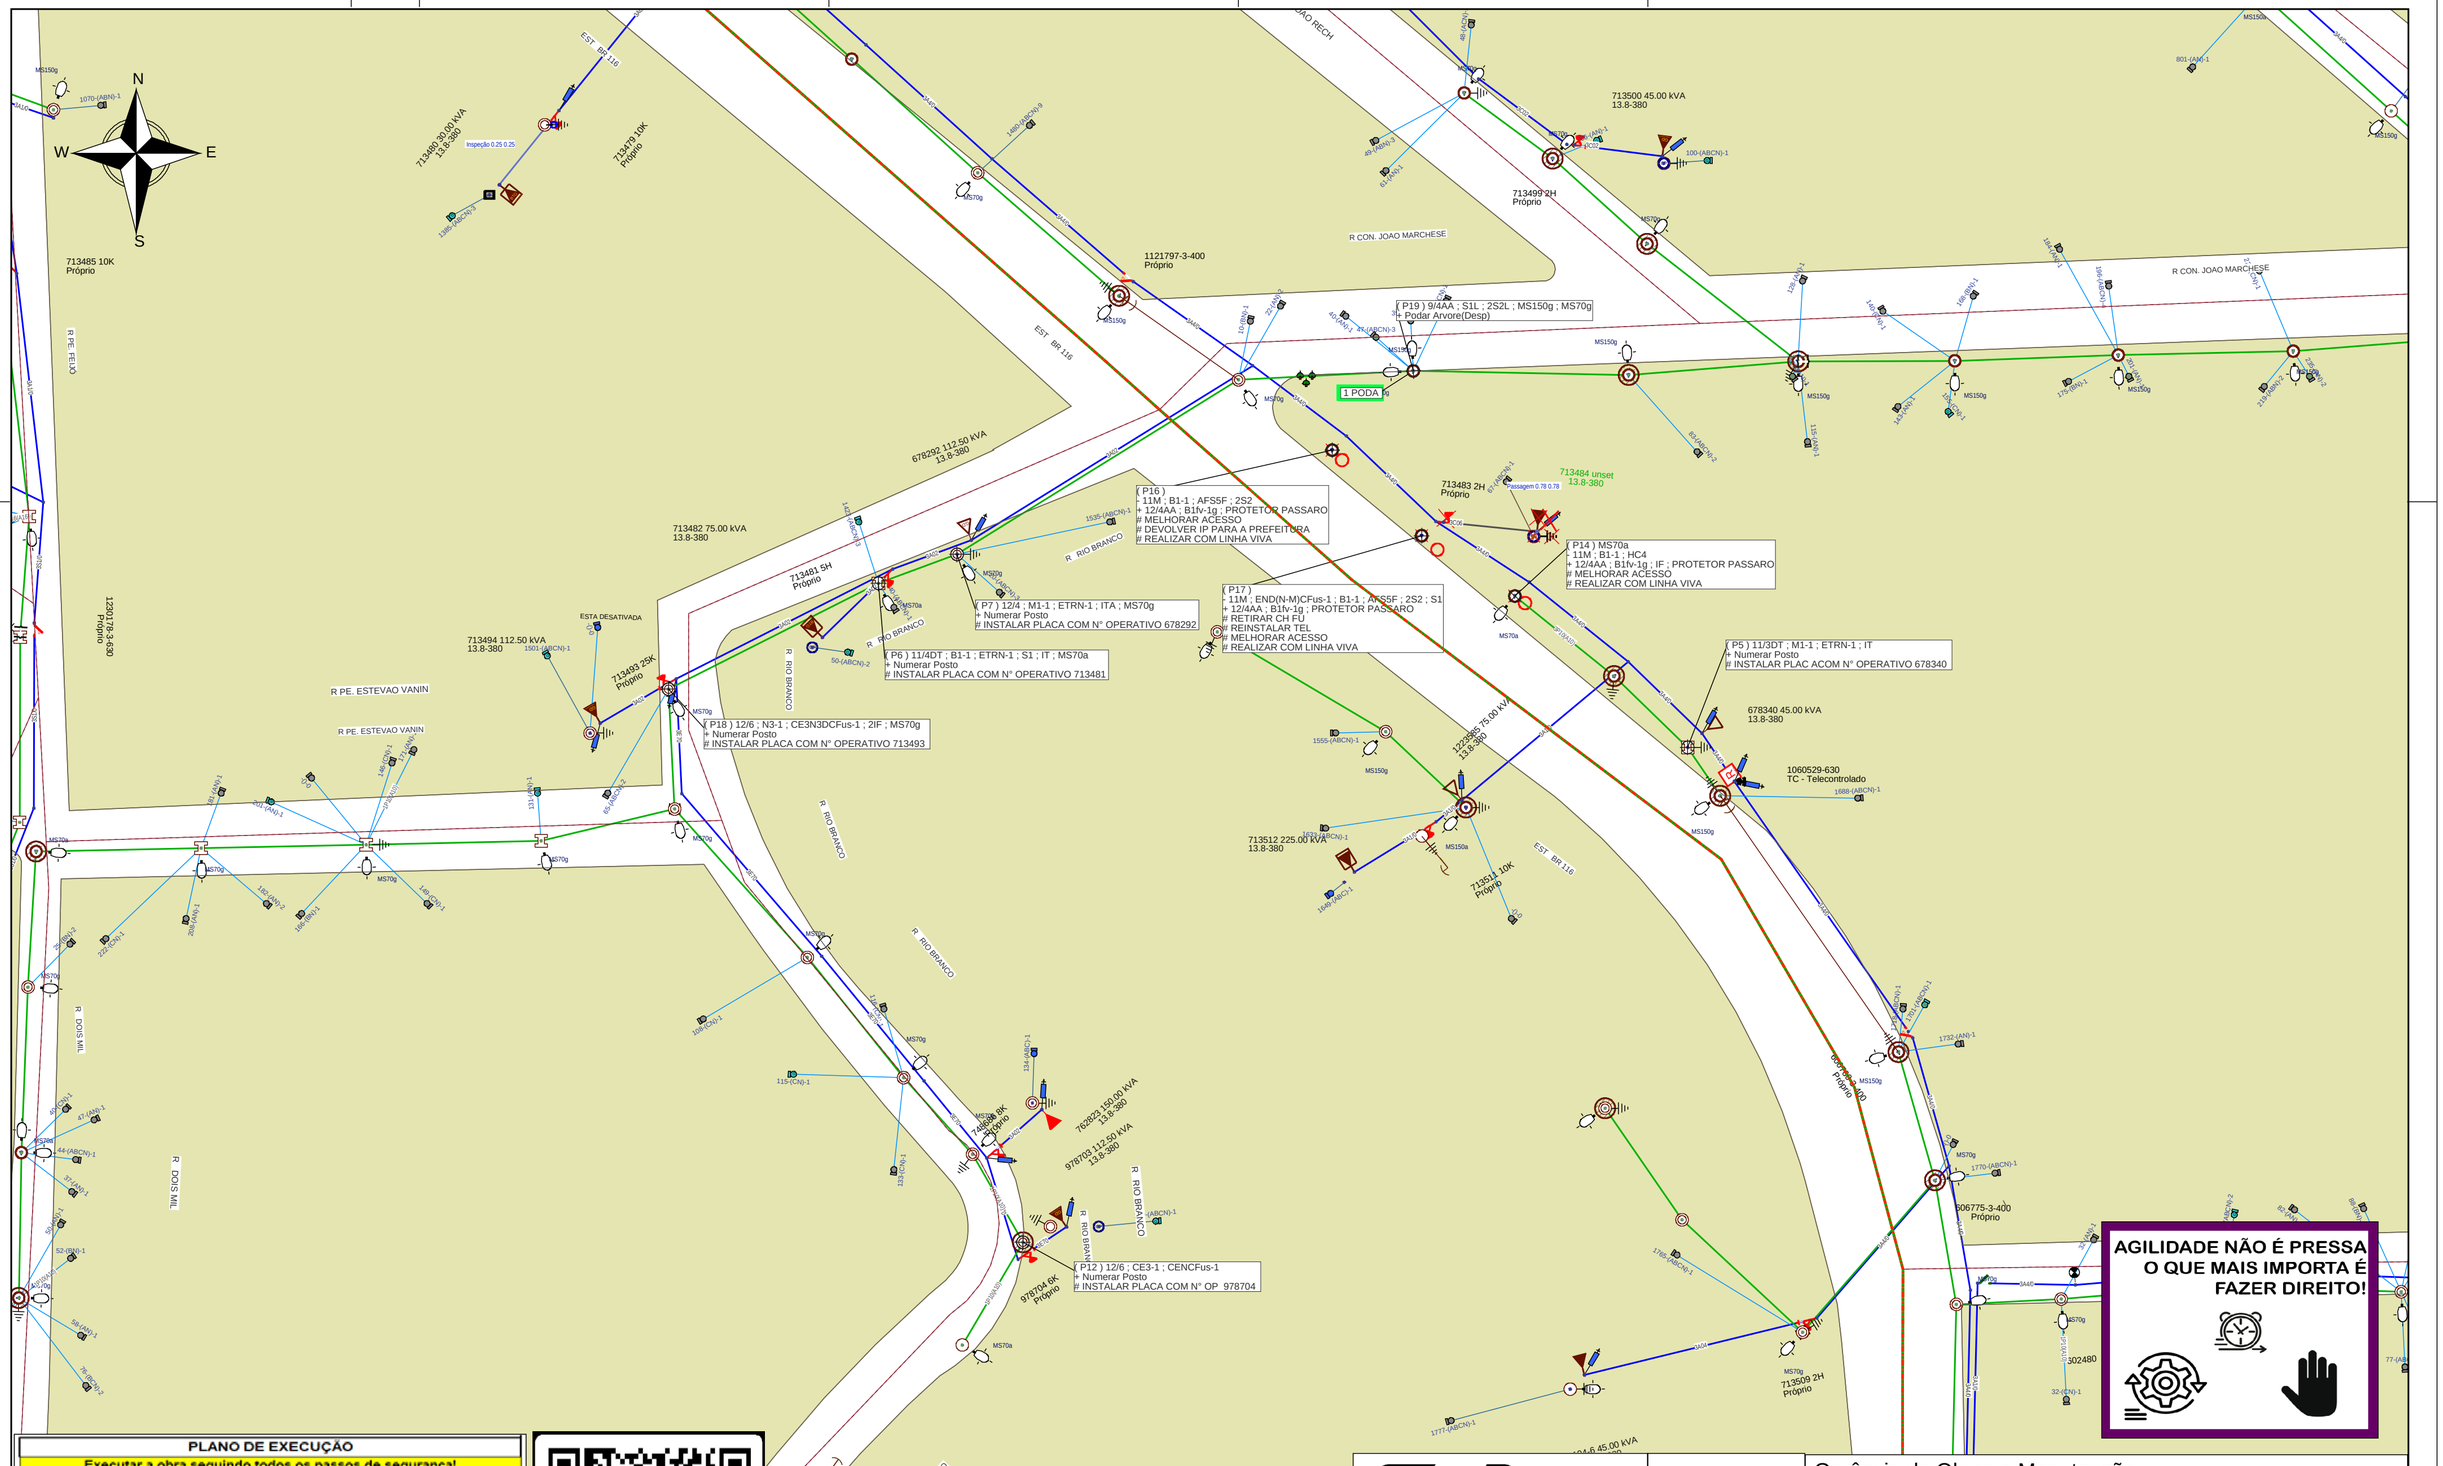

PLANO DE EXECUÇÃO

Executar a obra seguindo todos os passos de segurança!

Substituir postes,realizar podas.

Executar conforme projetado, alterações solicitar via D.I

Ação	Equipamento	Número	Clientes	Duração	CHI
Linha Viva?		Sim	CHI TOTAL		0

Poste novo a ser instalado (quando indicado em planta)

FeedBack Para Fábrica de Projetos

Planeje
Use
Teste
Sinalize
Aterre

Leticia Laxes Gracioli

Leticia Laxes Gracioli
Gerência de Processos de Obras e Manuntenção | DROP
Técnico de Análise e Projetos
CFT: 03573031056

CPFL ENERGIA

Gerência de Obras e Manutenção

Município: São Marcos

Cliente: RGE SUL DISTRIBUIDORA DE ENERGIA S/A

Obra: Caxias do Sul 2025 - Insp Visual de Rede

Endereço: RDV BR 116, 1688 - CENTRO - SAO MARCOS/RS

Responsável Técnico:
Eng. Ederson Paulo Vogel
CREA: RS135794 ART: 10911826

Escala: 1:850	Data: 01/10/2024	Nota: 000006387498
Classe de isolação: 15kV	AL: SMC12	Folha 1
Projetista: Leticia Laxes	Projeto: 000007614633	Levantador: Alessandro Severo