


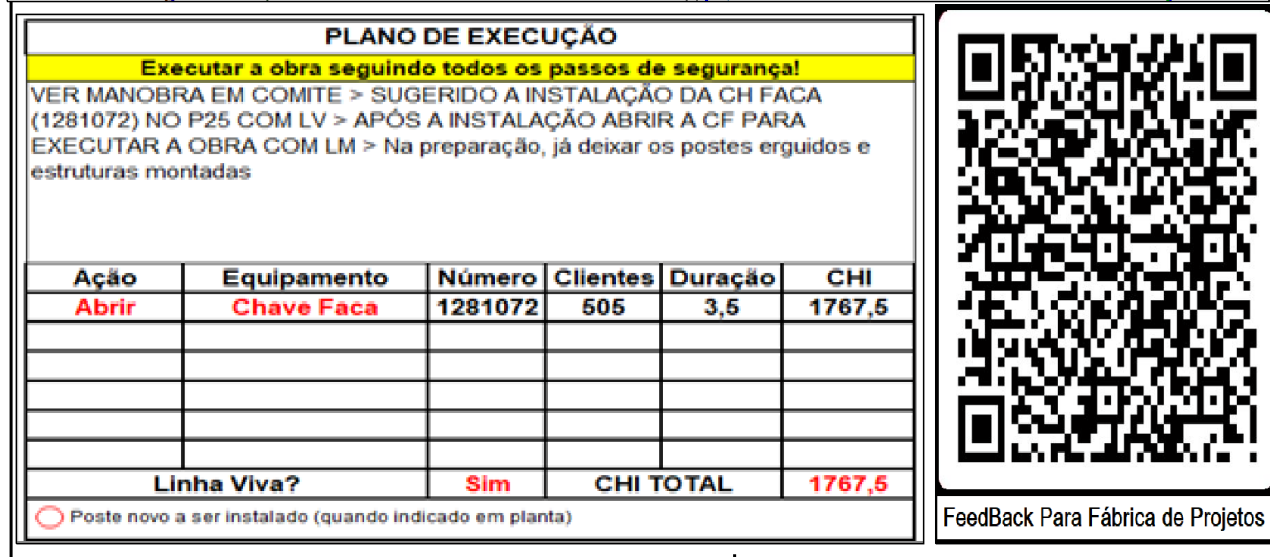
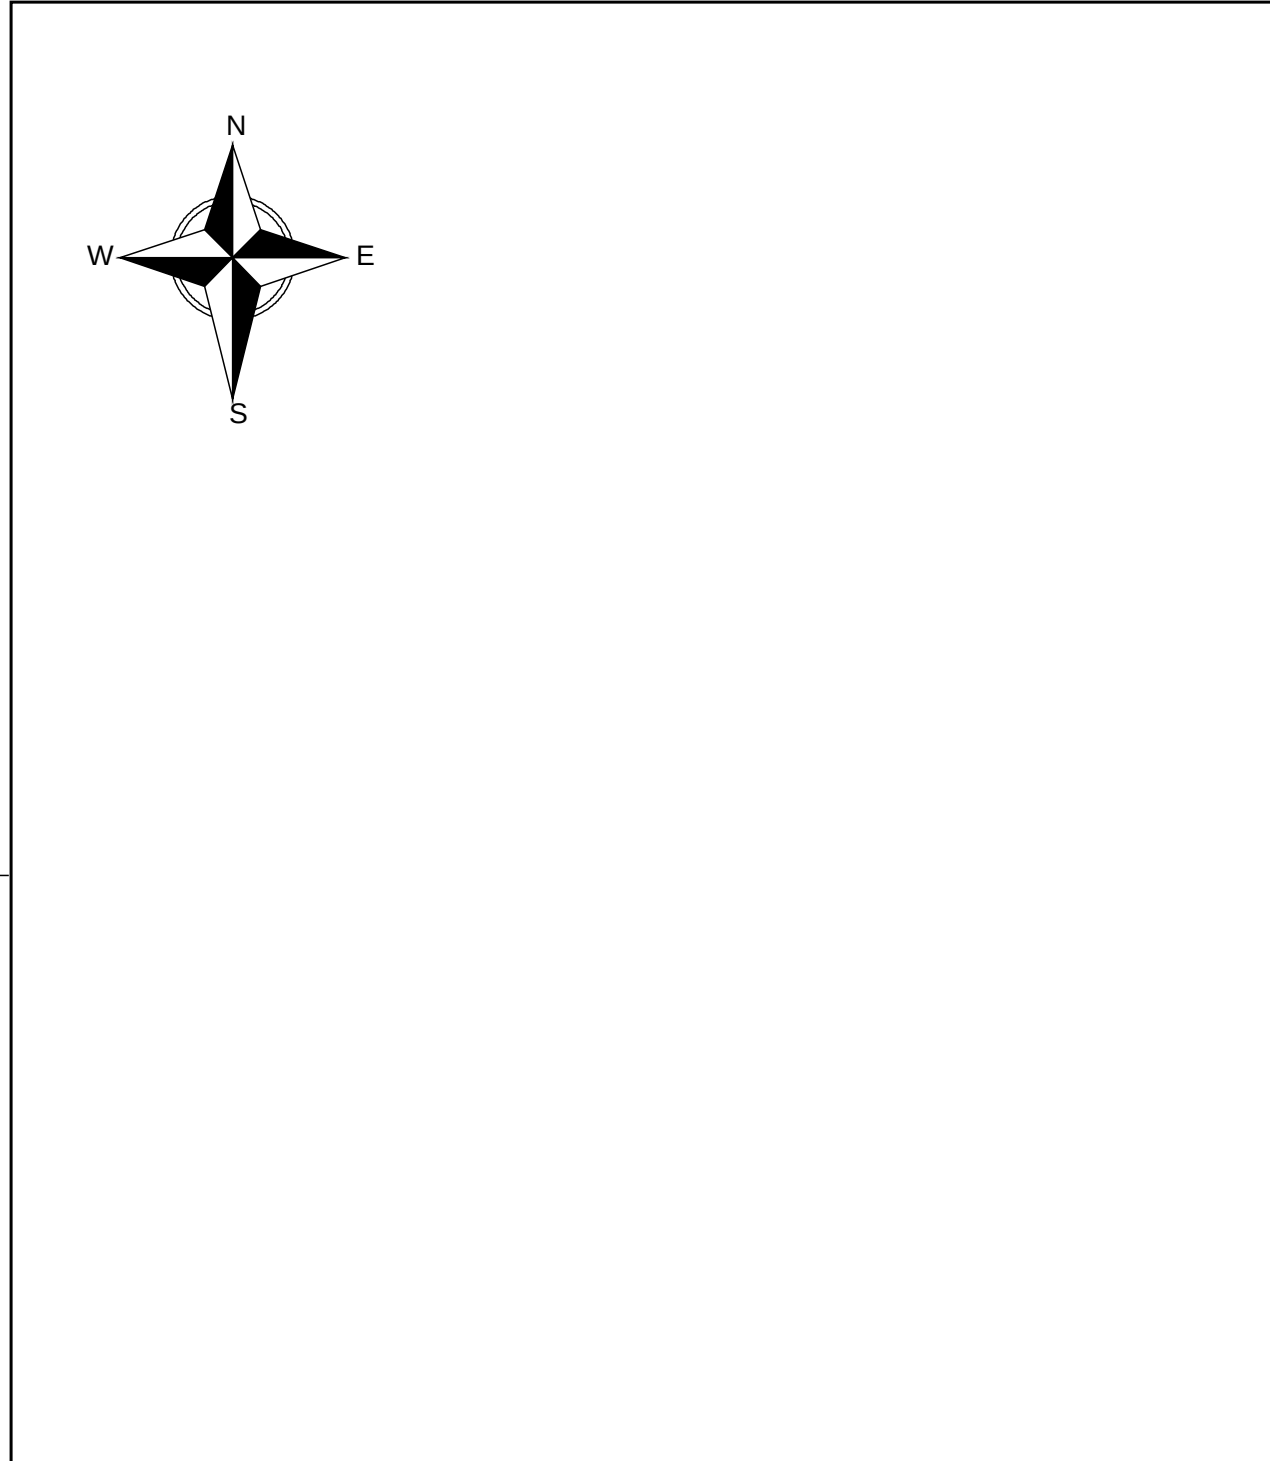
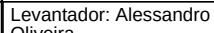
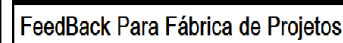
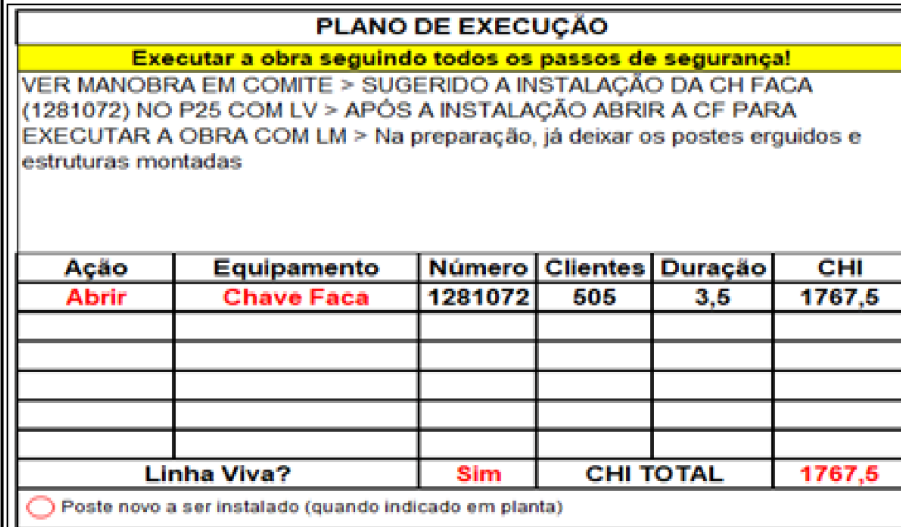
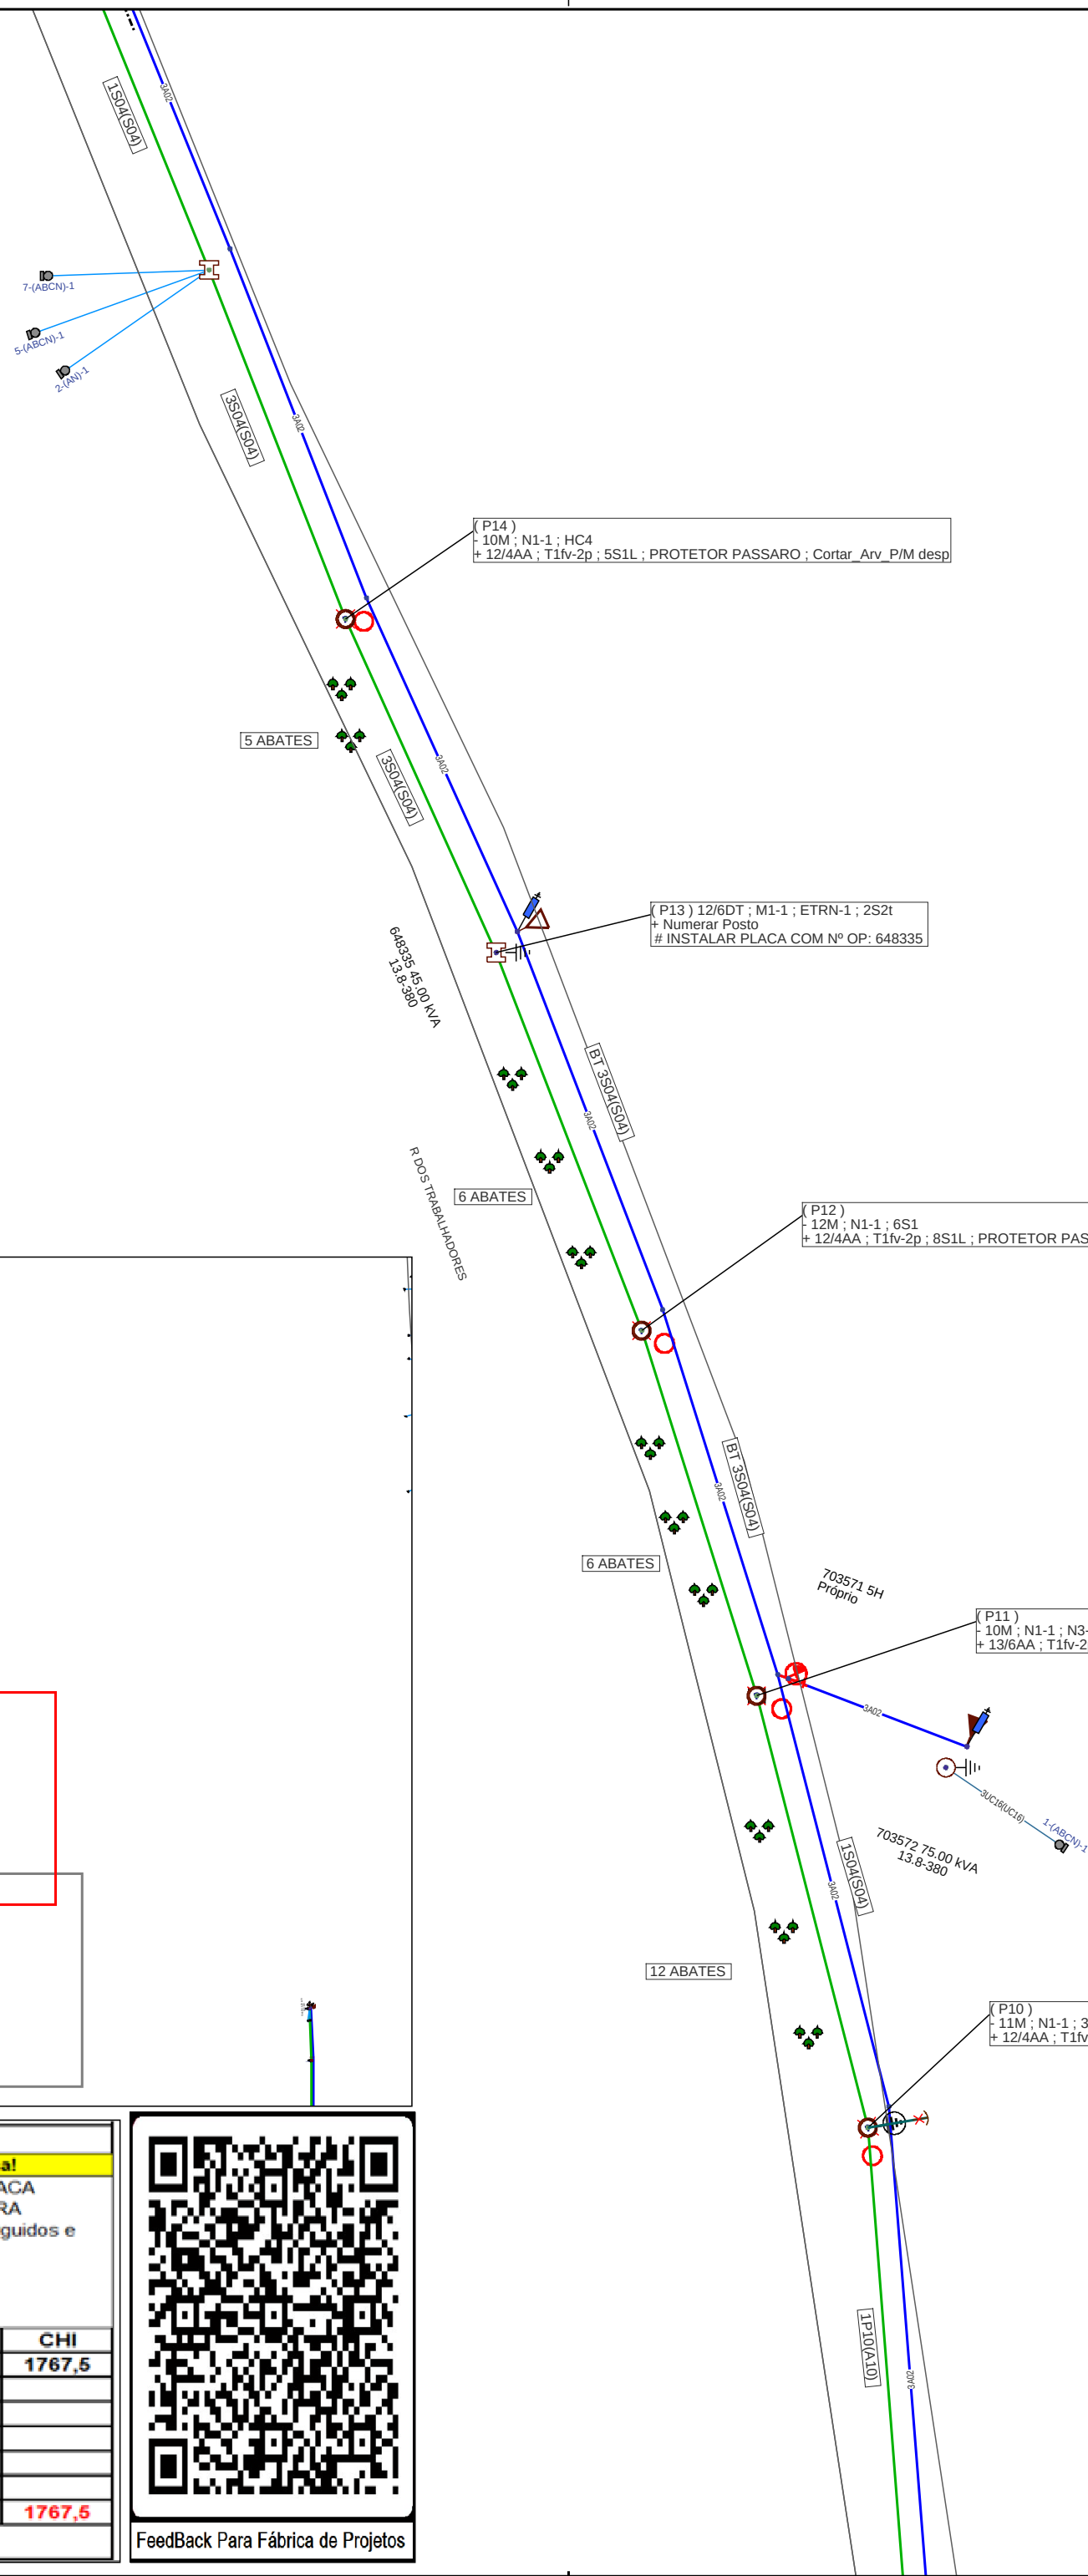


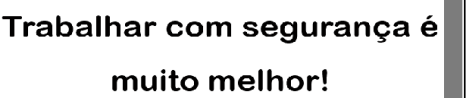

**Trabalhar com segurança é
muito melhor!**

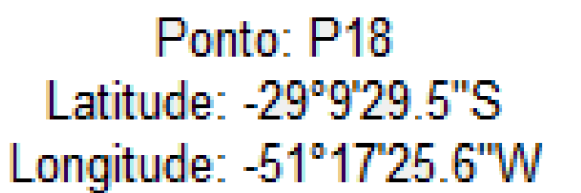

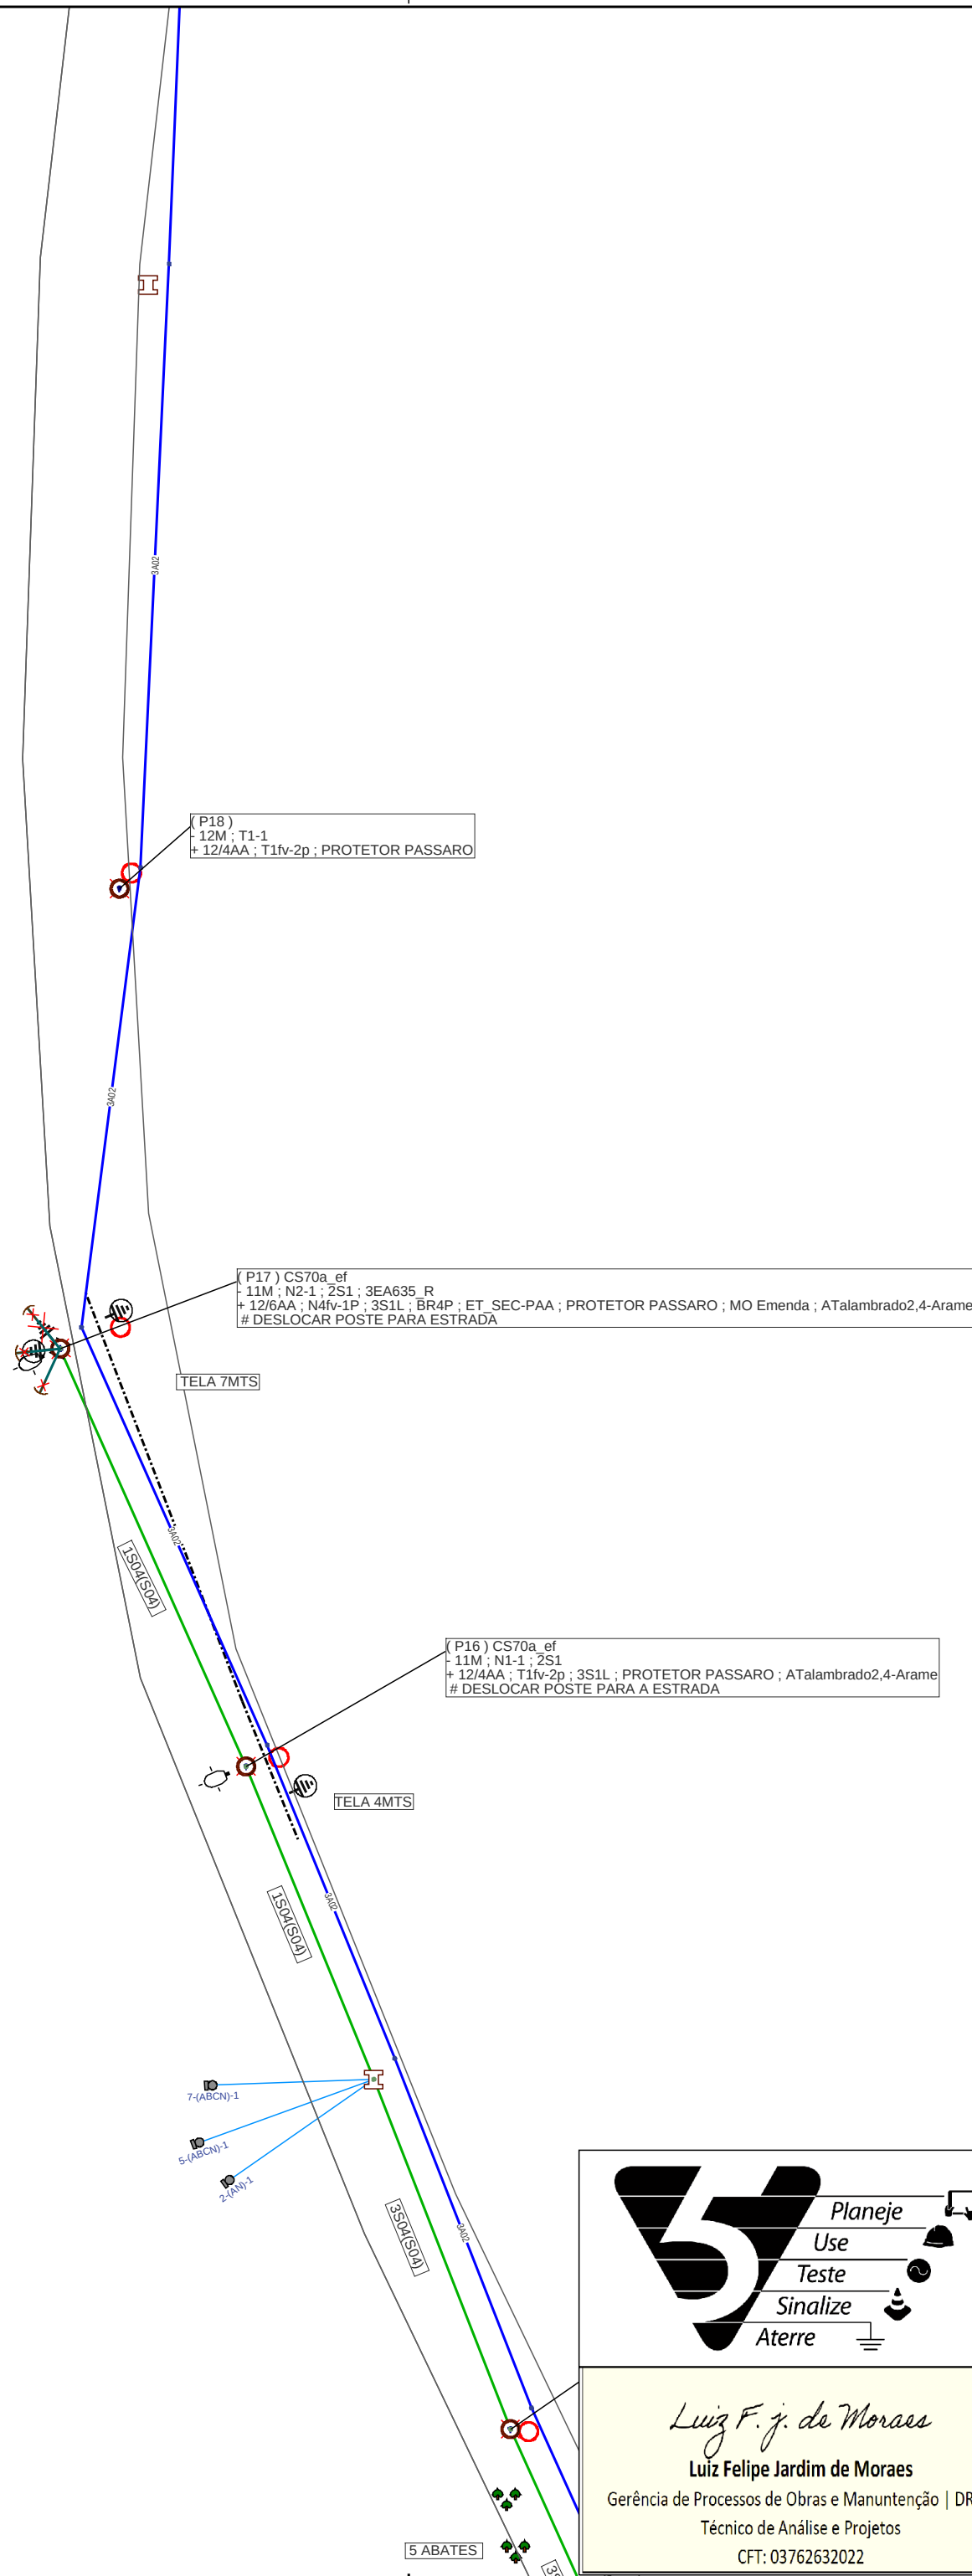




FeedBack Para Fábrica de Projetos



Responsável Técnico:

 Eng. Ederson Paulo Vogel
 CREA: RS135794 ART: 10911826

Levantador: Alessandro
Oliveira

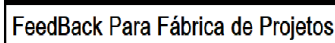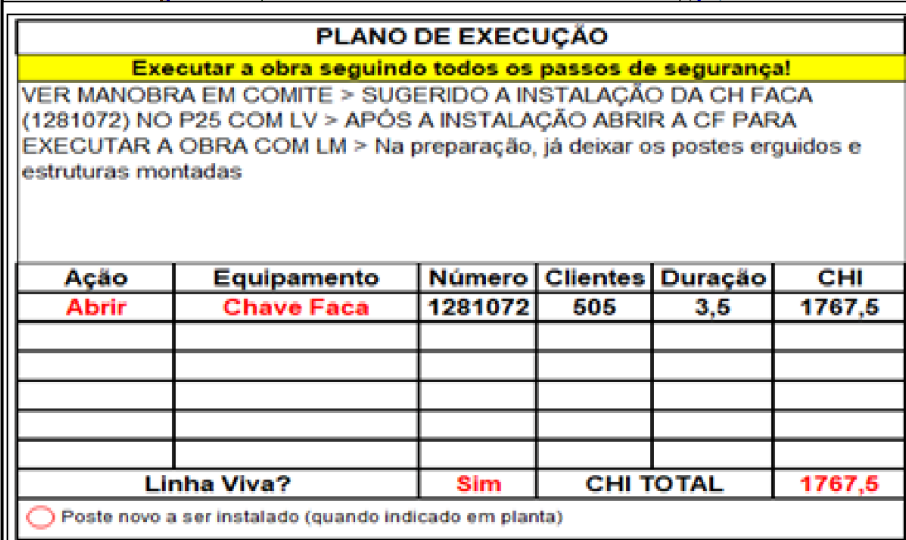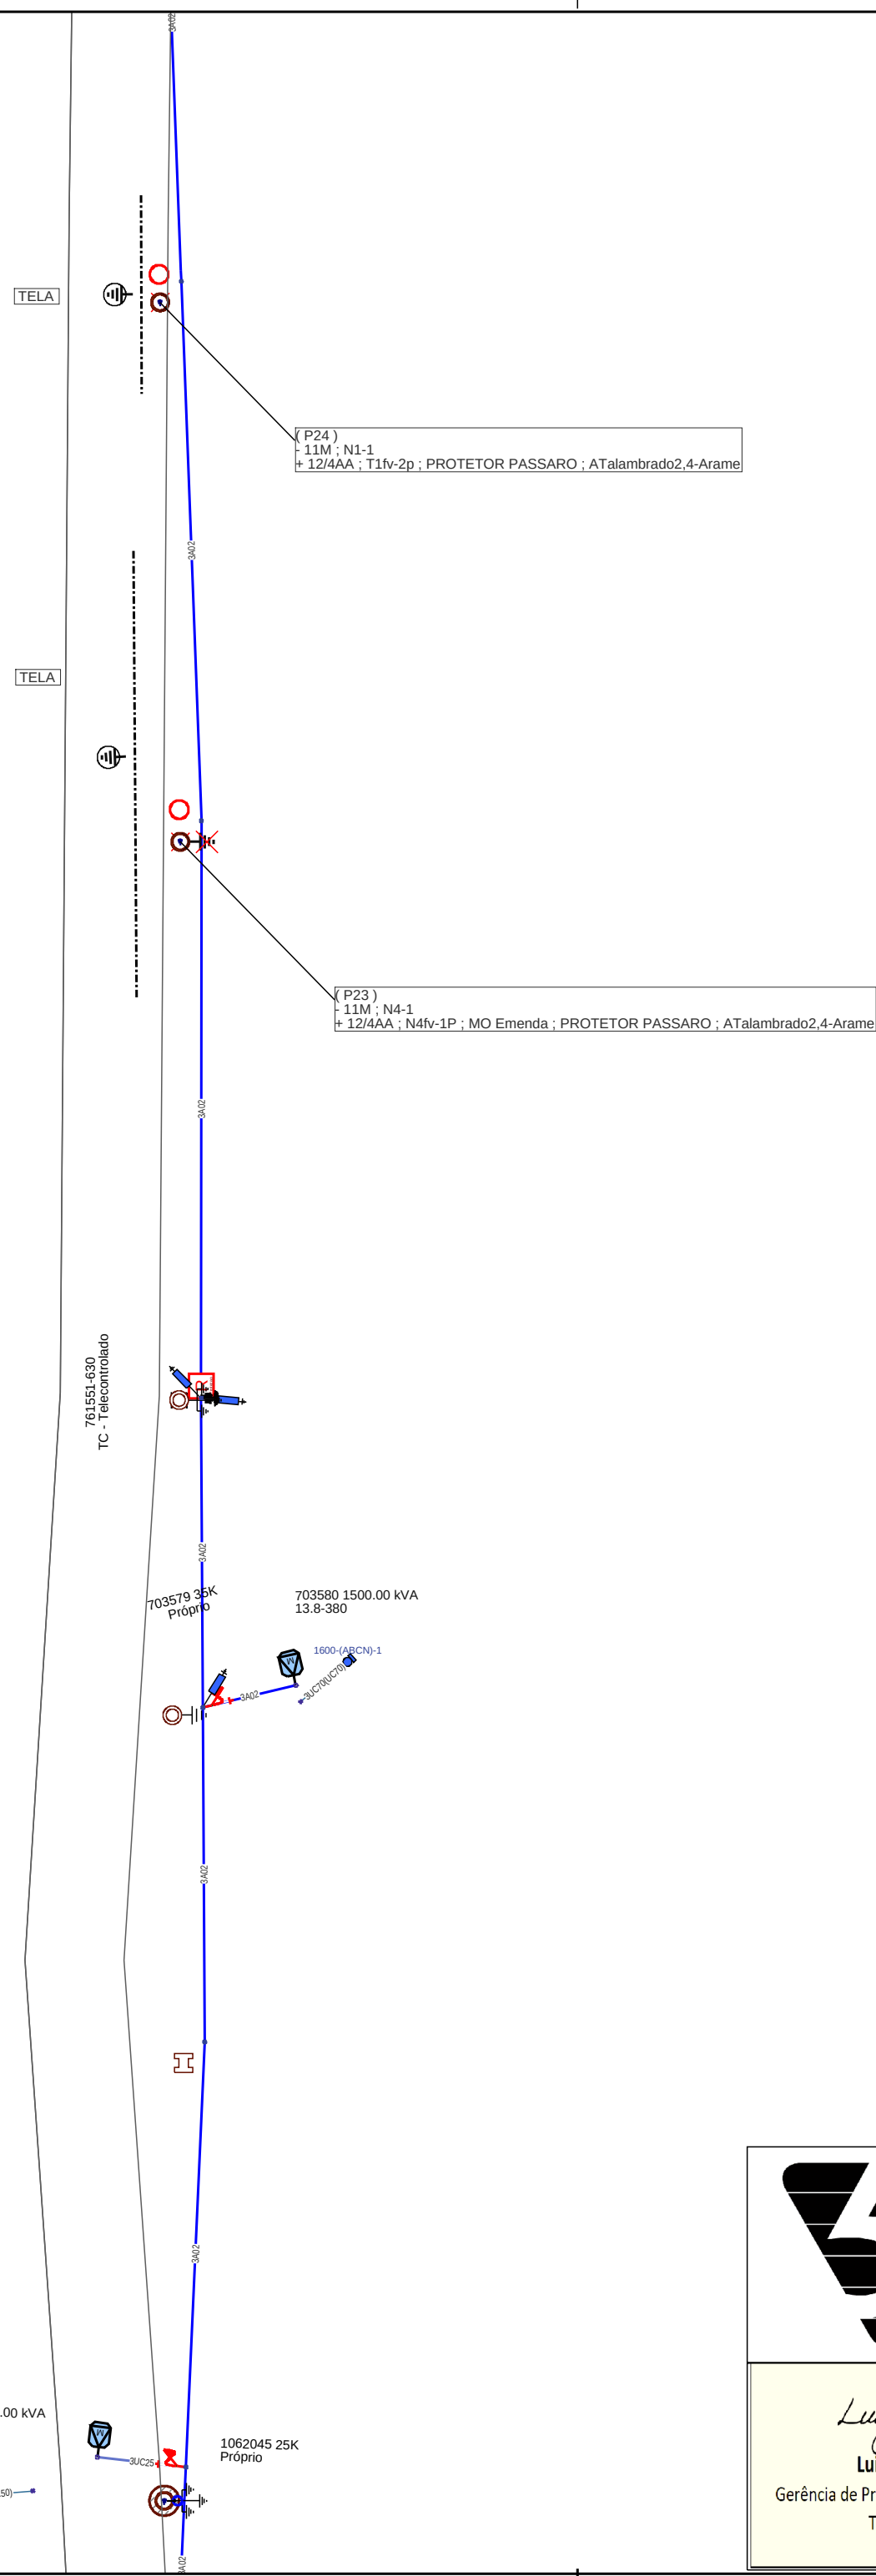

	Gerência de Obras e Manutenção		
	Município: Caxias do Sul		
Cliente: RGE SUL DISTRIBUIDORA DE ENERGIA S/A			
Obra: Caxias do Sul 2025 - Insp Visual de Rede			
Endereço: EST VRS 864 - 1600, MATO PERSO, FARROUPILHA			
Responsável Técnico:  Eng. Ederson Paulo Vogel CREA: RS135794 ART: 10911826	Escala: 1:850	Data: 01/02/2025	Nota: 000006620693
	Classe de isolamento: 15kV	AL: CXH34	Folha 4
	Projetista: Luiz Felipe	Projeto: 000007714404	Levantador: Alessandro Oliveira