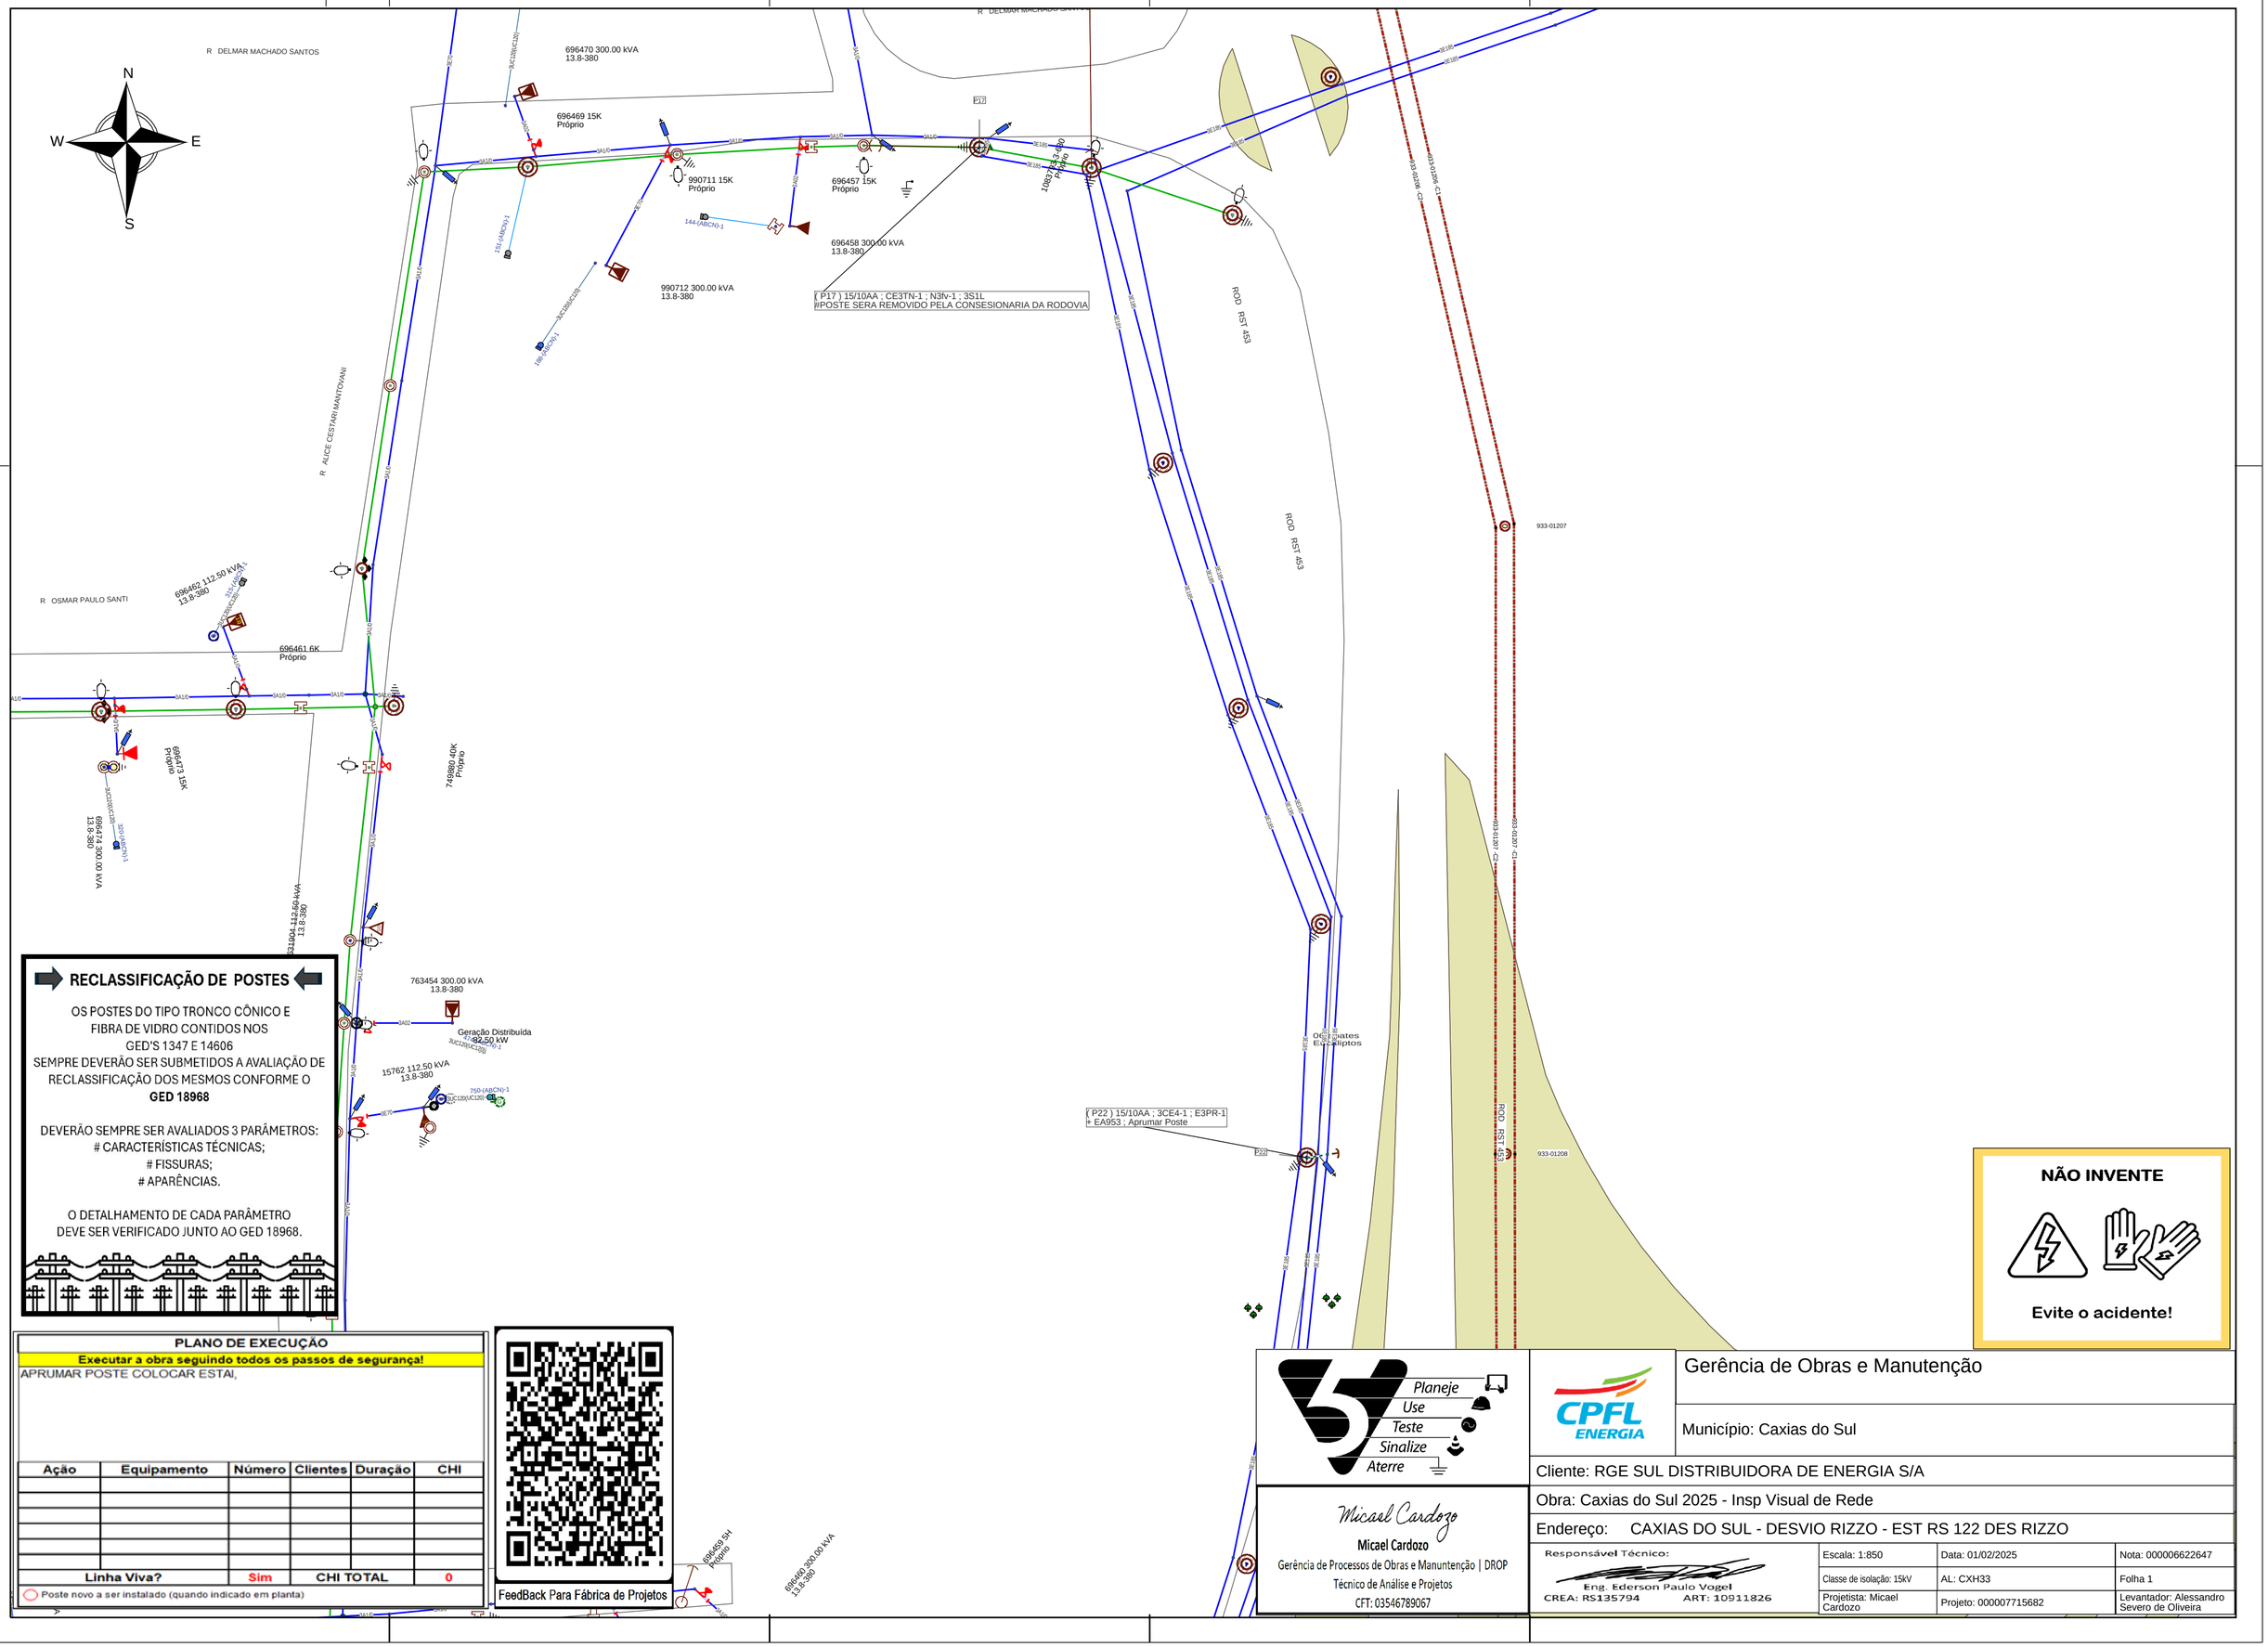

RECLASSIFICAÇÃO DE POSTES

OS POSTES DO TIPO TRONCO CÔNICO E FIBRA DE VIDRO CONTIDOS NOS GED'S 1347 E 14606 SEMPRE DEVERÃO SER SUBMETIDOS A AVALIAÇÃO DE RECLASSIFICAÇÃO DOS MESMOS CONFORME O **GED 18968**

DEVERÃO SEMPRE SER AVALIADOS 3 PARÂMETROS:
CARACTERÍSTICAS TÉCNICAS;
FISSURAS;
APARÊNCIAS.

O DETALHAMENTO DE CADA PARÂMETRO DEVE SER VERIFICADO JUNTO AO GED 18968.

NÃO INVENTE

Evite o acidente!

PLANO DE EXECUÇÃO

Executar a obra seguindo todos os passos de segurança!

APRUMAR POSTE COLOCAR ESTAI,

Ação	Equipamento	Número	Clientes	Duração	CHI
Linha Viva?		Sim	CHI TOTAL		0

Poste novo a ser instalado (quando indicado em planta)

FeedBack Para Fábrica de Projetos

Planeje
Use
Teste
Sinalize
Aterre

Micael Cardozo
Micael Cardozo
Gerência de Processos de Obras e Manuntenção | DROP
Técnico de Análise e Projetos
CFT: 03546789067

CPFL ENERGIA

Gerência de Obras e Manutenção

Município: Caxias do Sul

Cliente: RGE SUL DISTRIBUIDORA DE ENERGIA S/A

Obra: Caxias do Sul 2025 - Insp Visual de Rede

Endereço: CAXIAS DO SUL - DESVIO RIZZO - EST RS 122 DES RIZZO

Responsável Técnico:
Eng. Ederson Paulo Vogel
CREA: RS135794 ART: 10911826

Escala: 1:850	Data: 01/02/2025	Nota: 000006622647
Classe de isolação: 15kV	AL: CXH33	Folha 1
Projetista: Micael Cardozo	Projeto: 000007715682	Levantador: Alessandro Severo de Oliveira