


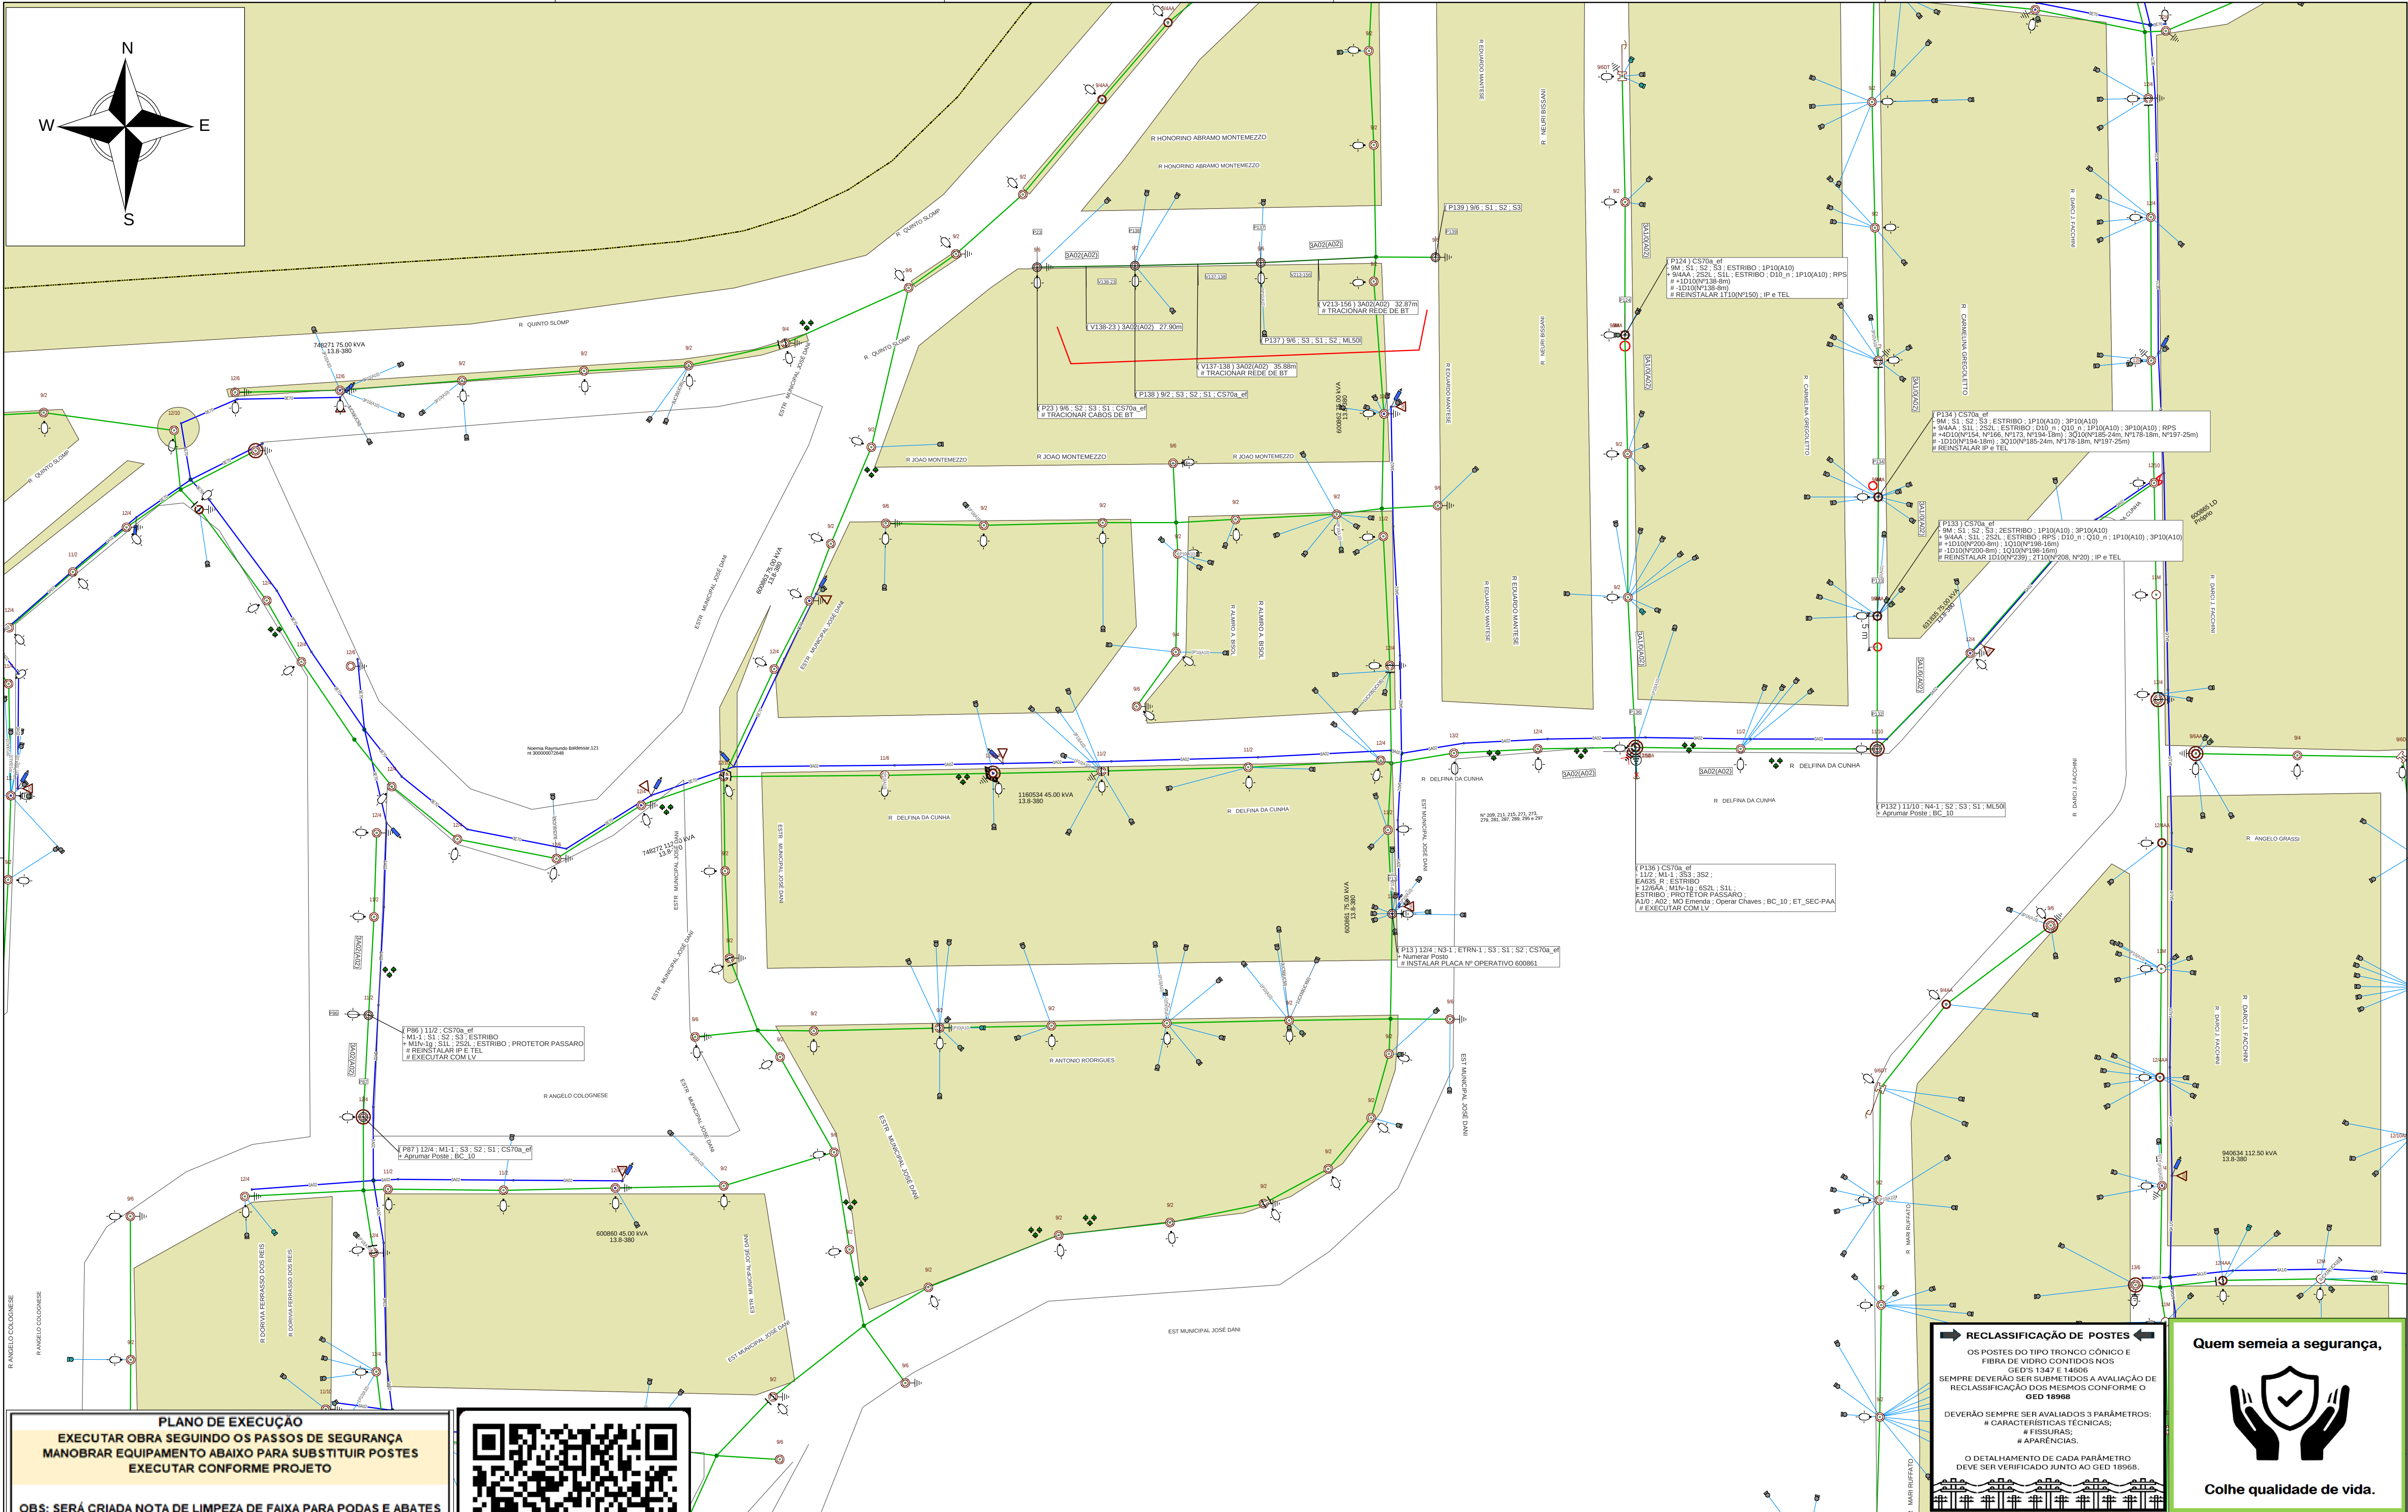

PLANO DE EXECUÇÃO
EXECUTAR OBRA SEGUINDO OS PASSOS DE SEGURANÇA
MANOBRAR EQUIPAMENTO ABAIXO PARA SUBSTITUIR POSTES
EXECUTAR CONFORME PROJETO

OBS: SERÁ CRIADA NOTA DE LIMPEZA DE FAIXA PARA PODAS E ABATES

Ação	Equipamento	Número	Clientes	Duração	CHI
Desligar	Transformador	631835	70	5	350
Desligar	Transformador	600861	105	5	525
Desligar	Transformador	600862	77	5	385
Desligar	Transformador	600860	23	5	115

Linha Viva?	Sim	CHI TOTAL	1375
-------------	-----	-----------	------

Poste novo a ser instalado (quando indicado em planta)

FeedBack Para Fábrica de Projetos

Jailson Cardoso Kessner
Jailson Cardoso Kessner
Gerência de Processos de Obras e Manutenção | DROP
Técnico de Análise e Projetos
CFT: 01389333086

Planeje
Use
Teste
Sinalize
Aterre

Gerência de Serviços de Rede: SERRA

Município: Caxias do Sul

Cliente: RGE SUL DISTRIBUIDORA DE ENERGIA S.A

Obra: Caxias do Sul 2025 - Insp Visual de Rede

Endereço: R NEURI BISSANI Nº 246

Responsável Técnico:
Eng. Ederson Paulo Vogel
CREA: RS195794

Escala: 1:850
Classe de Isolção: 15kV
Projeto: 00000737300

Data: 01/03/2025
AL: CXH44
Projeto: 00000737300

Nota: 00006722811
Folha 1
Levanteador: REINHOLDO BRULINER