


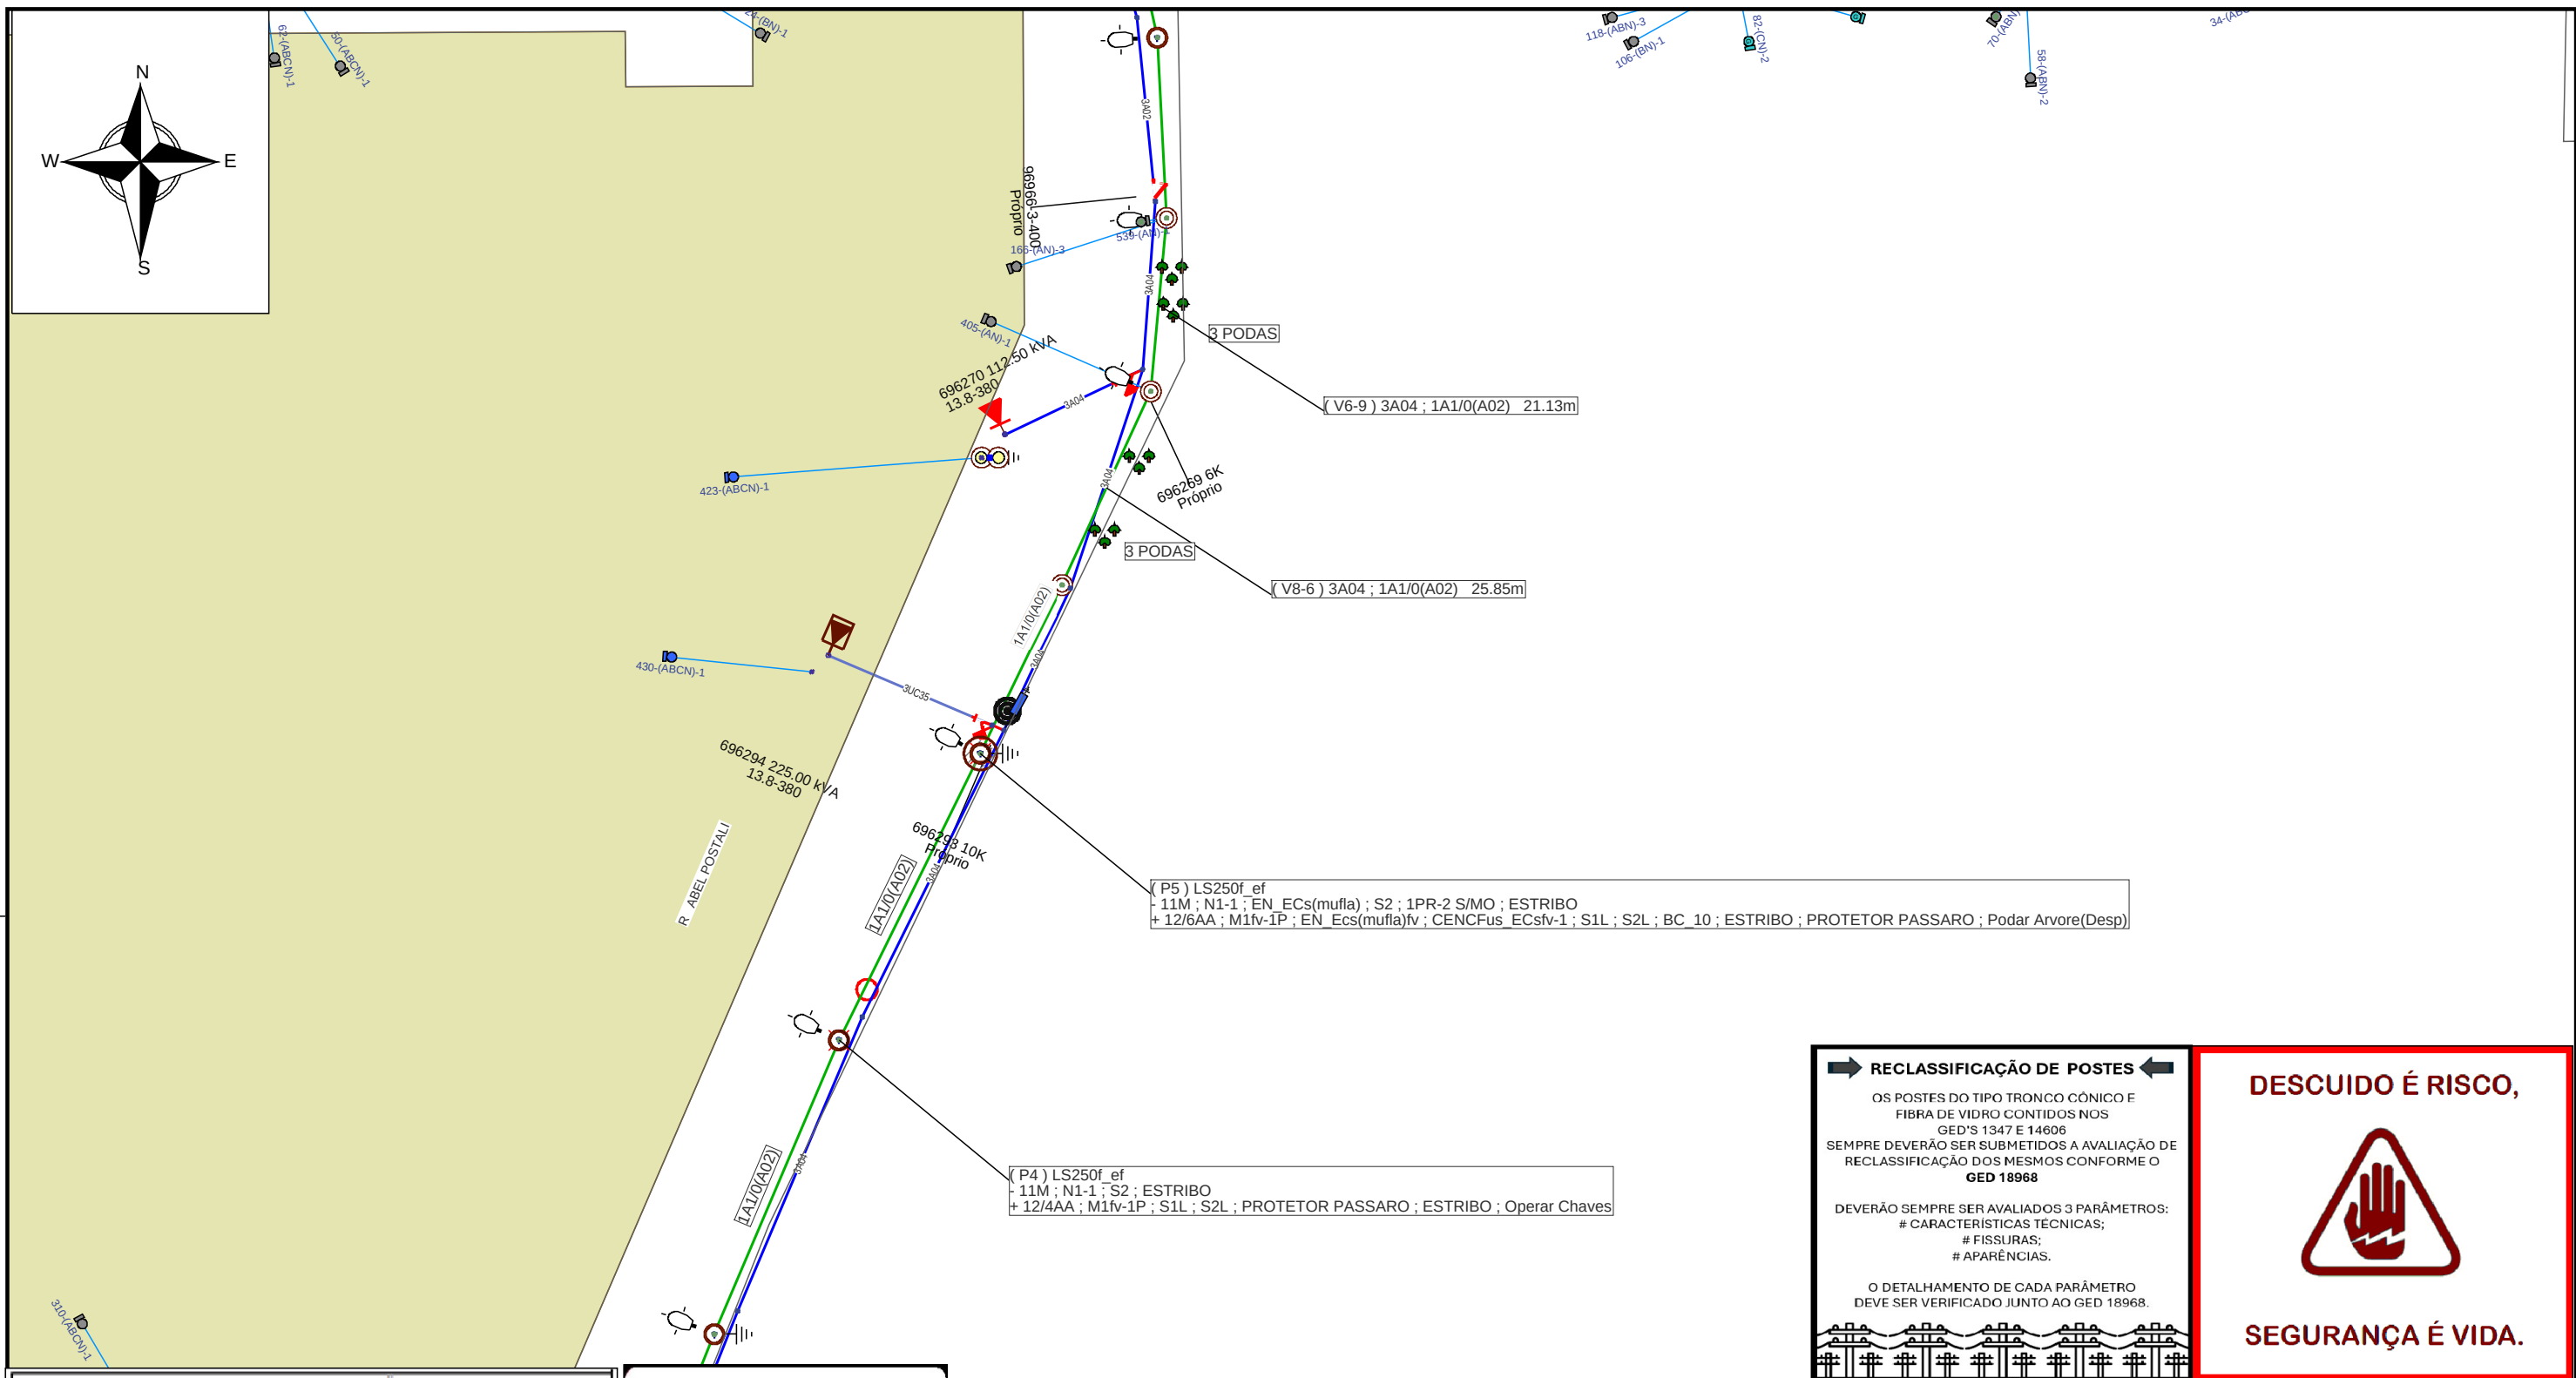

RECLASSIFICAÇÃO DE POSTES

OS POSTES DO TIPO TRONCO CÔNICO E FIBRA DE VIDRO CONTIDOS NOS GED'S 1347 E 14606 SEMPRE DEVERÃO SER SUBMETIDOS A AVALIAÇÃO DE RECLASSIFICAÇÃO DOS MESMOS CONFORME O GED 18968

DEVERÃO SEMPRE SER AVALIADOS 3 PARÂMETROS:

- # CARACTERÍSTICAS TÉCNICAS;
- # FISSURAS;
- # APARÊNCIAS.

O DETALHAMENTO DE CADA PARÂMETRO DEVE SER VERIFICADO JUNTO AO GED 18968.

DESCUIDO É RISCO,

SEGURANÇA É VIDA.

PLANO DE EXECUÇÃO					
Executar a obra seguindo todos os passos de segurança!					
SUBSTITUIR POSTES INDICADOS EM PLANTA SEGUINDO OS PROCEDIMENTOS DE SEGURANÇA					
Ação	Equipamento	Número	Clientes	Duração	CHI
Abrir	Religador	758133	3	5	15
Abrir	Chave Faca	96966			
Fechar	Religador	1047799			
Linha Viva?		Não	CHI TOTAL		15
☐ Poste novo a ser instalado (quando indicado em planta)					

FeedBack Para Fábrica de Projetos

Planeje
Use
Teste
Sinalize
Aterre

Breno Ardenghy
Breno Ardenghy Da Silva
Gerência de Processos de Obras e Manutenção | DROP
Técnico de Análise e Projetos
CFT: 03188101074

Gerência de Obras e Manutenção

Município: Caxias do Sul

Cliente: RGE SUL DISTRIBUIDORA DE ENERGIA S.A

Obra: Caxias do Sul 2025 - Insp Visual de Rede

Endereço: R ABEL POSTALI 430 CIDADE NOVA CAXIAS DO SUL

Responsável Técnico:	Eng. Ederson Paulo Vogel CREA: RS135794 ART: 10911826	Escala: 1:800	Data: 01/03/2025	Nota: 000006723382
		Classe de isolamento: 15kV	AL: CXH43	Folha 1
		Projetista: BRENO ARDENGHY	Projeto: 000007737268	Levantador: ALESSANDRO SEVERO DE OLIVEIRA