


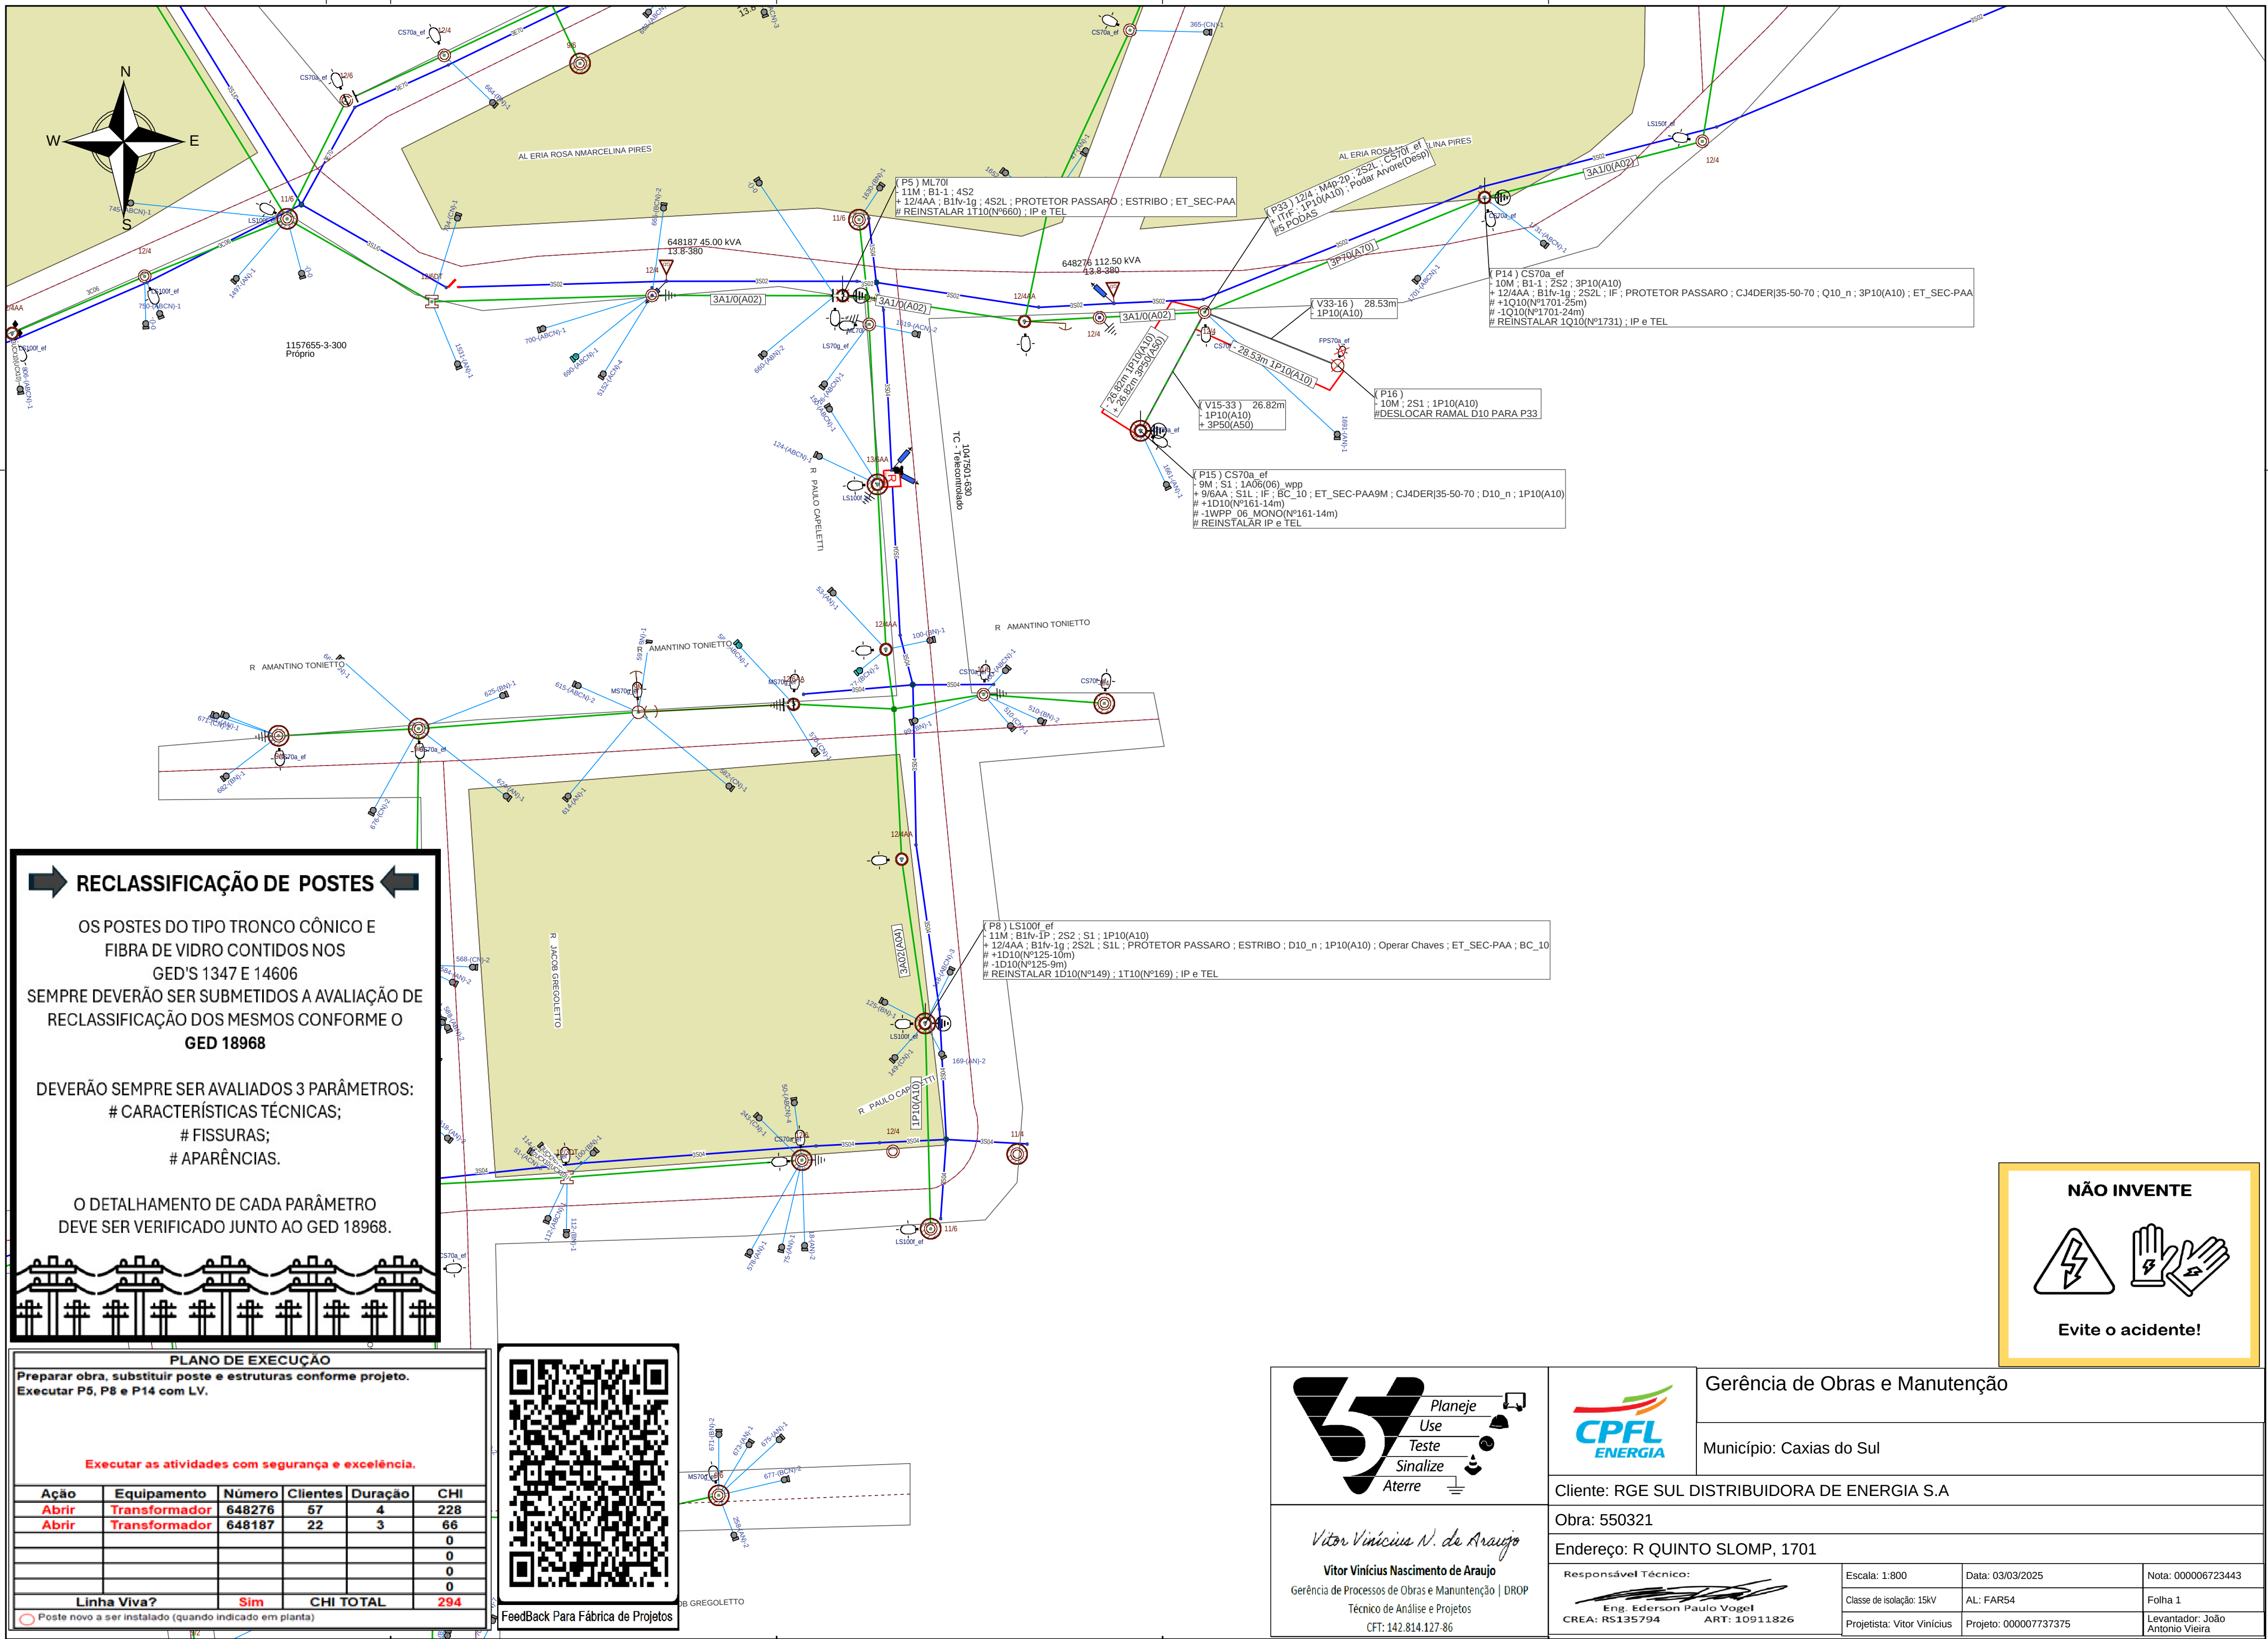

RECLASSIFICAÇÃO DE POSTES

OS POSTES DO TIPO TRONCO CÔNICO E FIBRA DE VIDRO CONTIDOS NOS GED'S 1347 E 14606 SEMPRE DEVERÃO SER SUBMETIDOS A AVALIAÇÃO DE RECLASSIFICAÇÃO DOS MESMOS CONFORME O GED 18968

DEVERÃO SEMPRE SER AVALIADOS 3 PARÂMETROS:
CARACTERÍSTICAS TÉCNICAS;
FISSURAS;
APARÊNCIAS.

O DETALHAMENTO DE CADA PARÂMETRO DEVE SER VERIFICADO JUNTO AO GED 18968.

PLANO DE EXECUÇÃO					
Preparar obra, substituir poste e estruturas conforme projeto. Executar P5, P8 e P14 com LV.					
Executar as atividades com segurança e excelência.					
Ação	Equipamento	Número	Clientes	Duração	CHI
Abrir	Transformador	648276	57	4	228
Abrir	Transformador	648187	22	3	66
					0
					0
					0
					0
Linha Viva?		Sim	CHI TOTAL		294
☐ Poste novo a ser instalado (quando indicado em planta)					

FeedBack Para Fábrica de Projetos

NÃO INVENTE

Evite o acidente!

Planeje
Use
Teste
Sinalize
Aterre

Gerência de Obras e Manutenção

Município: Caxias do Sul

Cliente: RGE SUL DISTRIBUIDORA DE ENERGIA S.A

Obra: 550321

Endereço: R QUINTO SLOMP, 1701

Responsável Técnico:

Eng. Ederson Paulo Vogel
CREA: RS135794 ART: 10911826

Escala: 1:800
Classe de isolamento: 15KV
Projetista: Vitor Vinicius

Data: 03/03/2025
AL: FAR54
Projeto: 000007737375

Nota: 000006723443
Folha 1
Levantador: João Antonio Vieira

Vitor Vinicius N. de Araujo
Gerência de Processos de Obras e Manutenção | DROP
Técnico de Análise e Projetos
CFT: 142.814.127-86