


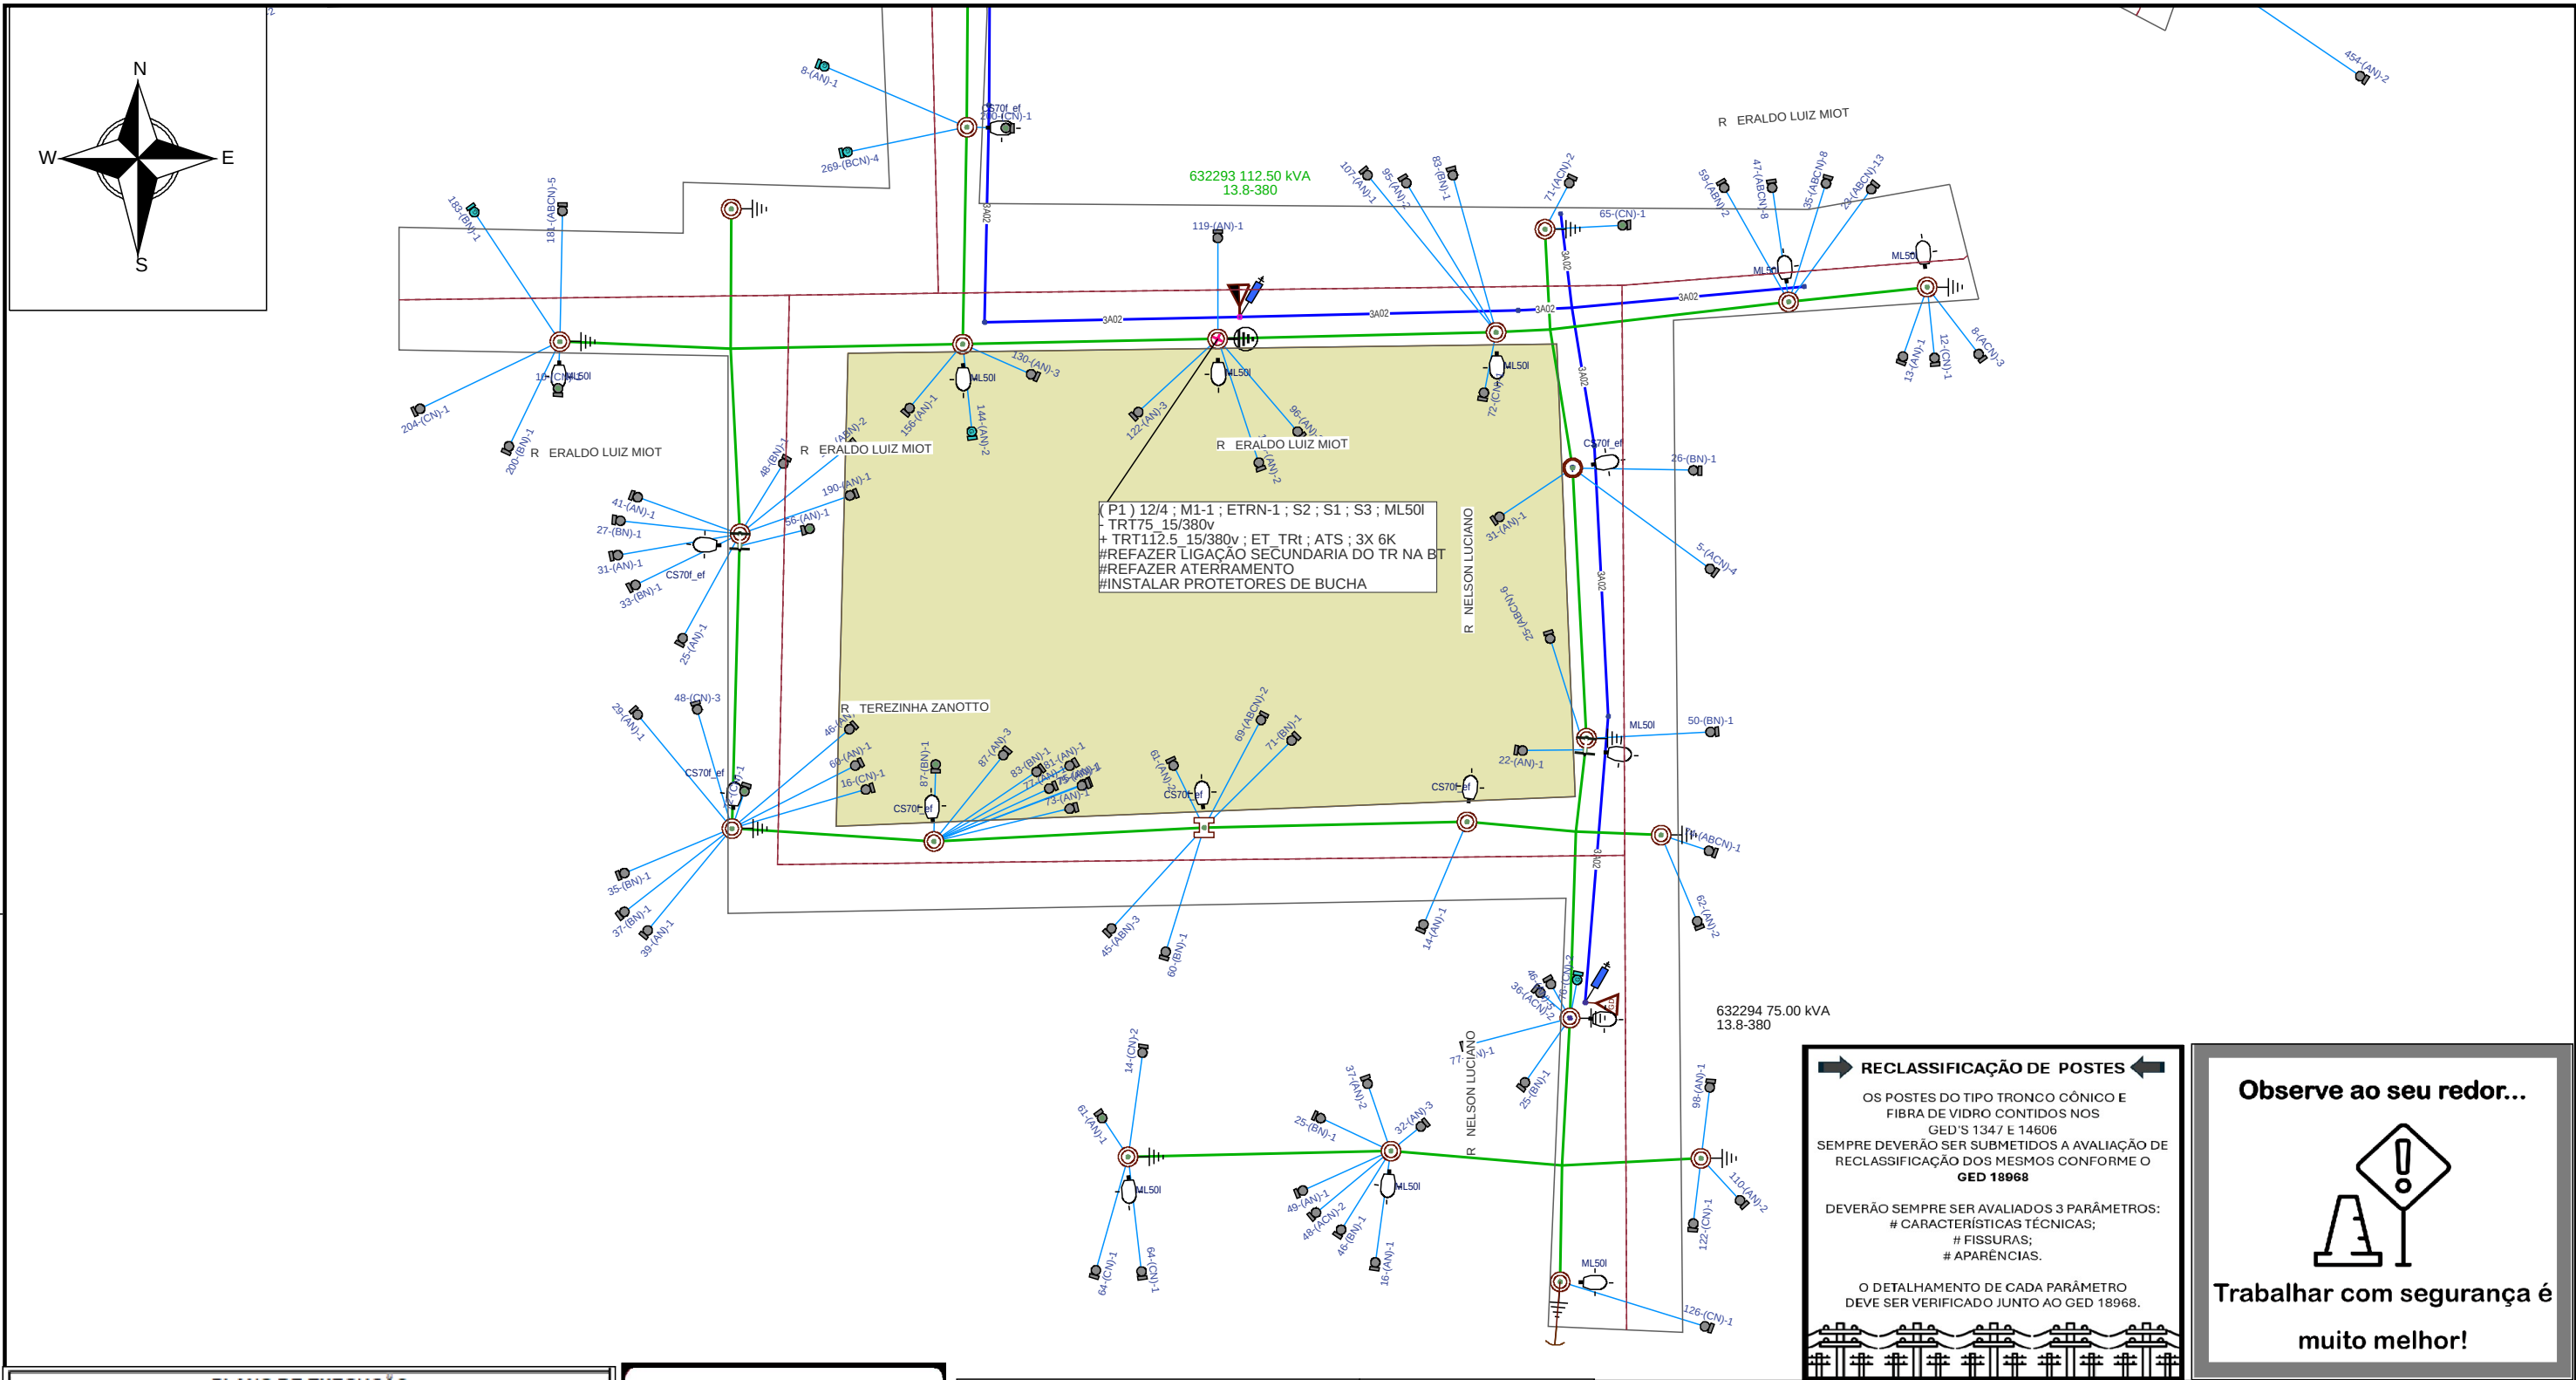

PLANO DE EXECUÇÃO					
Abrir equipamento abaixo para executar a substituição do TR.					
Ação	Equipamento	Número	Clientes	Duração	CHI
Abrir	Transformador	632293	90	5	450
Linha Viva?		Não	CHI TOTAL		450
☐ Poste novo a ser instalado (quando indicado em planta)					

FeedBack Para Fábrica de Projetos

Planeje
Use
Teste
Sinalize
Aterre

Pietro Vargas Passos
Gerência de Processos de Obras e Manutenção | DROP
Técnico de Análise e Projetos
CFT: 04787663003

Gerência de Obras e Manutenção
Município: Caxias do Sul

Cliente: RGE SUL DISTRIBUIDORA DE ENERGIA S/A

Obra: Plano Sobrecarga 2025

Endereço: Caxias do Sul BR RS

Responsável Técnico:

Eng. Ederson Paulo Vogel
CREA: RS135794 ART: 10911826

Escala: 1:850
Classe de isolamento:
15kV
Projetista: Pietro Vargas

Data: 13/11/2025
AL: CXA15
Projeto: 000007926708

Nota:
000006783017
Folha 1
Levantador