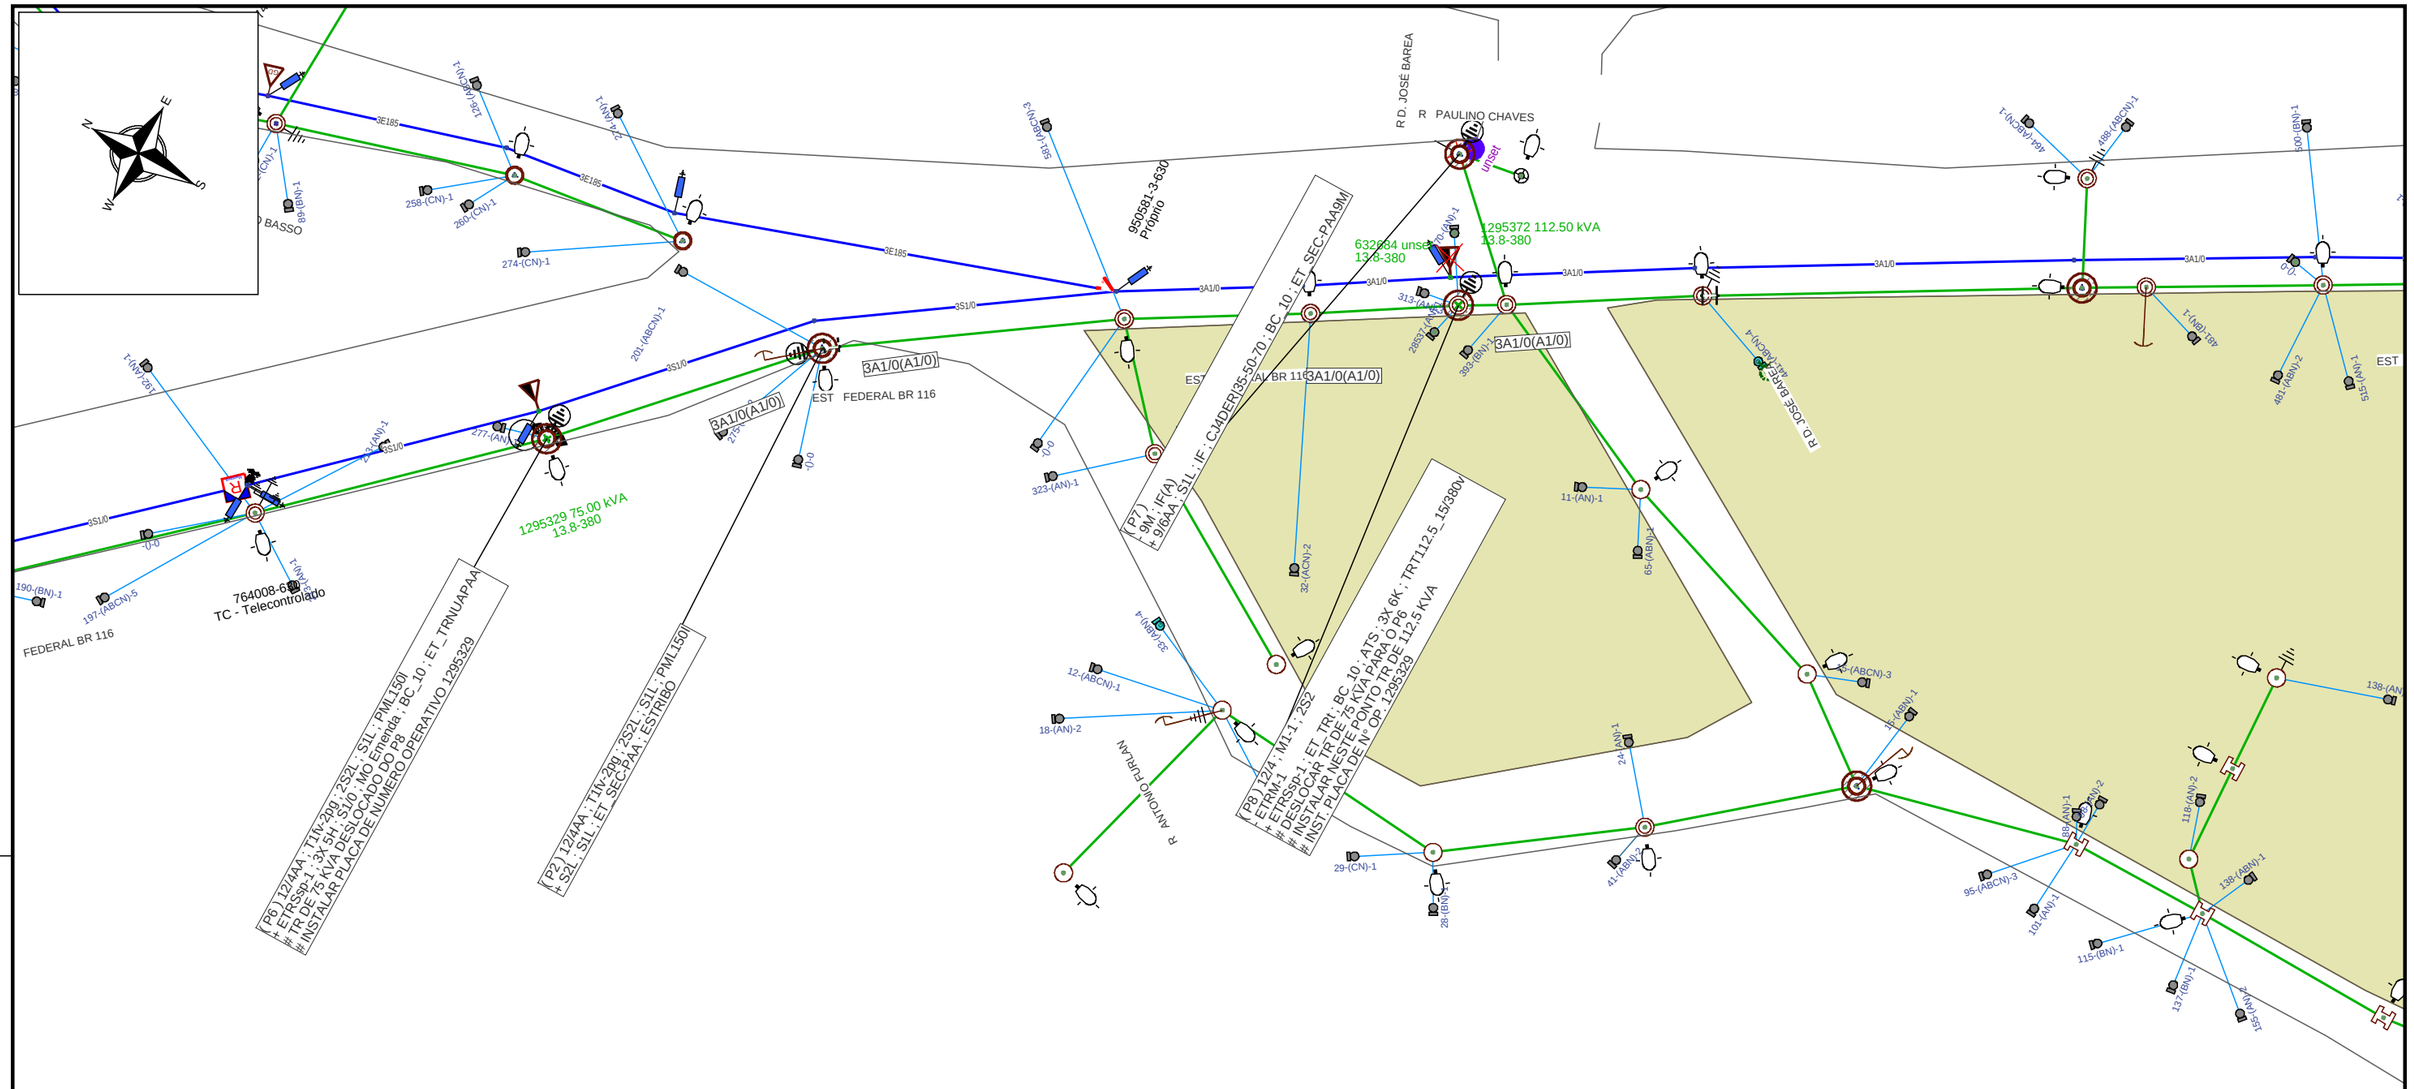

Na preparação abrir cava + implantar poste + passar rede para poste novo + retirar postes velhos Instalar + (Desligar TR 632684)

O DEC EM ESTUDO PODE SER OTIMIZADO EM ATÉ 1317,5 CHI | Quantidade de equipes sugeridas para o desligamento | 0 | 0

Equipamento Desligado	Número Operativo	Clientes Desligados	Duração da intervenção	CHI Total	Observações (se necessário)
TRANSFORMADOR	632684	94	4	376	
ESTUDO DE CHI			Total	376	

Buscar Dados | Busca Eq Pai | Criar Arvore | Pesquisa DIB | Acionar Medição (ATR)

RE: 4000535 — Base interna de dados 27/04/2025

Técnico: ADELAR MIGUEL FERREIRA GRAFE — Data da análise: 01/12/2025

RECLASSIFICAÇÃO DE POSTES

OS POSTES DO TIPO TRONCO CÔNICO E FIBRA DE VIDRO CONTIDOS NOS GED'S 1347 E 14606 SEMPRE DEVERÃO SER SUBMETIDOS A AVALIAÇÃO DE RECLASSIFICAÇÃO DOS MESMOS CONFORME O **GED 18968**

DEVERÃO SEMPRE SER AVALIADOS 3 PARÂMETROS:
CARACTERÍSTICAS TÉCNICAS;
FISSURAS;
APARÊNCIAS.

O DETALHAMENTO DE CADA PARÂMETRO DEVE SER VERIFICADO JUNTO AO GED 18968.

Seja a mudança que você quer ver na segurança do trabalho.

FeedBack Para Fábrica de Projetos

5S: Planeje, Use, Teste, Sinalize, Aterre

Henrique Silva Erguy Junior
Gerência de Processos de Obras e Manutenção | DROP
Técnico de Análise Projetos I
CFT: 528754740 4-9

CPFL ENERGIA

Gerência de Obras e Manutenção

Município: Caxias do Sul

Cliente: RIO GRANDE ENERGIA S.A.

Obra: Plano Sobrecarga 2025

Endereço: 632684

Responsável Técnico:
Eng. Ederson Paulo Vogel
CREA: RS135794 ART: 10911826

Escala: 1:850	Data: 07/07/2025	Nota: 000006783037
Classe de isolação: 15kV	AL: CXG25	Folha 1
Projetista: HENRIQUE ERGUY	Projeto: 000007828082	Levantador ADELAR GRAFE